

From One Continuous Spine to Five Urban Relation Transects

ONE CONTINUOUS SPINE TO FIVE URBAN RELATION TRANSECTS DESIGN RESPONSE WINDOWS FOR THREE KEY AREAS


30 SEC | READ THE PROPOSITION

The Jing-Zhang public space spine is becoming continuous

but its transverse public relations with the city on both sides have not followed


URBAN RELATION TRANSECTS

The key transverse transect is the design unit for reorganising urban relations.


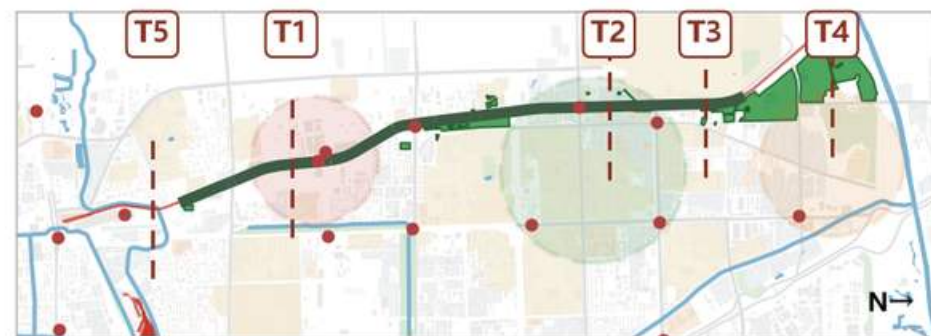


— Jing-Zhang public space main axis — Relation transects T1-T5
 Response window (indicative extent, not equivalent to the official key-area boundary)

3 MIN | READ THE METHOD

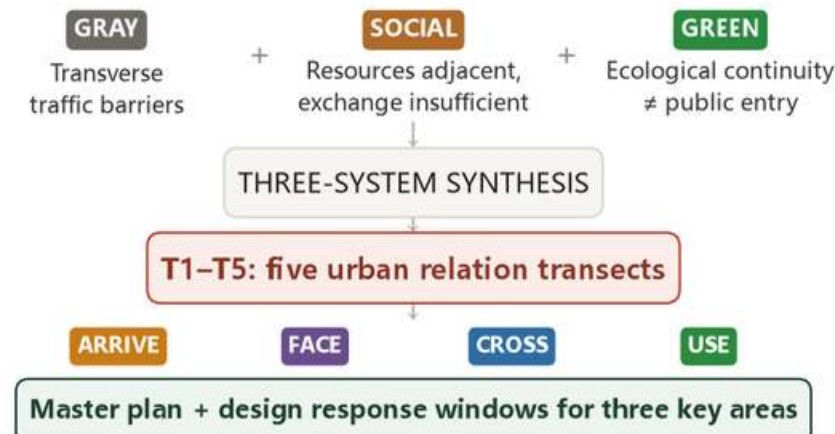

15 MIN | READ THE DESIGN

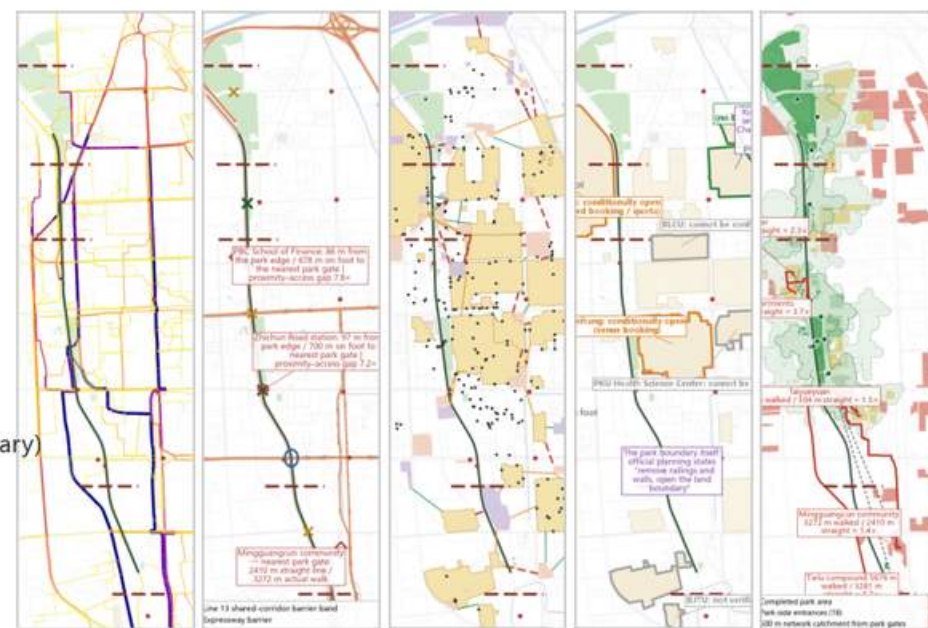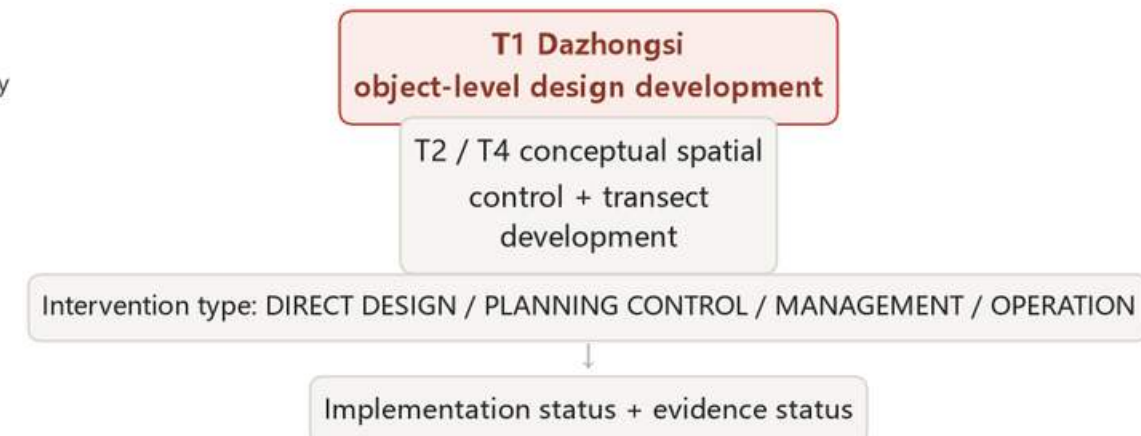

Gray · walking network · Gray · crossing barriers · Social · campus permeability · Green · real accessibility



✓ VERIFIED

Existing objects, plan relations, walking evidence

○ DESIGN-DEFINED


Relation reorganisation, spatial strategy, design intervention

△ TO VERIFY

Exact levels, tenure, opening and engineering conditions

— NOT PROPOSED AT THIS STAGE

Statutory land-use change, unverified new engineering crossing

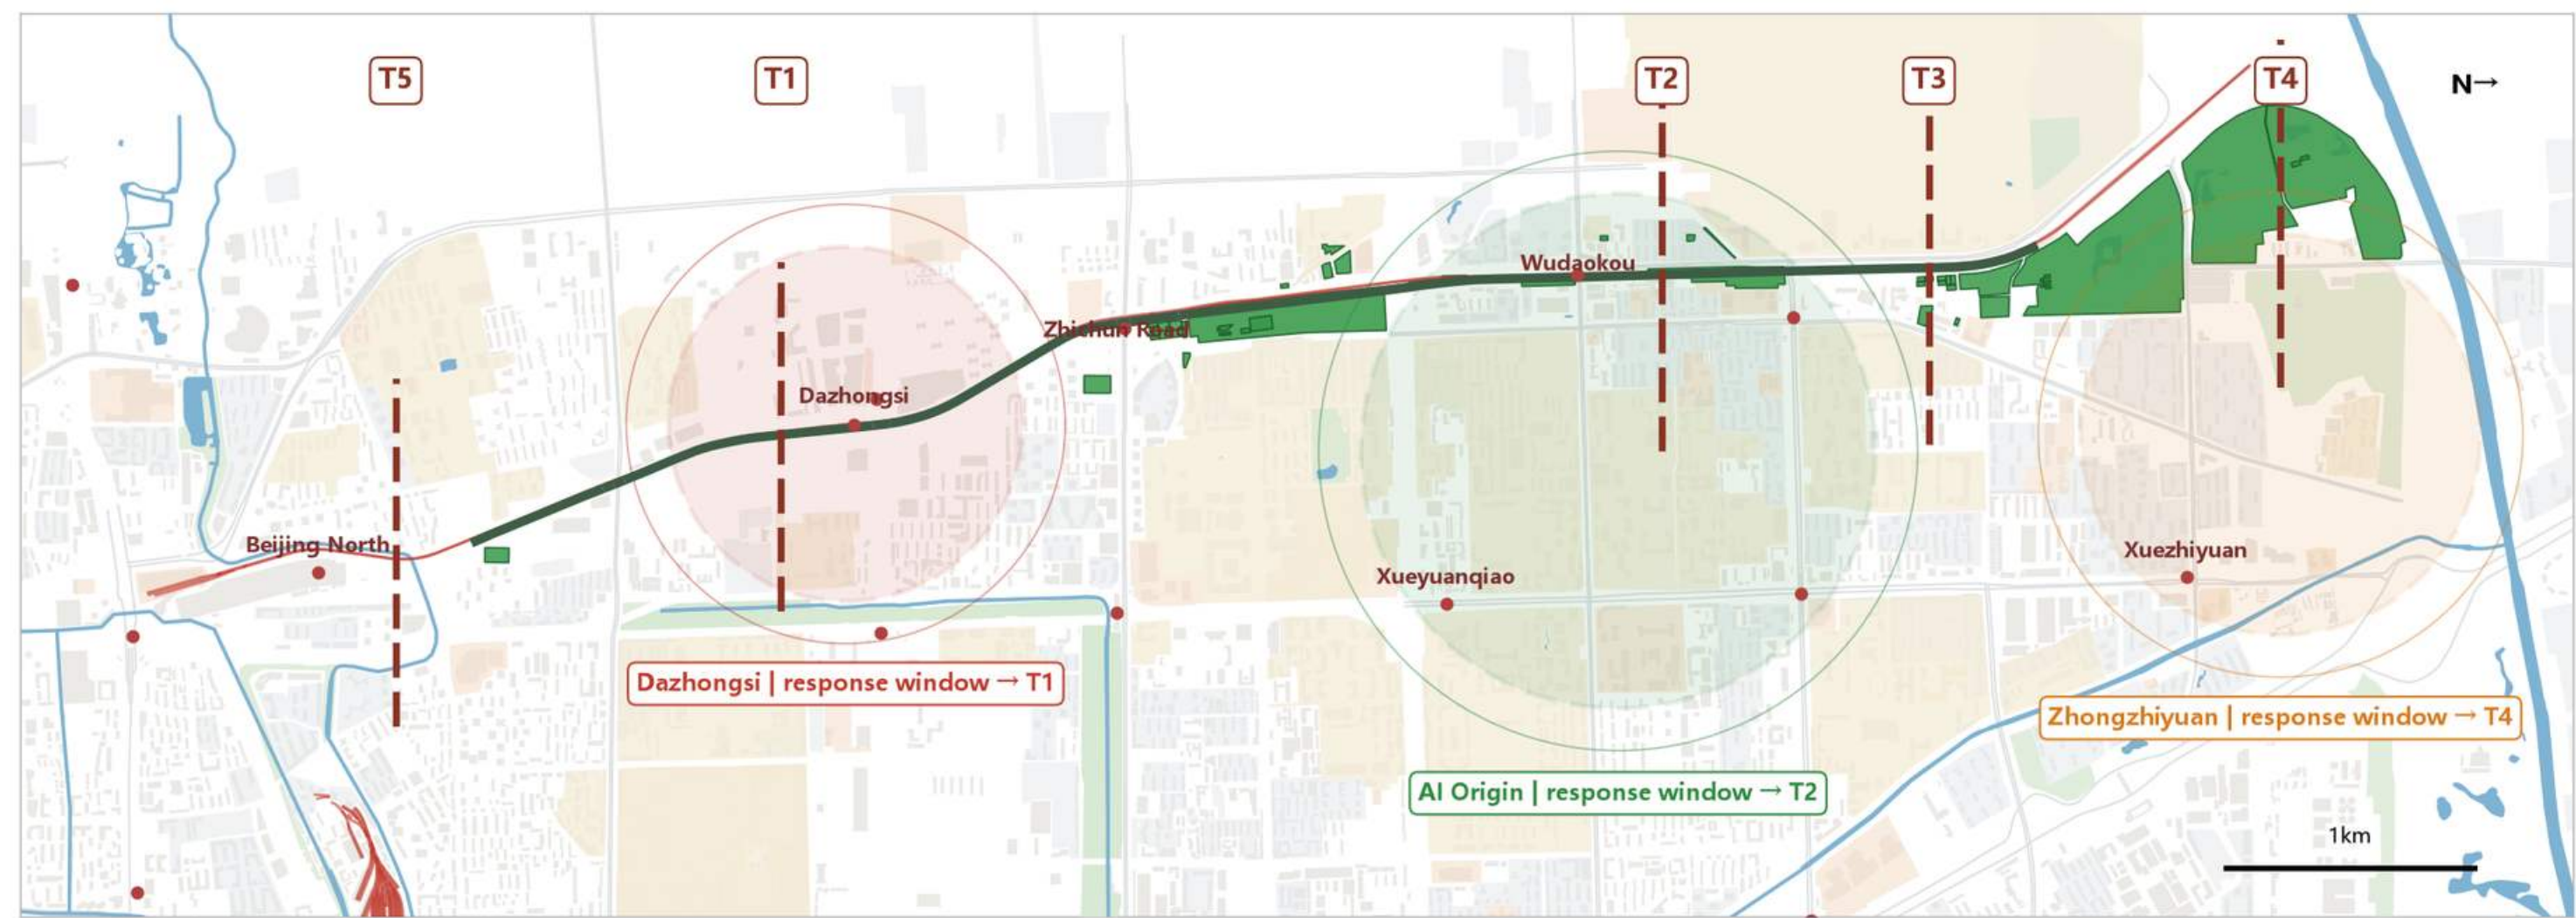

- Jing-Zhang public space main axis (relation belt)
- Relation transects T1-T5
- Dazhongsi | response window → T1
- AI Origin | response window → T2 (the T3 campus edge as adjacent context)
- Zhongzhiyuan | response window → T4
- Rail stations (T5 = the Beijing North terminus gateway, a controlling transect)

DESIGN CONCEPT

URBAN RELATION TRANSECT

Along the continuous Jing-Zhang spine we identify the key transverse positions where relational conflicts concentrate, take the **ARRIVE**ct as the **FACE**gn unit, a **CROSS**rganise the **USE**rbn

The four relation types are the key to the Jing-Zhang spine, but they are not the concept of this proposal itself. must reorganise; they are not the concept of this proposal itself. on both sides again

Five urban relation transects identify the typical problems along the line; the focused responses are set out in the design response windows for the three key areas

One continuous spine × five relation transects × differentiated relation reorganisation

Response window | a key design location identified by this proposal along Jing-Zhang; not equivalent to the official key-area extent.



- Jing-Zhang heritage alignment (the spine)

Line 13 + operating corridor
- High-speed at-grade section / yard tracks

Beijing North rail yard
- Military administration area

Expressway / arterial road
- Crossing · walkable (3)

Crossing · conditions TO VERIFY (3)
- North Third Ring overpass (grade-separated node)


Relation transects T1–T5

The same facilities that carry movement are the ones that create the division.

The Line 13 shared corridor, the North Third and Fourth Ring expressways, the Beijing North rail yard and the at-grade high-speed section together form the north–south movement network along the line — and at the same time the principal east–west barrier. The seven existing crossings fall into three classes by level

of verification: three are walkable, three have conditions still to verify, and the North Third Ring is

The transport infrastructure that carries north–south movement is also the transverse barrier to east–west urban relations.
the grade-separated node where Jing-Zhang passes over the expressway.

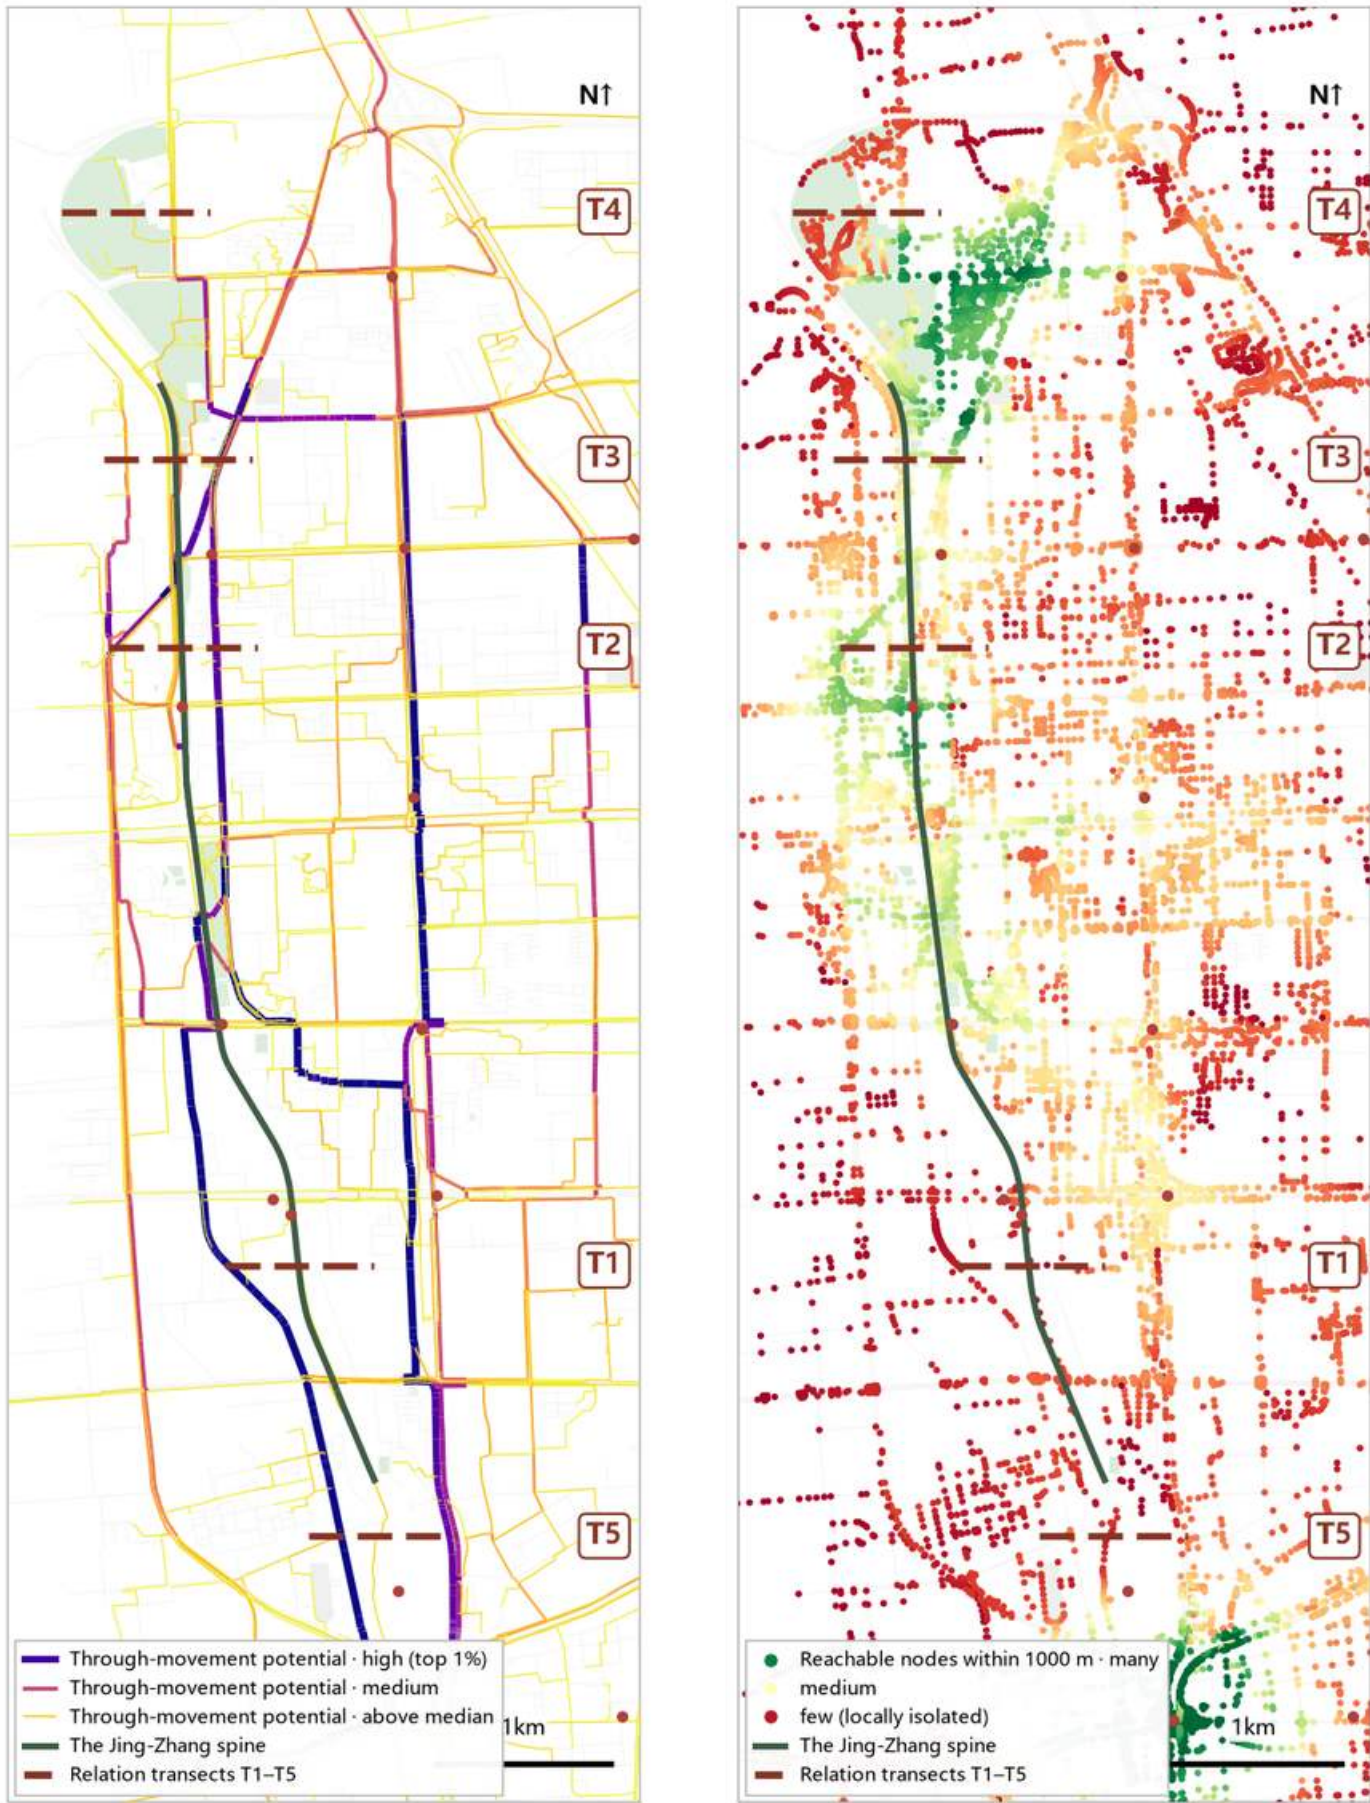


① Through-movement potential (proxy indicator) ② Local connection scale (proxy indicator)

Two drawings, two different questions


① Through-movement potential: which streets carry movement across the whole network? — Jing-Zhang is not currently a main through route; only a few east-west streets, such as Chengfu Road and Zhichun Road, score high. ② Local connection scale: how many streets can be reached within 1000 m of each position? — Large blocks of low values appear around the university compounds and the rail yard.

The network is continuous,
but structural accessibility is not even.


Limits of use: these are project-defined proxy indicators (not standard space syntax) and cannot be used to infer actual pedestrian flow; they provide the network-structure basis for the station access question that follows, while planning judgements rest on real walking evidence.

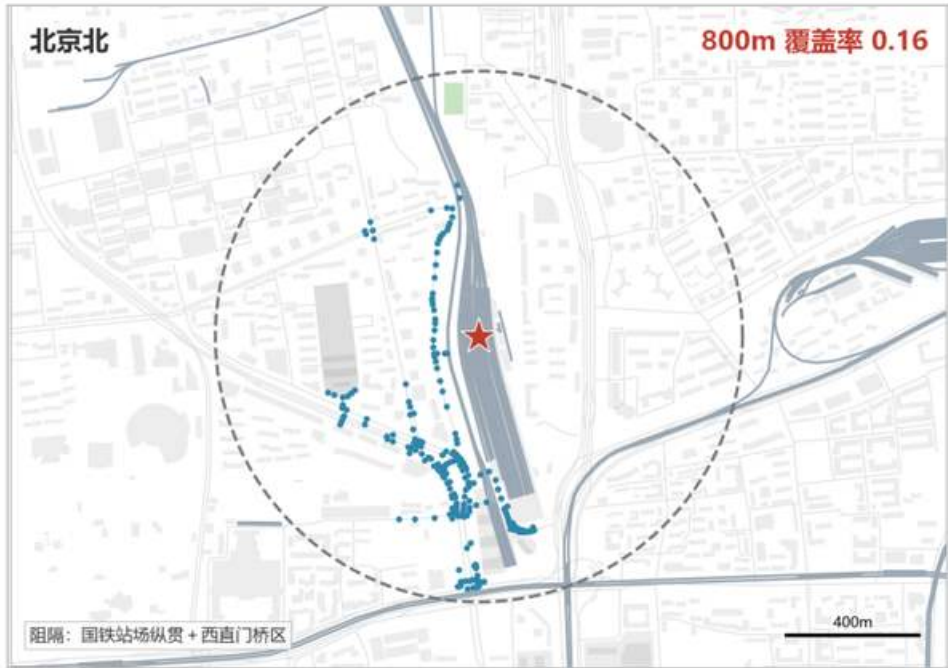

01 Beijing North | catchment ratio 0.16

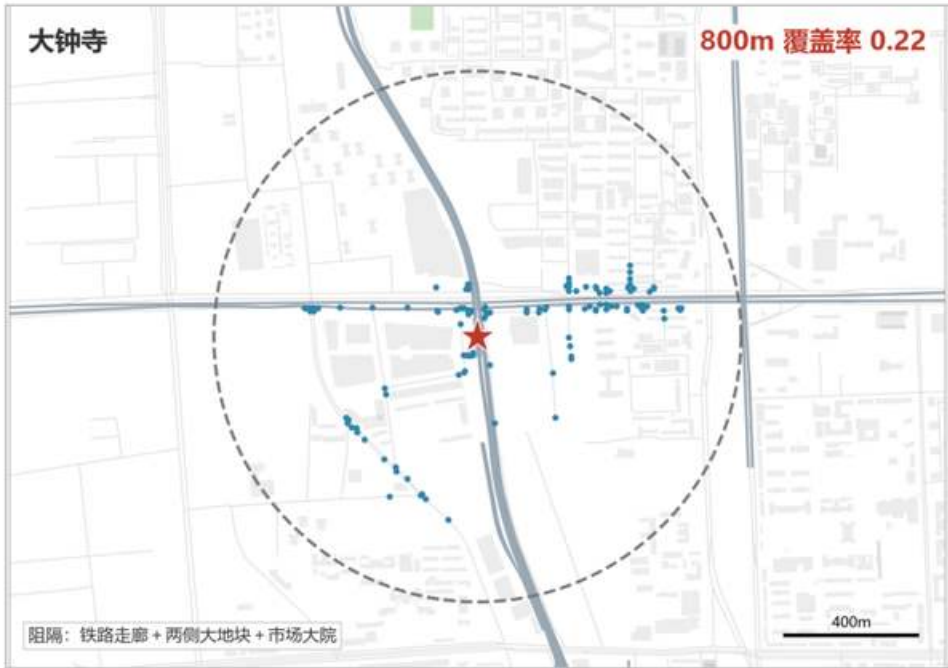


02 Dazhongsi | catchment ratio 0.22

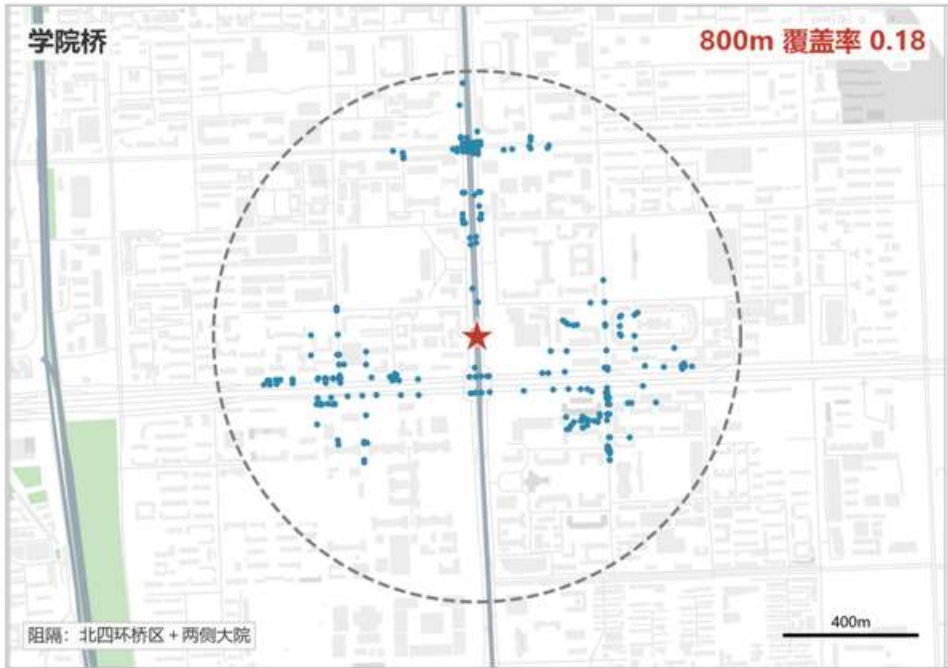


03 Xueyuanqiao | catchment ratio 0.18



04 Wudaokou | catchment ratio 0.58 (control)

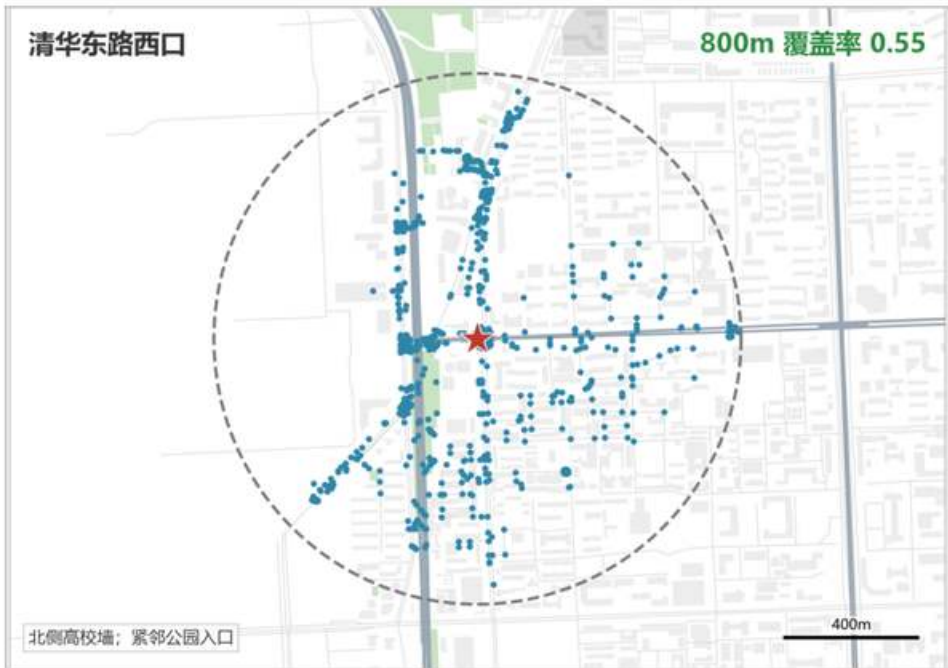

05 Tsinghua East Road West | catchment ratio 0.55 (park-side entrance)

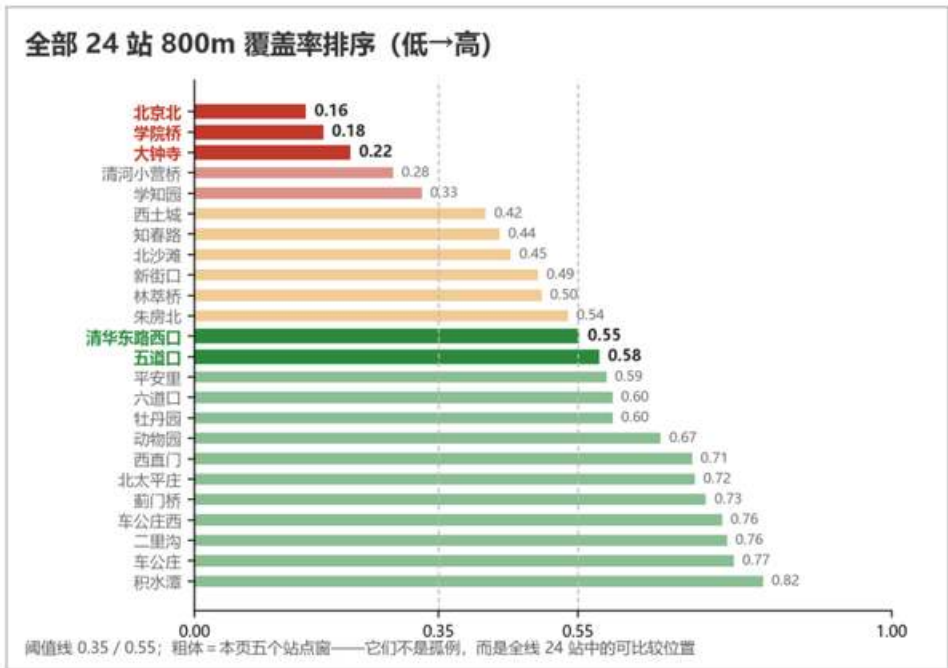

06 All 24 stations by catchment ratio (low → high)


A Station ≠ Real Access

There is a clear gap between the standard 800 m catchment and the real walking network.


Reading the drawing

Beijing North 0.16, Xueyuanqiao 0.18, Dazhongsi 0.22: actual reachable coverage is markedly low — enclosed by the railway and large compounds and bridge zones, the blue nodes cluster in only a few directions. Wudaokou 0.58 and Tsinghua East Road West 0.55 are relatively high: where the street grid is fine-grained or the station sits beside a park entrance, the catchment stays largely intact. Low values are not general; they are produced by specific barriers. The number of stations alone does not represent the real public access capacity along Jing-Zhang. The ranking of all 24 stations shows the low values concentrated in the southern section and at bridge-zone stations.

Method / data: the grey dashed circle is the standard 800 m radius around each station; the blue dots are street nodes actually reachable within 800 m along the OSM walking network; the catchment ratio is reachable nodes ÷ all street nodes inside the standard circle (a project-defined network-permeability indicator, not a standard TOD metric; it says nothing about ridership or intensity of use); and the walking network is the most complete public domain walking network available in the open public space of the existing network).

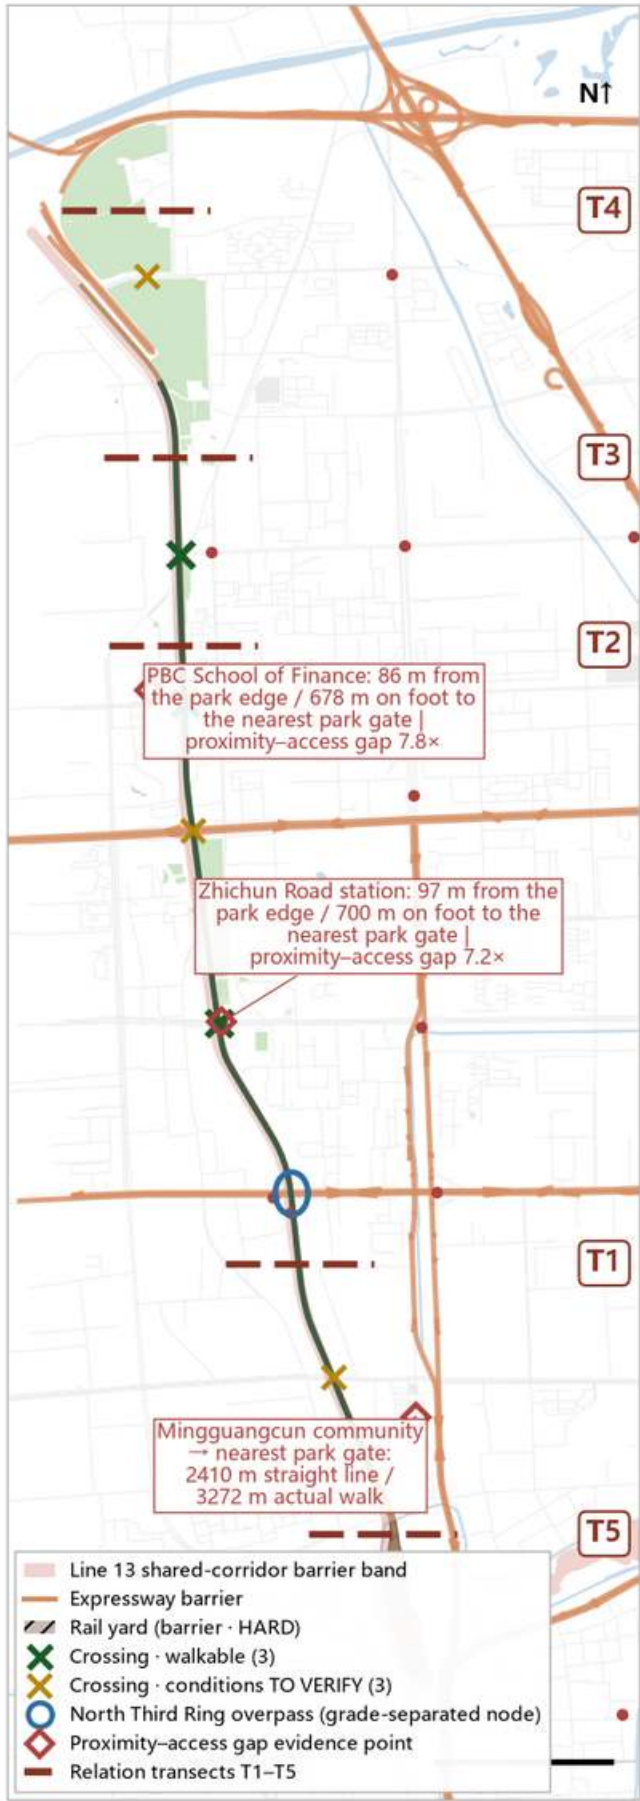

North Third Ring grade-separated node + walked verification on the T1 segment (geometric proximity vs real access)

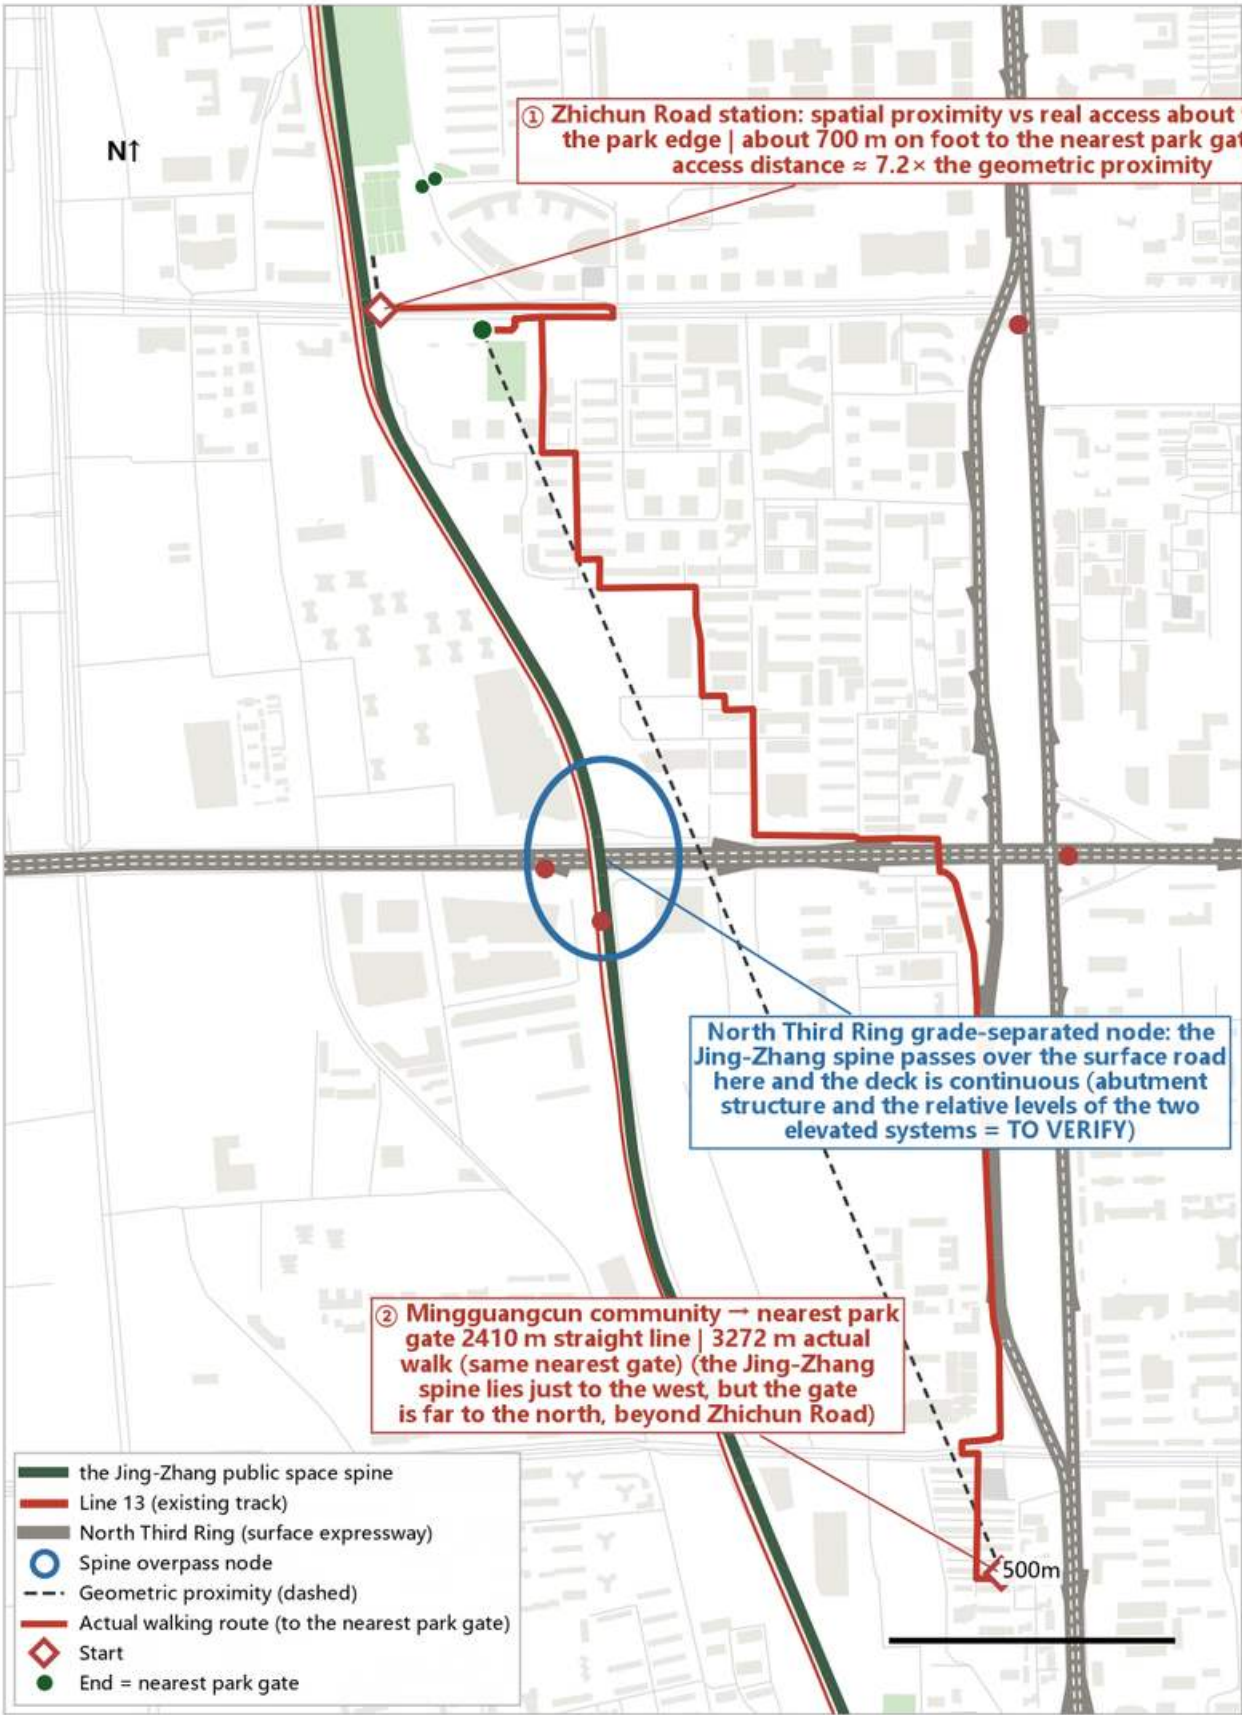


Cannot cross the line

The Line 13 shared corridor, the expressways and the rail yard form HARD barriers. Of the seven existing crossings, three are walkable but purely traffic-shaped, three have conditions still to verify, and the North Third Ring is the node where the spine passes over the expressway. Walked verification: Zhichun Road station is about 97 m from the park edge but about 700 m on foot to the nearest gate — roughly 7.2× the geometric proximity. Mingguangcun community **Crossings are not lacking along the line, but real transverse barriers remain in several segments.**

Together with the station-access page these form two independent evidence chains: previous page = cannot reach the station; this page = cannot cross the line.

So close, yet unreachable: crossings exist at only a few points and are mostly purely traffic-shaped. The 7.2× figure is a proximity-access gap (the two legs have different end points, so it is not a strict detour ratio). Data: the detour table and shortest paths on the walking network

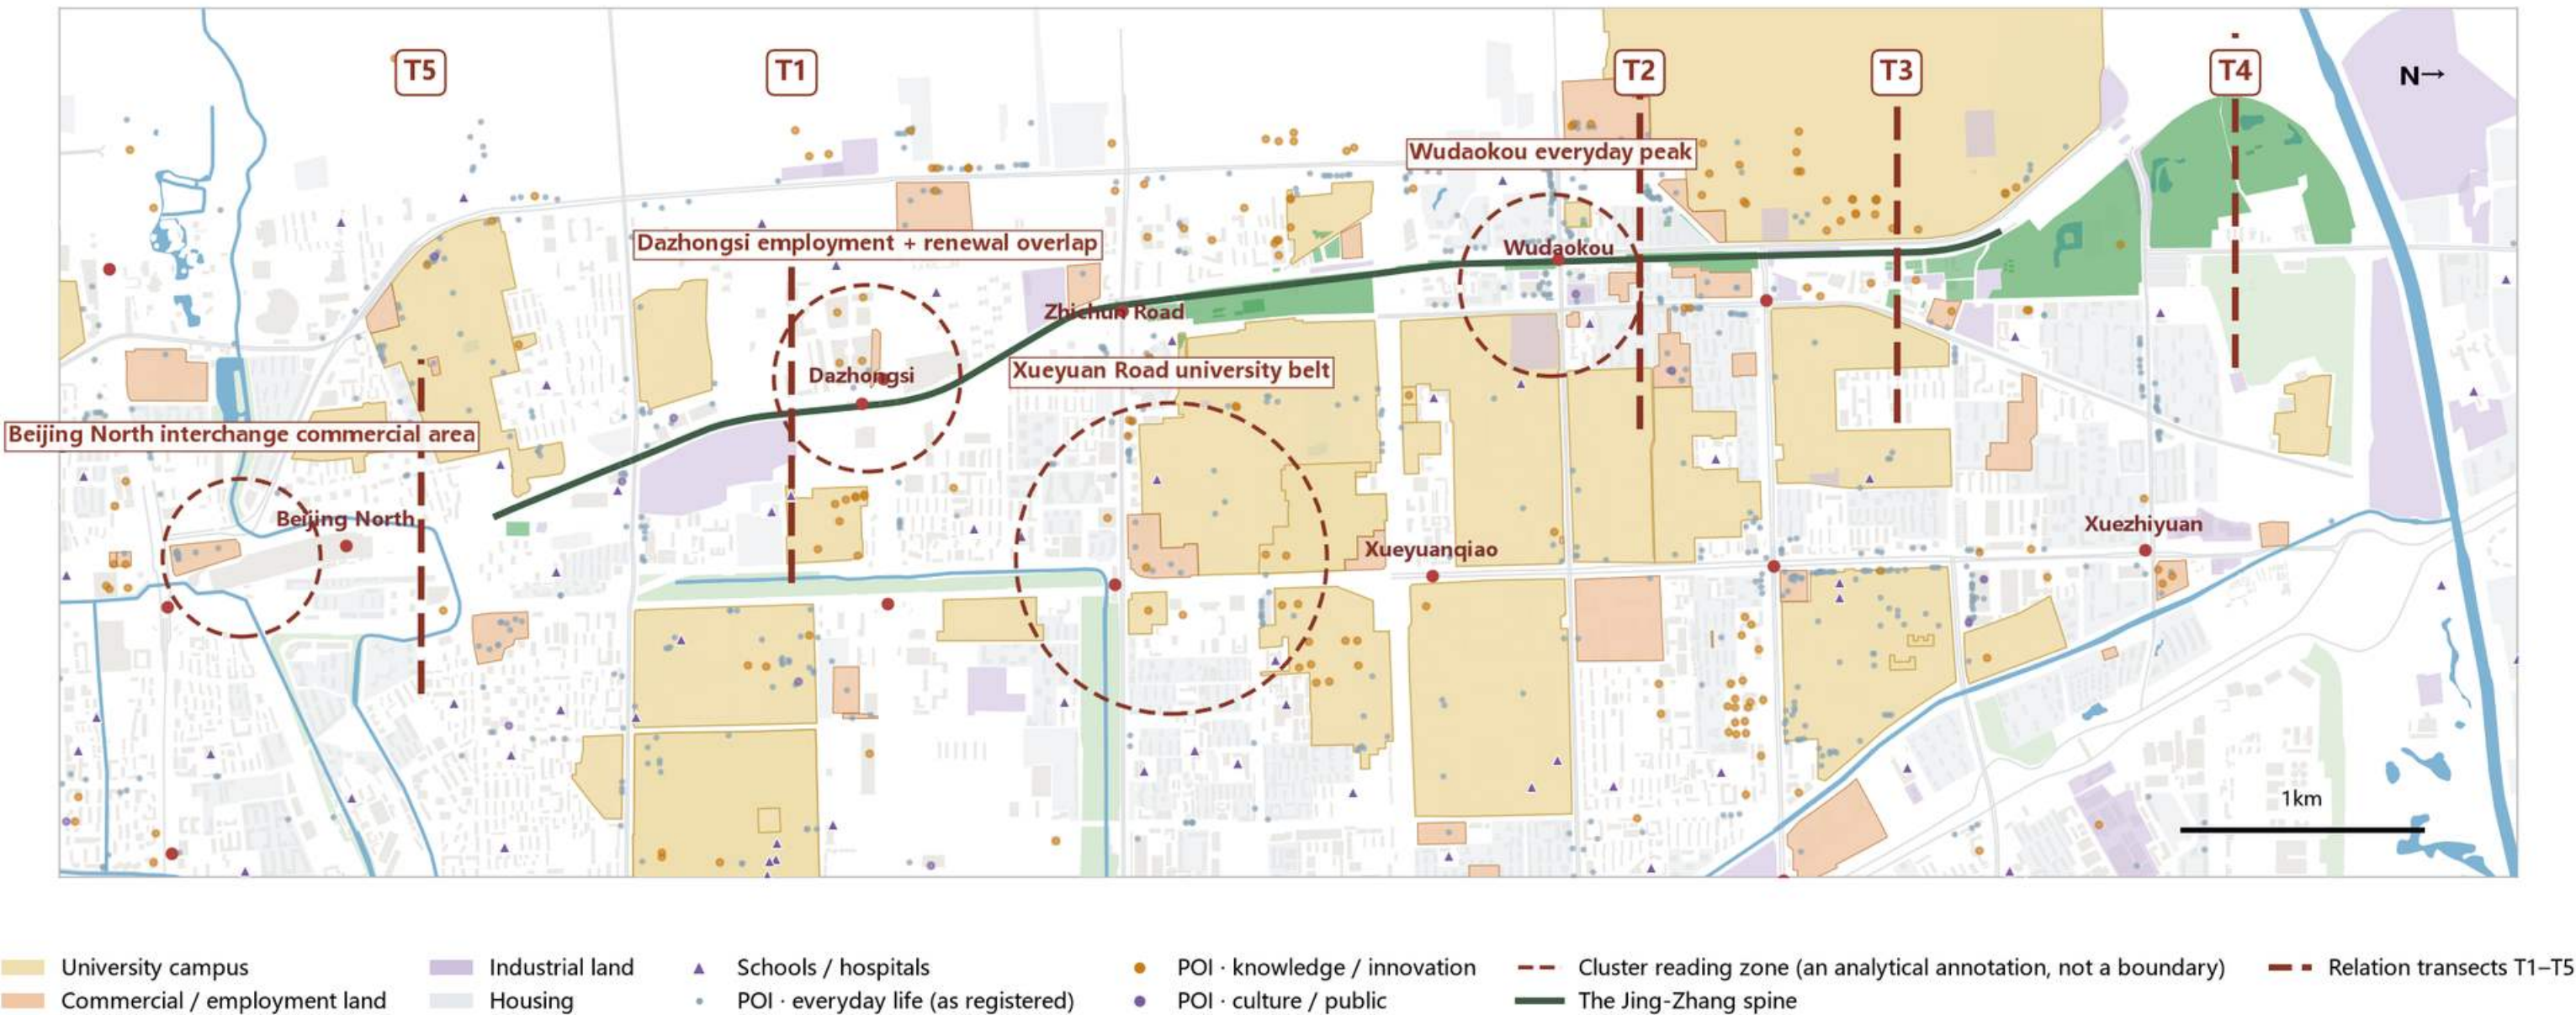


Four clusters; three of them touch the corridor.

Universities, research, translation services, industrial parks, communities and everyday services cluster strongly along the line. POI data show registered distribution only and do not represent intensity of use. The next three pages test, in turn: real access between

residents and services; the physical permeability and opening conditions of the universities; and the conditions for public exchange between innovation resources.

The problem with social infrastructure is not a shortage of facilities but a mismatch in the conditions of access, openness and exchange.

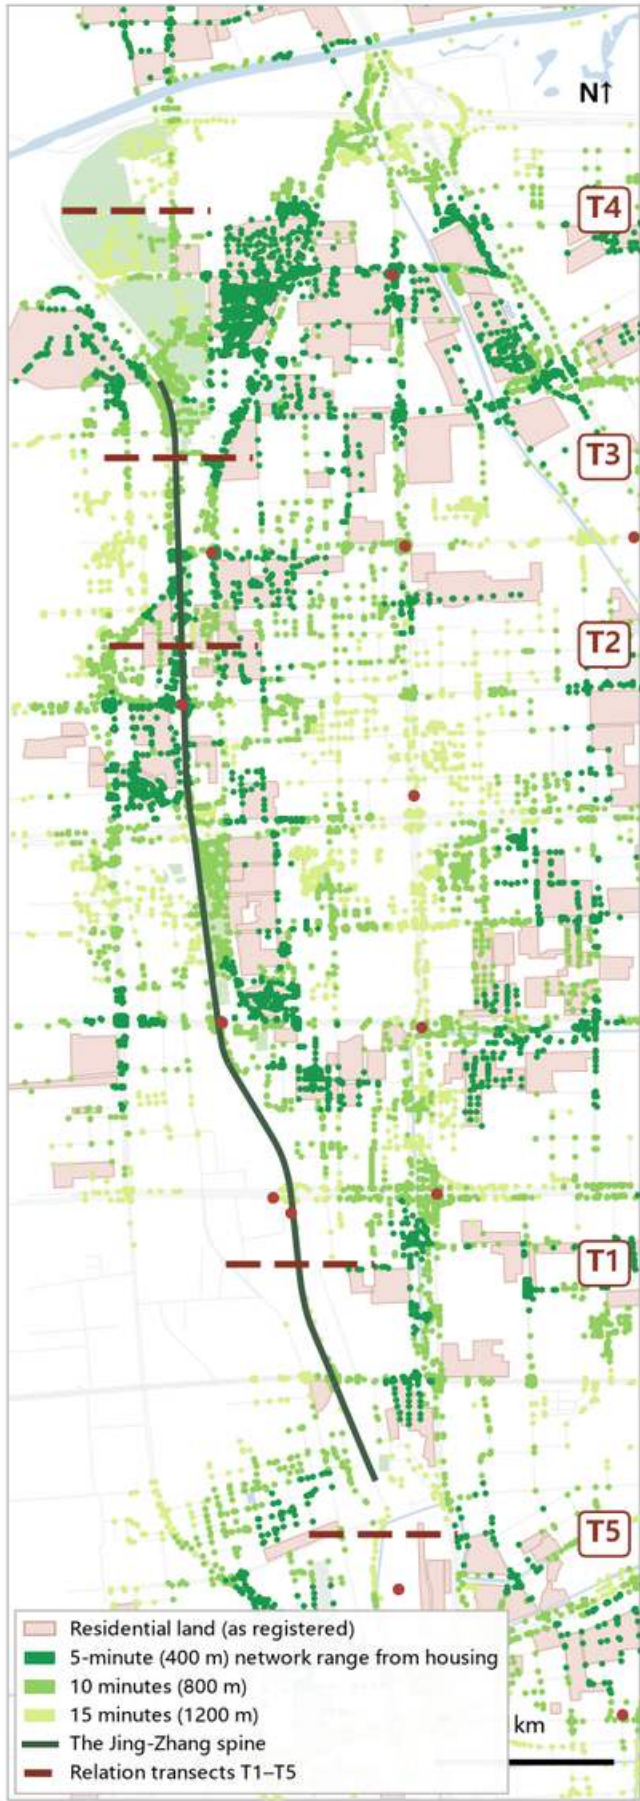

Secondary tests (same size, top-aligned)



Test ① | number of service types reachable within 15 minutes (0-5, red = low)



Test ② | healthcare within 1200 m (red = not covered: the northern area is weaker)



Test ③ | education within 1200 m (negative result: no new gap found)


Facilities are not scarce; the mismatch is in real walking

Measured as a 15-minute neighbourhood, the total provision along the line is not short; only the northern area is weaker on healthcare, and the education check found no new gap. The mismatch appears on the walking network: around the completed section the isochrones are whole and continuous, while for housing across the tracks or against the expressway they are cut into fragments. For some of these areas the actual walk to the nearest public

space is three to four times the straight-line distance.

The problem is not a shortage of services but a mismatch between where facilities are and what can actually be reached on foot.

The 15-minute neighbourhood (on the real walking network)

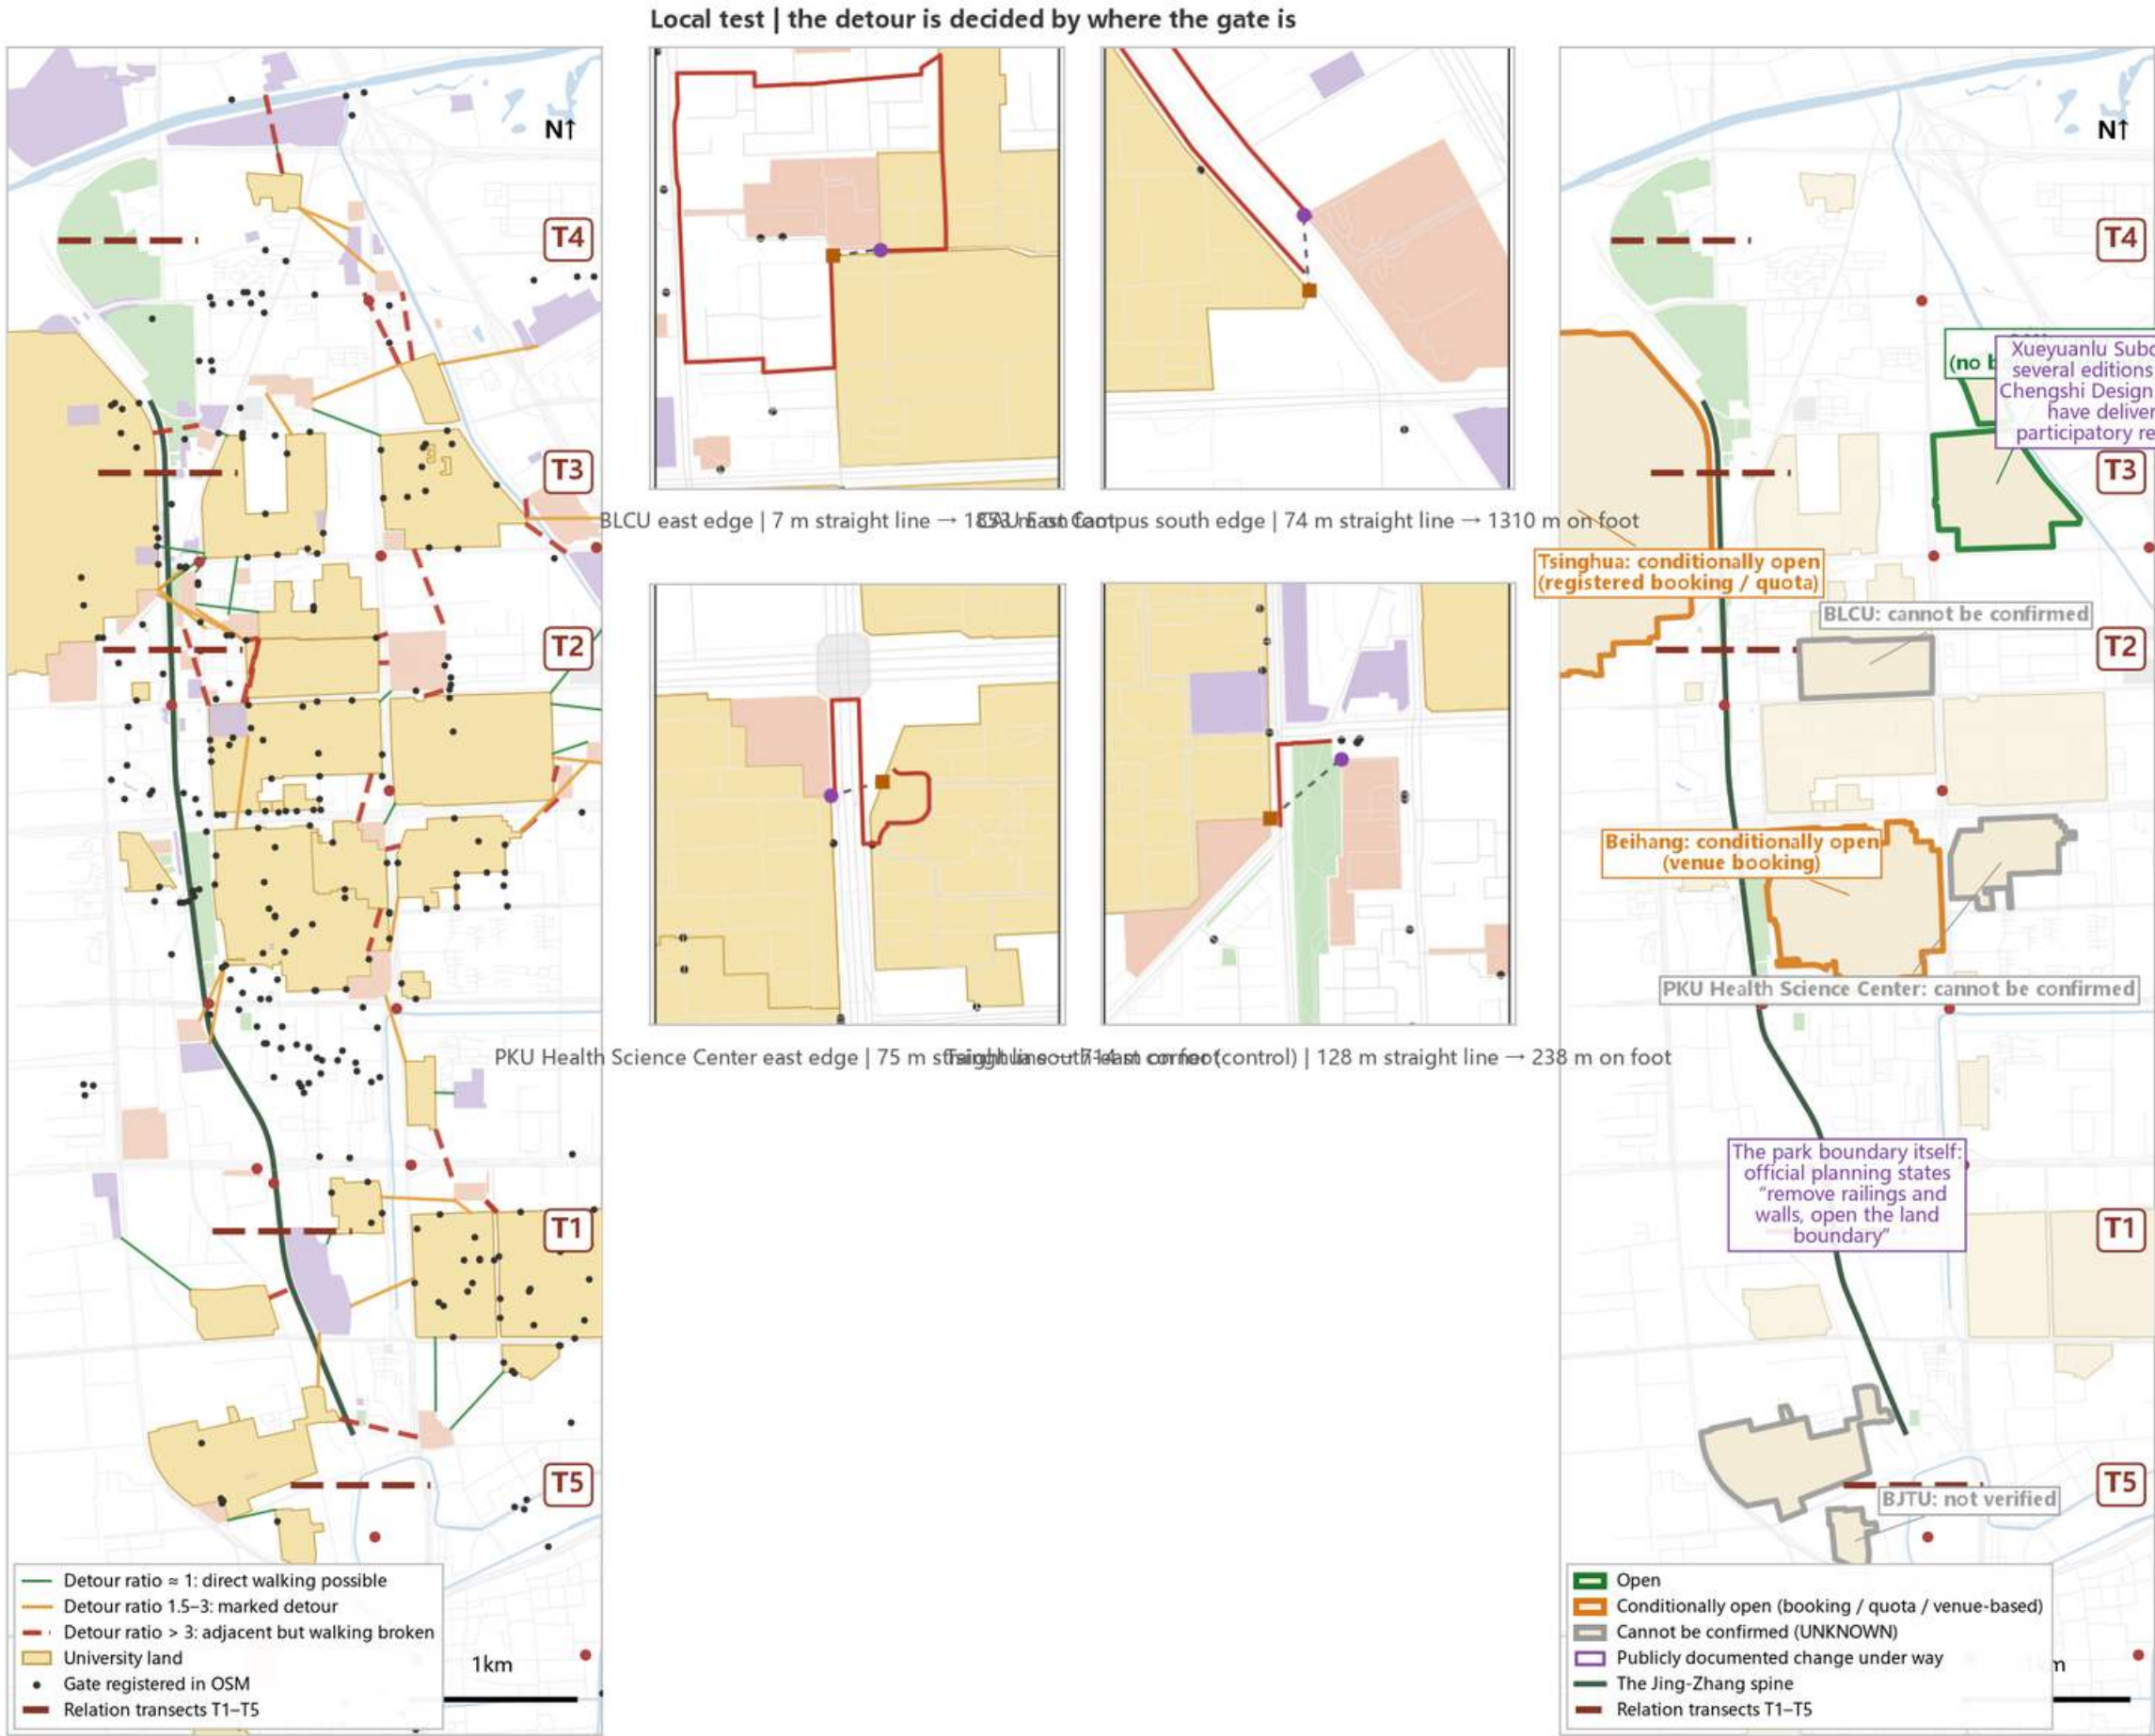


Spatial proximity,
physical access
and institutional openness
are not the same thing.

The universities along the line sit
close to Jing-Zhang, yet public exchange
still depends on where the gates are,
on opening rules and on management edges.

Different campus interfaces therefore
need differentiated approaches to
opening and control.

01 Physical connection | can you get there

02 Opening conditions | are you allowed in

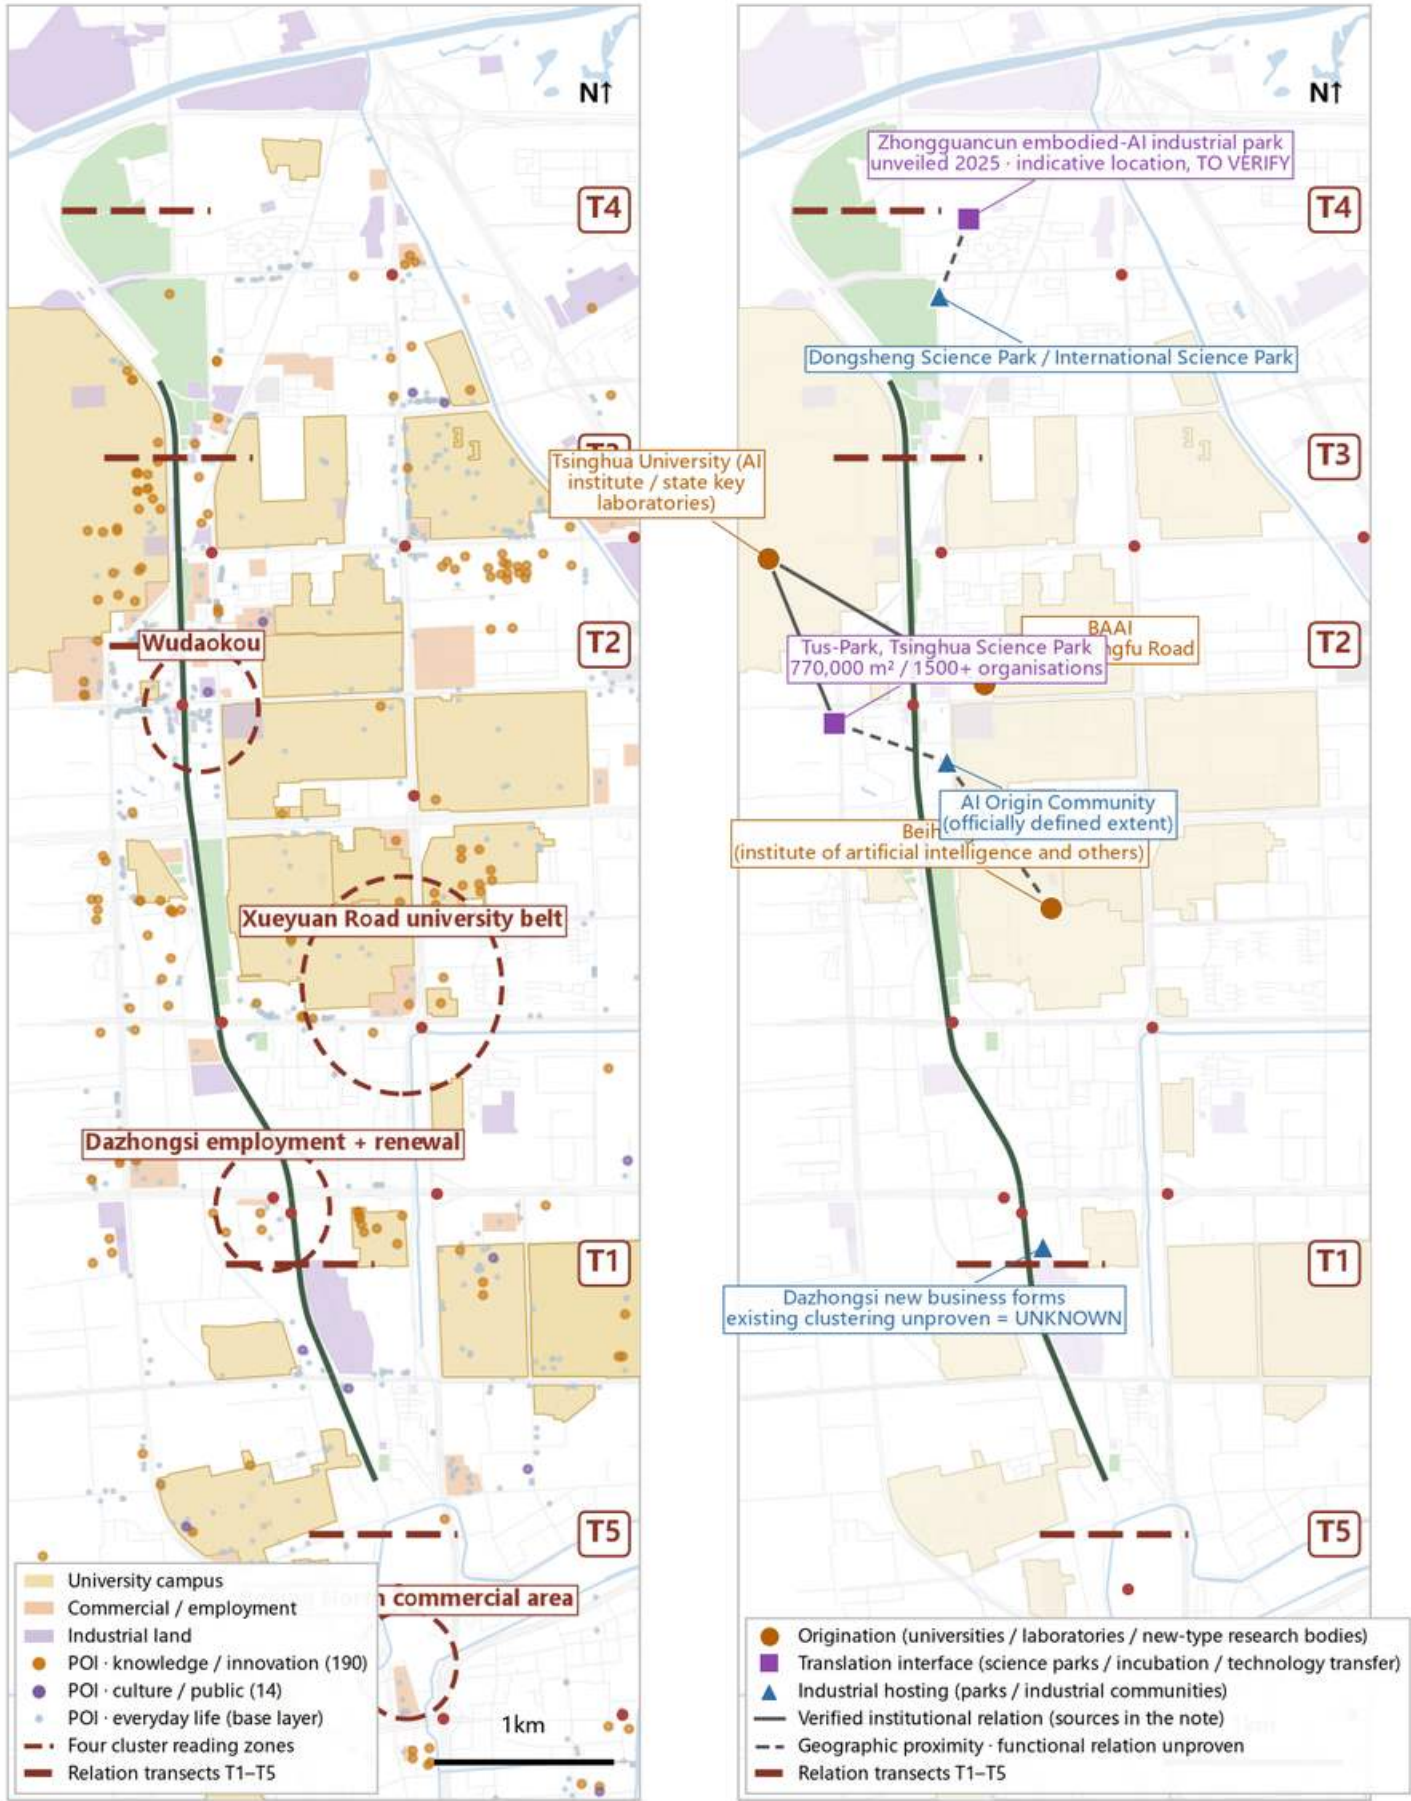


Resources have clustered; the exchange interface is weak

① Clustering: knowledge and innovation POIs form continuous bands along Xueyuan Road and around Wudaokou; universities, industrial land and three of the four clusters touch the corridor. ② Institution-level evidence: the verified origination-translation cluster lies around Chengfu Road-Wudaokou, immediately beside the corridor; at Tsinghua East Road the proximity is geographic and the interface unproven; existing clustering at Dazhongsi is unproven; Zhongzhiyuan = industrial hosting + new translation facilities. But the exchange interfaces and everyday connections between these institutions and urban public space are uneven — public space is the most direct potential exchange interface among the three, and it is precisely this layer that is currently weakest. **The resources have clustered densely, but the public exchange interface and everyday connections remain weak.**

Definitions: POI = registered distribution; verified institutional relations are drawn solid and geographic proximity - functional relation unproven. This does not assert that "the innovation chain has not formed".

① Clustering of innovation resources (as registered) ② Origination → translation → hosting (institutional evidence)

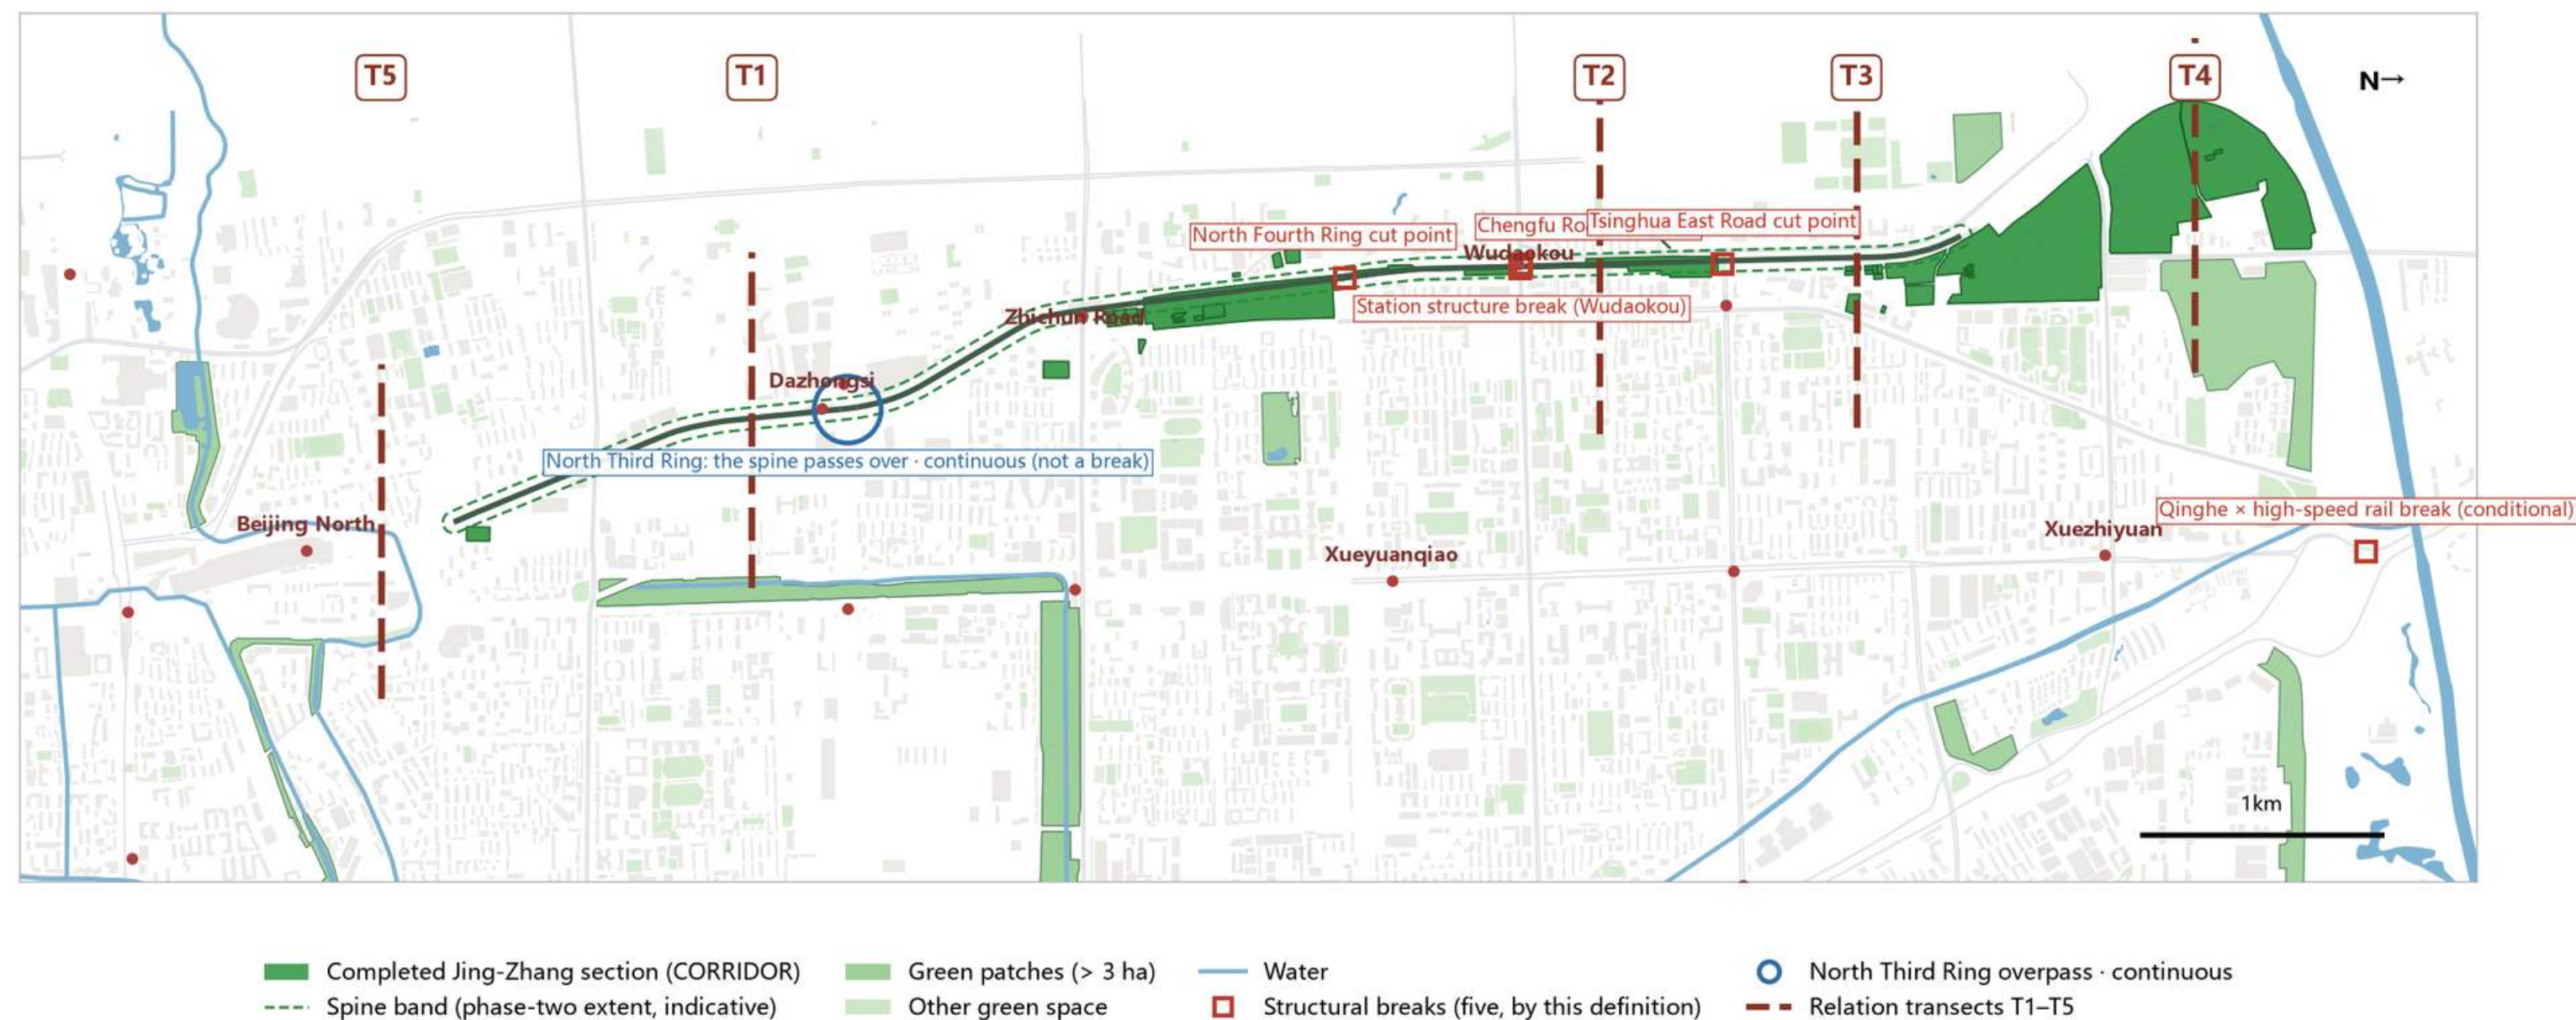


“Green on the map” does not mean “structurally connected” .

Jing-Zhang is one of the main continuous north-west to south-east green public-space spines within the study area. There are five structural breaks, four of them caused by grey infrastructure; at the North Third Ring the spine passes over and the green corridor stays continuous. Evidence on the functional performance of the green space is missing along the line, so no judgement of “insufficient function” is made. The next page tests ecological continuity against whether residents can actually get in.

The point of renewing green infrastructure is not to add more green, but to turn the ecological spine into public space that can be entered, reached and used.



① Ecological / physical continuity

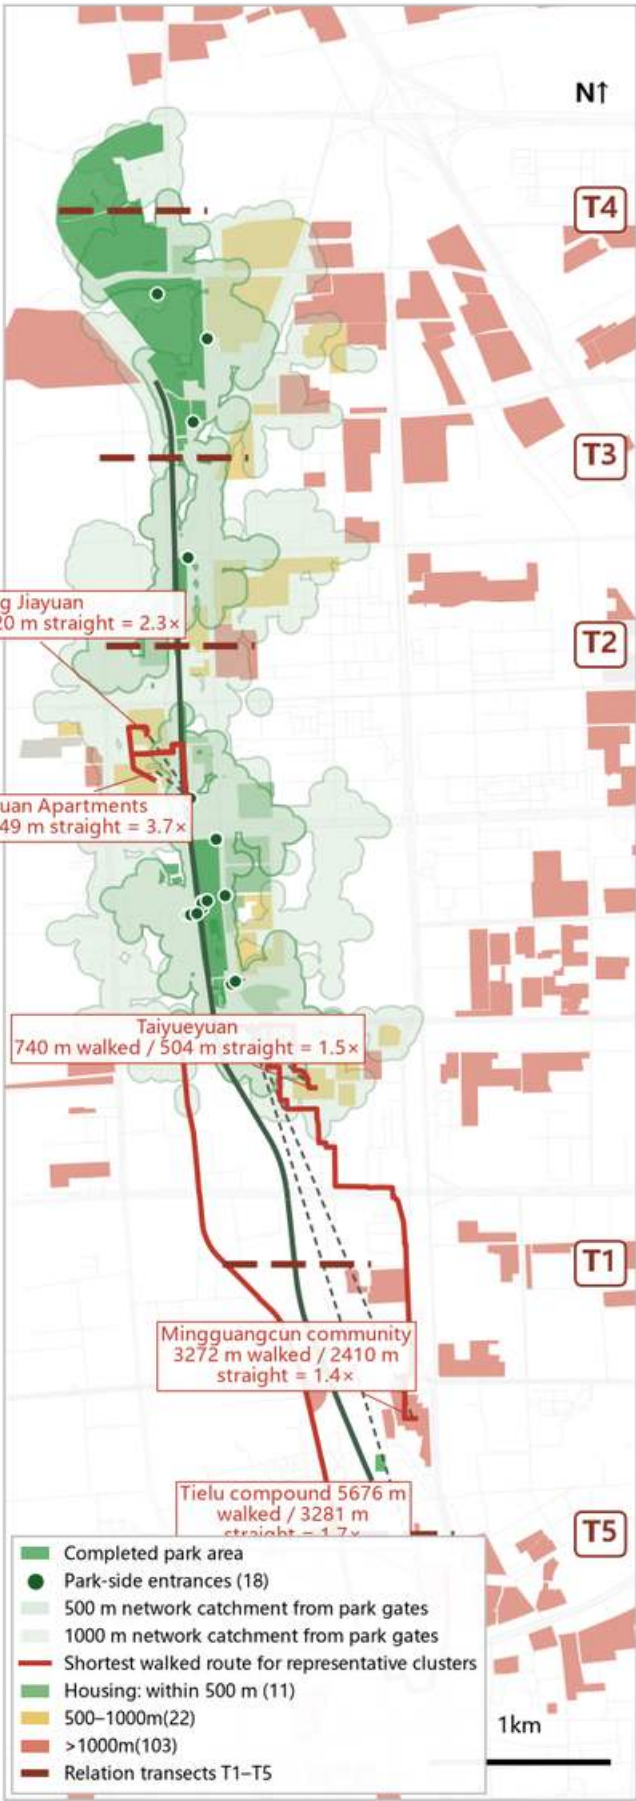

② Real access from housing to Jing-Zhang public space



Nodes near housing → any registered park entrance (green ≤ 400 m / amber ≤ 1200 m / red > 1200 m)

Ecological continuity ≠ being able to enter

Left: the northern section has ample, adjacent green space and the blue line is continuous — the ecological base is not the main problem. Centre: network catchments from the park-side entrances show the 500 m rings whole on both sides of the completed section, while whole blocks of housing across the tracks and beside the expressway fall outside 1000 m. The walked-to-straight-line ratios

reveal “close but hard to reach”.
Ecological continuity does not mean continuity of public use.

Definitions: entrances = park entrances registered in OSM (within 30 m of park_system); distance = shortest path on the whole walking network; the phase-two section is missing; functional evidence is not assessed. The secondary test uses a different definition (housing node → any park entrance) and does not replace the primary evidence.



① GRAY × SOCIAL interaction problem ② SOCIAL (× GREEN) interaction problem ③ GRAY × GREEN interaction problem --- Multi-system overlap location — The Jing-Zhang spine --- Relation transects T1–T5

Problem key (numbered on the drawing)

- ① Broken arrival chain in the station area [GRAY × SOCIAL] Dazhongsi / Beijing North ② Built adjacency without connection [SOCIAL, GRAY-caused] employment belt / Mingguangcun / west of T2 ③ Boundary proximity, touching but not passable [SOCIAL × GREEN] the T3 university belt ④ Insufficient public layering at crossings [GRAY] transverse, corridor-wide ⑤ Structural break in the green network [GRAY × GREEN] station structure / cut points / north end ⑥ Negative engineering interface along the spine [GRAY × GREEN] in segments along the line

The three infrastructure gaps overlap in different combinations, producing a different urban relation problem at each of T1–T5.




Transect	The real problem	Relation focus
T1 Dazhongsi	The station, the renewal parcels and Jing-Zhang are already closely adjacent, but arrival, level change and transverse	ARRIVE relation FACE not yet for CROSS hole
T2 Chengfu Road-Wudaokou	Universities, innovation resources and public space are adjacent, but the interface and the organisation of use have	FACE tled into USE le exchange
T3 Tsinghua East-Xueyuan Road	Opening conditions differ markedly along the campus edges; public exchange depends on management boundaries	FACE crossing CROSS ns
T4 Zhongzhiyuan	Industry, green space and the everyday city each operate on their own, without a sustained public interface between	FACE USE
T5 Beijing North	The yard and rail facilities divide east from west, and the Jing-Zhang terminus is not yet a gateway node that links th	ARRIVE both CROSS d organises arrival

STEP 0 | PROPOSITION

With a continuous public space now largely in place, the design focus shifts to reorganising the relations between the urban systems along the line and Jing-Zhang — first answering “which relation to change”, then “whether and how to intervene” .


STEP 1 | RELATION MECHANISM — which relation are we changing?

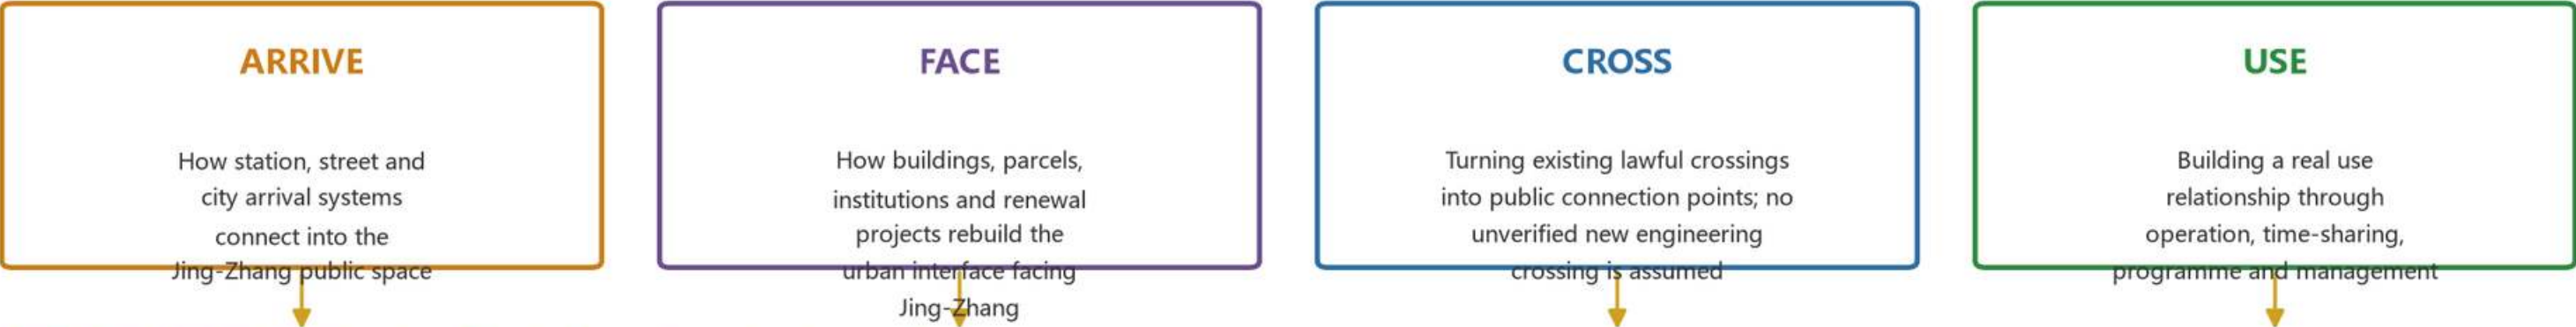

GATE | NO-DESIGN CHECK — does this relation really need an intervention?

First establish which kind of relation is at stake, then judge whether a spatial intervention is really needed. Four outcomes: NO DESIGN REQUIRED | NO DESIGN | TO VERIFY | UNKNOWN. Only relations that genuinely need intervention go on to STEP 2. “No number” does not mean “no problem” — it may mean no intervention is needed, conditions are undecided, or evidence is insufficient.

STEP 2 | INTERVENTION TYPE — by what means? (one primary type per problem)

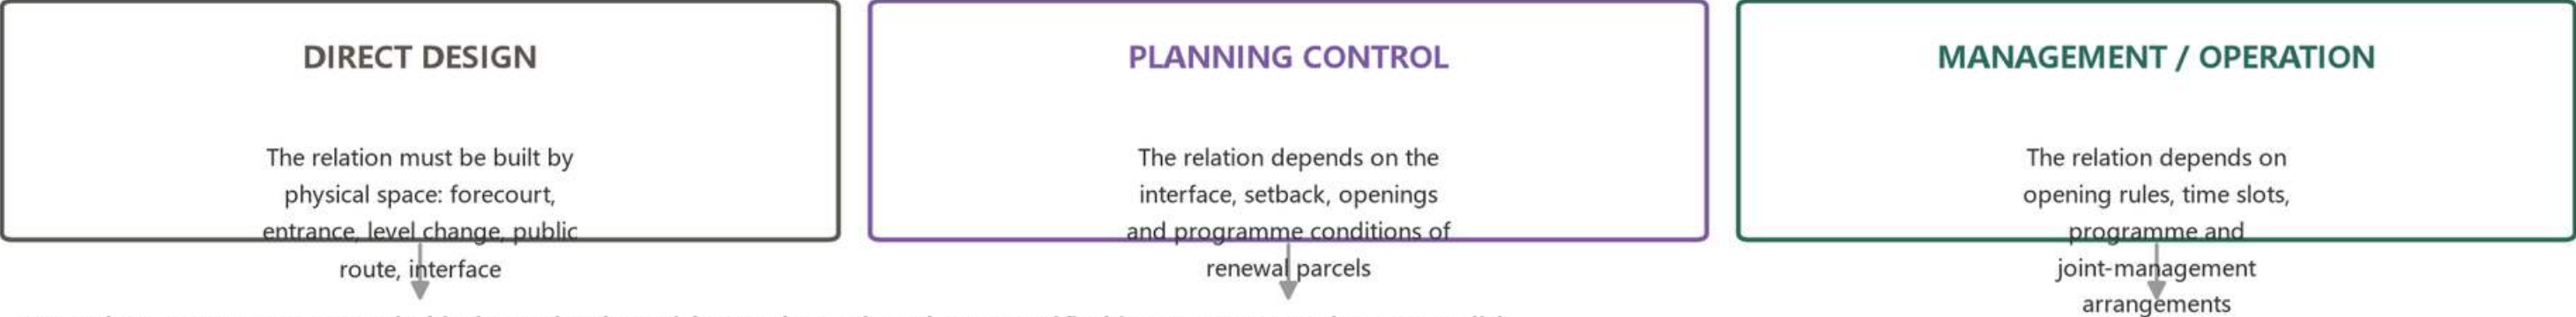

STEP 3 | Two status sets recorded independently (neither replaces the other; unverified items are never drawn as solid)

IMPLEMENTATION STATUS

NOW / ACTIONABLE

CONDITIONAL

FUTURE-RESERVE

EVIDENCE STATUS

VERIFIED

TO VERIFY


UNKNOWN

Decision rule: which relation to change → whether to intervene → how to intervene → implementation and evidence status. Applied to T1–T5 on the next page.

GRAY / SOCIAL / GREEN diagnosis → FP problem types (classification labels, not spatial units) → combined in space into T1–T5 (five relation transects)
→ relation mechanism → renewal mode / intervention type → planning action

Transect (spatial unit) + FP label		Renewal mode (secondary index)	RELATION MECHANISM		Intervention type → planning action implementation / evidence status			
T1	Dazhongsi	G-R01 interface reconstruction	ARRIVE	FACE	CROSS	DIRECT	Extend the entrance-to-spine arrival sequence; organise public use in the North Third Ring bridge zone	NOW-VERIFIED
		G-R03 plug-in attachment				CONTROL	Controlled reconstruction of the renewal parcel / Lanjing interface; controlled openings at Mingguangcun with services	CONDITIONAL-VERIFIED
		G-R05 time-shared substitution				MGMT	Time-slot and programme organisation of arrival in the 1733 forecourt	NOW · use TO VERIFY
		FP1 FP2 FP4						
T2	Chengfu Road–Wudaokou	S-R02 public space activation	FACE	USE		MGMT	Activation of the start-up area · time-shared use	NOW · use TO VERIFY
		G-R07 coordinated coupling (station rebuild)				DIRECT	Fill the western access gap (small scale, operation first)	NOW-VERIFIED 2.3–3.7×
		G-R01 interface reconstruction				CONTROL	Write the interface conditions of the Wudaokou station rebuild into the works	CONDITIONAL-VERIFIED
		FP2 FP6						
T3	Tsinghua East–Xueyuan Road	G-R01 interface reconstruction (campus)	FACE	CROSS		CONTROL	Conditional controlled exchange openings (agreed with the institutions)	CONDITIONAL-VERIFIED 13%
						NO DESIGN	Default is to keep existing conditions: no fence removal, no forced opening	—
						DIRECT	Strengthen the public character of existing crossings (at verified locations)	NOW-VERIFIED
		FP3						
T4	Zhongzhiyuan	GR-R02 green-structure renewal	FACE	USE		CONTROL	North end–Qinghe conditional green-network interface (reserved only if a lawful crossing condition holds)	CONDITIONAL · conditions TO VERIFY
		GAP① green-network structural connection				MGMT	A sustained public interface across industry, green space and everyday space	NOW-MEDIUM
						NO DESIGN	If the crossing condition does not hold → keep existing conditions (a legitimate outcome)	
		FP5 FP3						
T5	Beijing North	G-R03 plug-in attachment	ARRIVE	CROSS		DIRECT	Station-front gateway arrival organisation (small scale)	NOW-VERIFIED 0.16
		G-R01 interface reconstruction				DIRECT	Organise east–west connection through the station area (no new engineering crossing)	NOW-VERIFIED
		GAP② conversion of spatial resources				CONTROL	Reserve the Line 13A interface; conditional conversion of the shed land east of the railway	CONDITIONAL-VERIFIED
		FP1 FP4						

GAP① green-network structural connection and GAP② conversion of spatial resources do not belong to the four mechanisms; they are listed separately and do not constitute a fifth mechanism (in T4 they take the form of a CONDITIONAL GREEN-NETWORK INTERFACE). FP1 broken arrival chain in the station area / FP2 built adjacency without connection / FP3 touching but not passable / FP4 insufficient public layering at crossings / FP5 structural break in the green network / FP6 negative engineering interface.

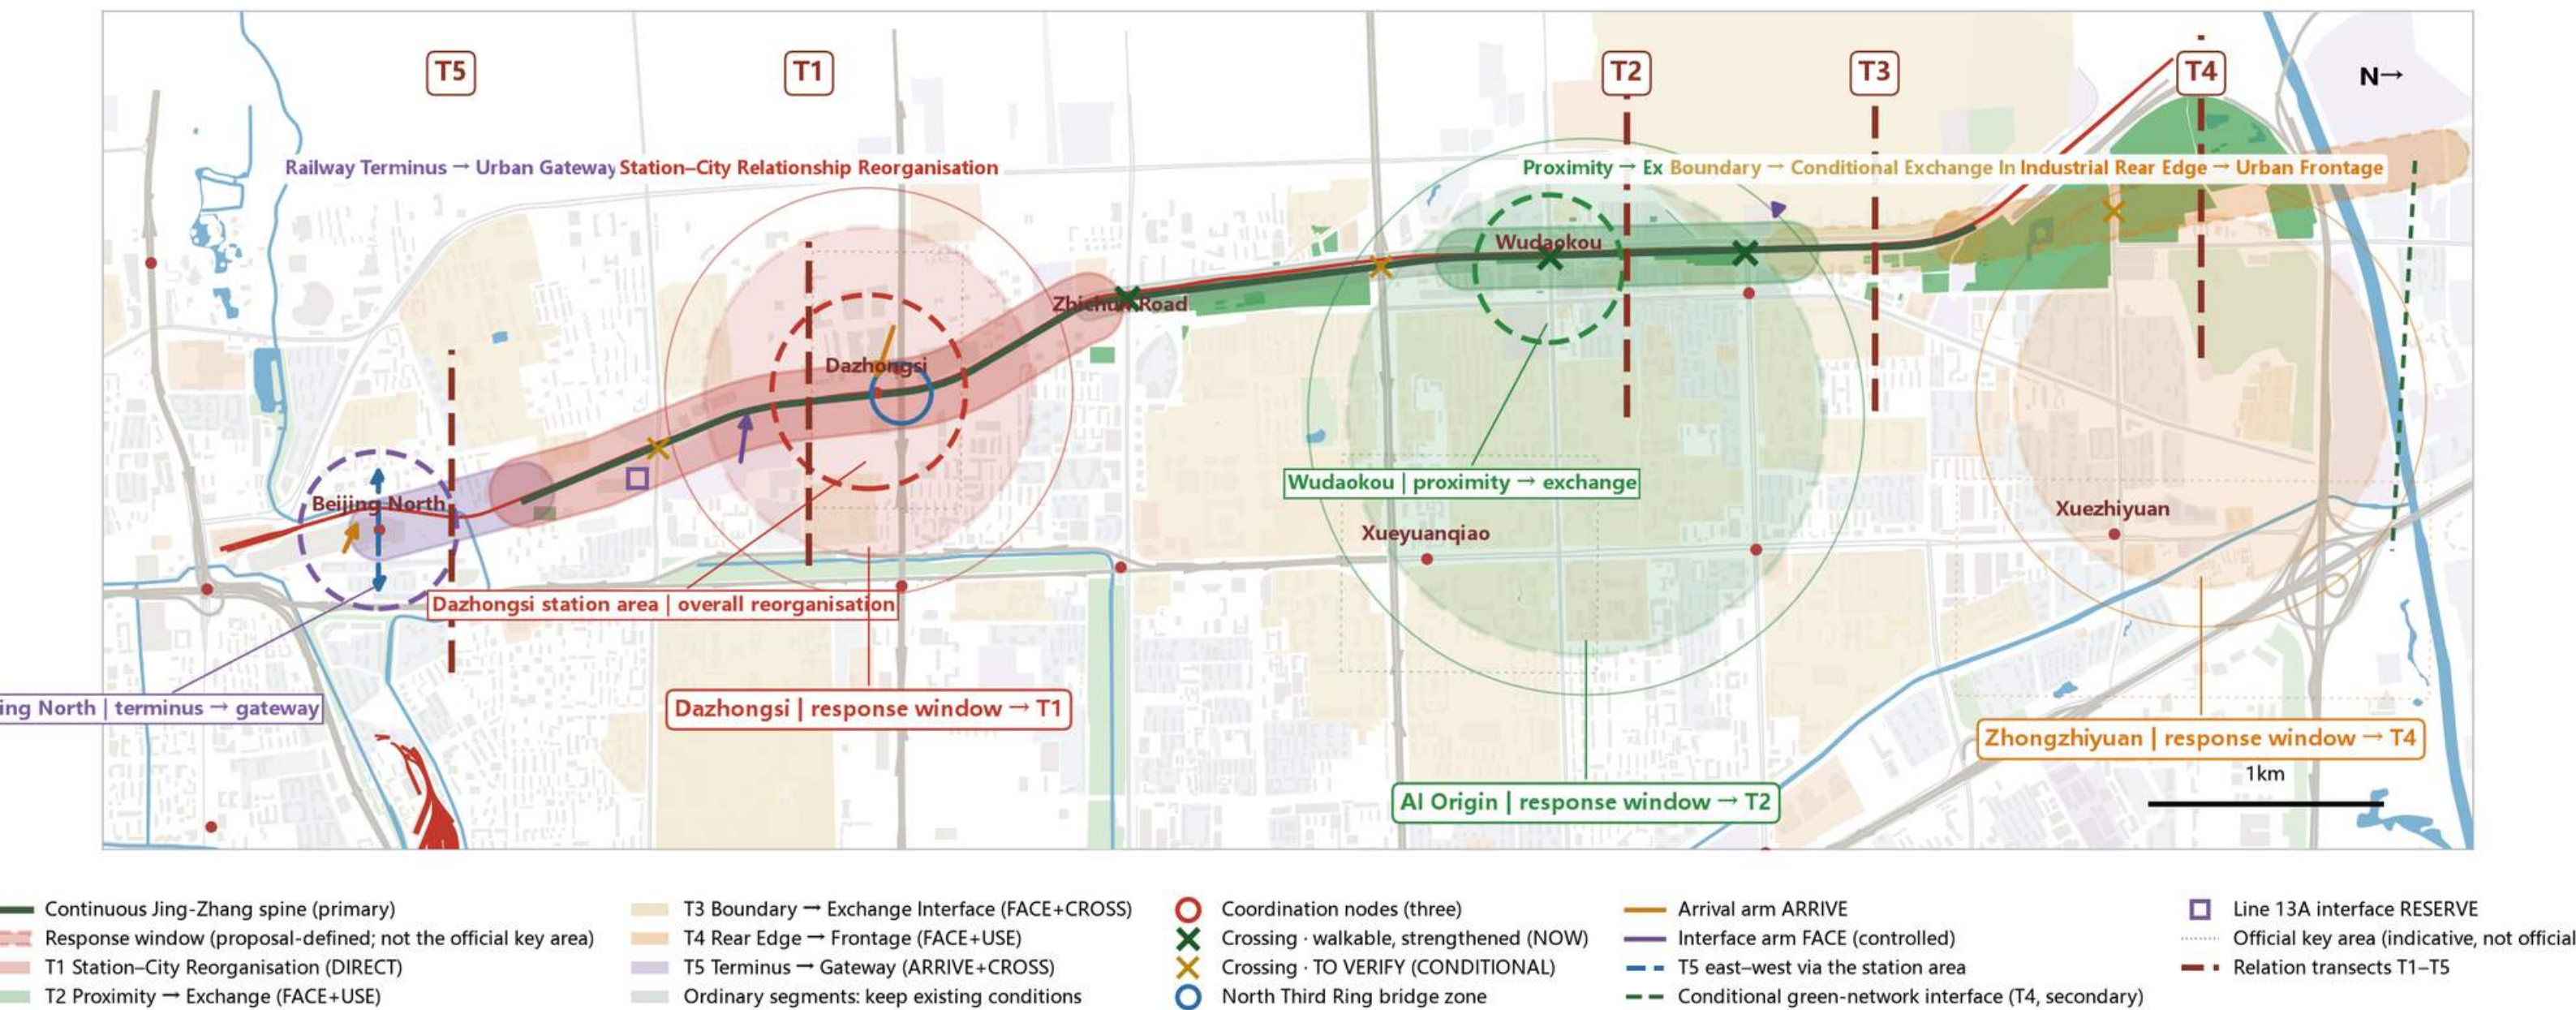

One continuous spine × five urban relation transects × design response windows for three key areas

T1 Station-City Relationship Reorganisation | T2 Proximity → Exchange | T3 Boundary → Conditional Exchange Interface | T4 Industrial Rear Edge → Urban Frontage (the conditional green-network interface is a secondary annotation only) | T5 Railway Terminus → Urban Gateway. Keeping existing conditions along the ordinary segments is also a planning decision. The three response windows are key design locations identified by this proposal; they are not equivalent to the official key-area boundaries.



Chengfu Road-Wudaokou | FACE + USE

EXISTING URBAN RELATIONS



Present reading

Resources, movement and existing crossings are all close at hand, yet the public space is still mainly for passing through, and lingering and exchange are cut into fragments.

Relation shift

Eligible Community for public exchange through existing crossings and into universities. Through exchange for

Future | Community exchange — crossing arrival — managed innovation exchange

Future strategy


Through exchange for courtyards, open ground floors and managed exchange interfaces, the existing crossings turn from traffic nodes into a continuous chain of public exchange.

FUTURE RELATION SCENARIO



Tsinghua East-Xueyuan Road | FACE + CROSS

EXISTING URBAN RELATIONS

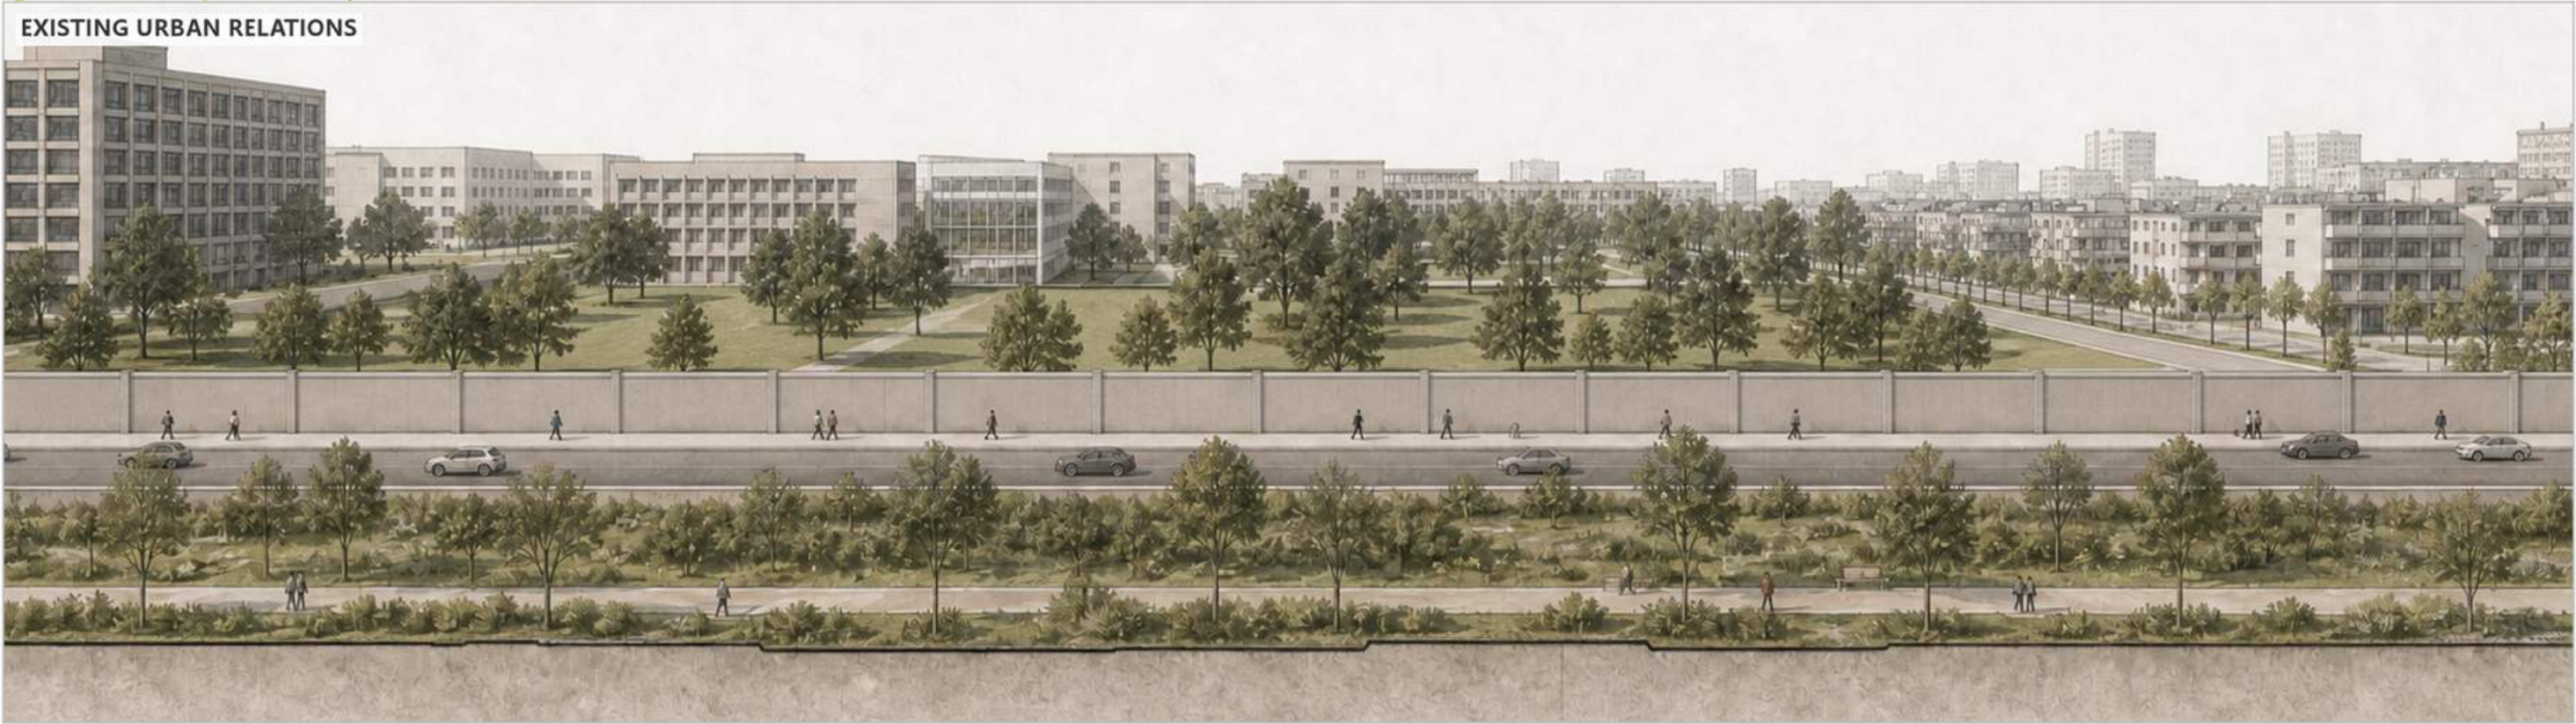

Present reading

Universities and research institutes sit next to Jing-Zhang, but a continuous management edge has kept the transverse relation at the level of mere spatial adjacency.

Relation shift


Now, Campus — hard boundary — city road — Jing-Zhang

Future | Campus — layered / controlled exchange interface — city road — Jing-Zhang

Future strategy

The single hard boundary becomes a graded interface: closed but public-facing — semi-open exchange. Conditional controlled opening designed and do not correspond to any verified existing campus gate.

FUTURE RELATION SCENARIO

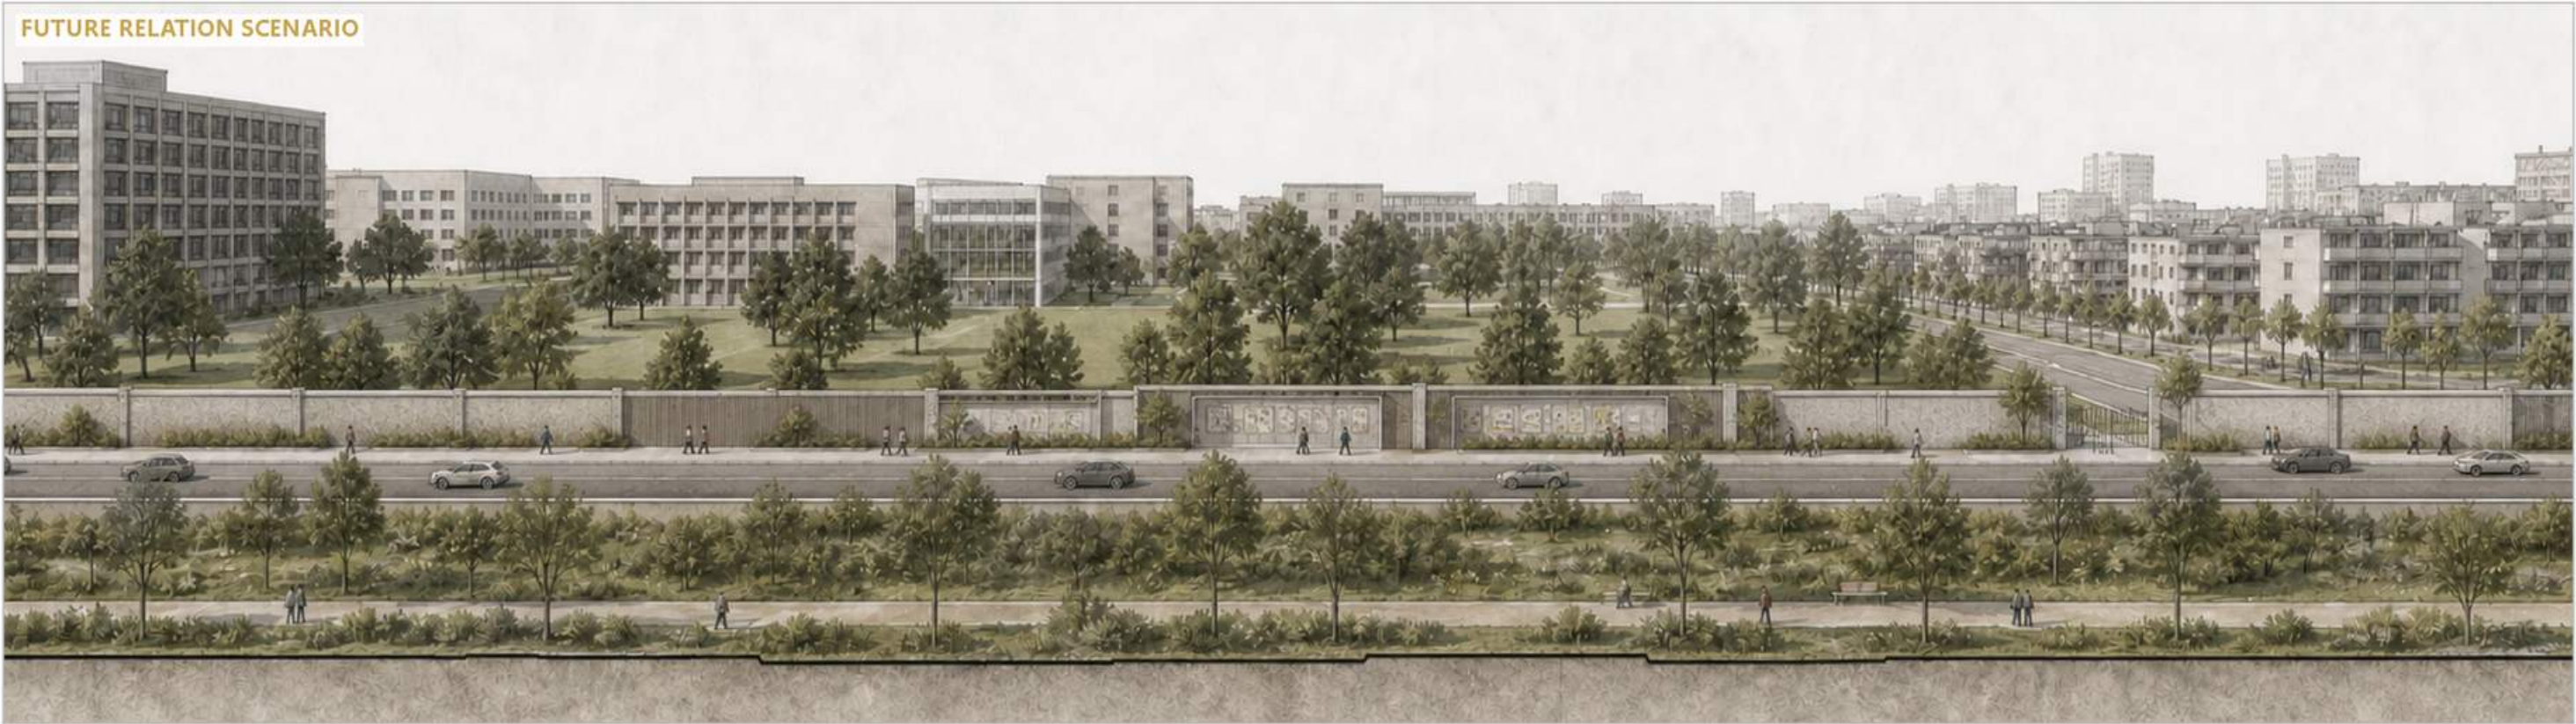

Zhongzhiyuan | FACE + USE

EXISTING URBAN RELATIONS



Present reading

Industry, green space and Jing-Zhang are adjacent, but the side facing the city is still mostly production backyard and space for passing through.

Relation shift

Mostly industry-backed space facing Jing-Zhang.

Future | Industry — public interface — everyday green space — Jing-Zhang — city life

Future strategy


Industrial operation continues; through public ground floors, semi-outdoor exchange, public forecourts and everyday green space, the secondary, conditional annotation only; the primary T4 mechanisms are FACE + USE. Industrial rear edge becomes a public frontage facing Jing-Zhang and city life.

FUTURE RELATION SCENARIO



Beijing North | ARRIVE + CROSS

EXISTING URBAN RELATIONS

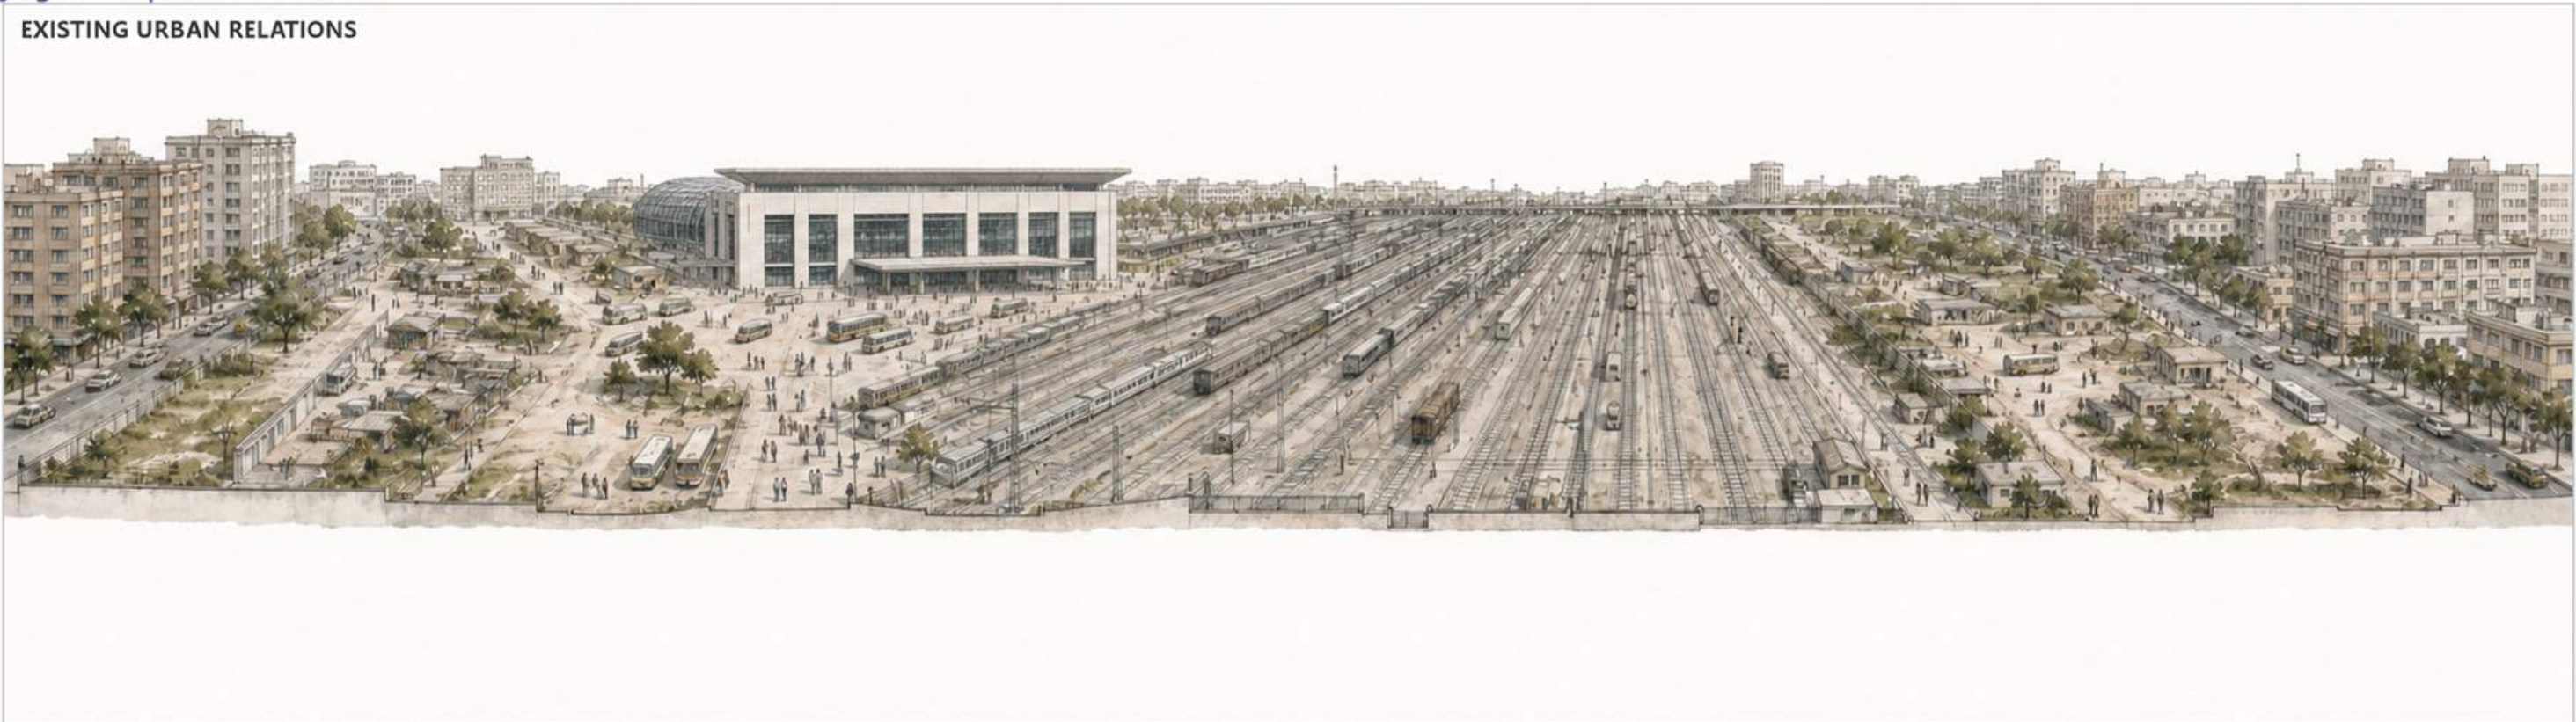

Present reading

The large rail yard reinforces the separation of the two sides; city arrival and the southern end of Jing-Zhang have yet to form a shared gateway identity and organisation.

Relation shift

New | City — primary arrival — Beijing North / Jing-Zhang terminus — rail yard — secondary interface — city

Future | City — primary arrival — Beijing North / Jing-Zhang terminus — rail yard — secondary interface — city

Future strategy

With the existing Beijing North station area as the orientation core, a primary arrival, an integrated architecture landscape gateway and crossing works are proposed. A secondary interface bring the city on both sides to face the southern end of Jing-Zhang together.

FUTURE RELATION SCENARIO






Dazhongsi Cluster | indicative location Beijing AI Origin Community (provisional) Zhongzhiyuan Acceleration Area (provisional) the Jing-Zhang public space spine Relation transects T1-T5

Official key area (task object)	Published area	Official task role	Response window in this proposal
Dazhongsi AI Industry Cluster	about 72.0 ha	AI-native new business forms	T1 Dazhongsi
Beijing AI Origin Community	about 104.3 ha	World-class AI innovation ecosystem	T2 (T3 as adjacent-boundary context)
Zhongzhiyuan AI Autonomous Innovation Acceleration Area	about 192.1 ha	Full-stack autonomous AI innovation system + global voice	T4 AI governance


Dazhongsi AI Industry Cluster

about 72.0 ha | AI-native new business forms

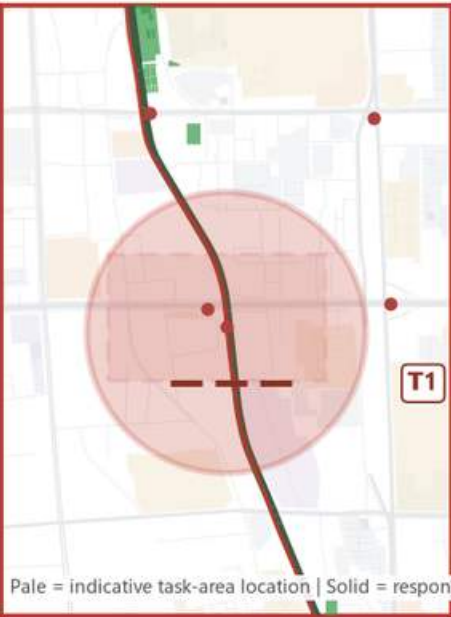

Beijing AI Origin Community

about 104.3 ha | world-class AI innovation ecosystem

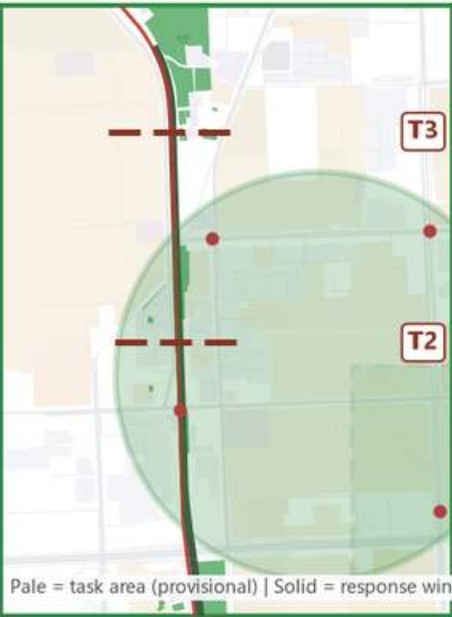

Zhongzhiyuan AI Autonomous Innovation Acceleration Area

about 192.1 ha | full-stack autonomous innovation system



Response window T1 Dazhongsi ARRIVE FACE CROSS

Relation problem

The station, the renewal parcels and Jing-Zhang are closely adjacent, but arrival, level change and transverse public relations do not yet form a whole.

Overall approach

01 Arrival reorganisation

A continuous arrival sequence: city approach → 1733 forecourt → entrances A/B → station structure

02 Public hinge in the station

Ground-level arrival → public vertical transfer within the station → upper-level public transfer, with no change to the rail works

03 Releasing relations on both sides

Released towards the Jing-Zhang spine, the N2 / eastern public space and the renewal interfaces on both sides

Design depth OBJECT-LEVEL DESIGN

Area-wide strategy | source

Official brief + public sources + the urban relation analysis already carried out in this proposal

Response window T2 (adjacency context: the T3 can FACE edge) USE

Relation problem

At the interface where the AI Origin Community meets Jing-Zhang directly: universities, innovation resources and public space are closely adjacent, but the exchange interface and the organisation of use have not yet settled into a stable relation.

Overall strategy

01 Campus-adjacent innovation translation network

Origination-incubation-display-translation form a continuous innovation interface; no new enclosed campus is built

02 Station exchange nodes

Stations such as Wudaokou and Tsinghua East Road West organise arrival, crossing, lingering and resource exchange

03 Campus-edge gradient

Closed but public-facing / semi-open exchange / conditional controlled opening

04 Everyday-life base for talent

Housing, services, social life, learning and innovation together form a campus-adjacent innovation district

05 Low-disturbance incremental renewal

Design depth STRATEGIC FRAMEWORK + CONCEPTUAL SPATIAL CONTROL (T2/T3) first; large-scale demolition is not the default path

Response window | source

The urban relation analysis and design work of this proposal

Response window T4 FACE USE

Relation problem

At the interface where Zhongzhiyuan faces Jing-Zhang and the surrounding everyday city: industrial operation, green space and city life are adjacent to one another, but a sustained public interface is lacking.

Overall strategy

01 Full-stack AI industrial base

R&D and production keep running, while the origination-pilot-translation-display relation is strengthened

02 Public innovation interface

The industrial rear edge becomes a public ground floor, semi-outdoor exchange and public forecourt facing Jing-Zhang

03 Building-green space-water as one system

Green space works as infrastructure for innovation exchange and everyday use, not as added planting

04 Industry display and public exchange network


Industrial capability becomes visible and open to exchange with the city, rather than operating only inside an enclosed campus

05 External transport and green interfaces

External transport such as the Fifth Ring is a specialist task; only green-network interface is a local, conditional interface and is not raised to a primary T4 mechanism

Not yet possible

Exact parcel positioning, building scale, retain-renovate-demolish decisions, statutory land-use change, precise road or engineering schemes, and a complete set of regulatory-plan indicators

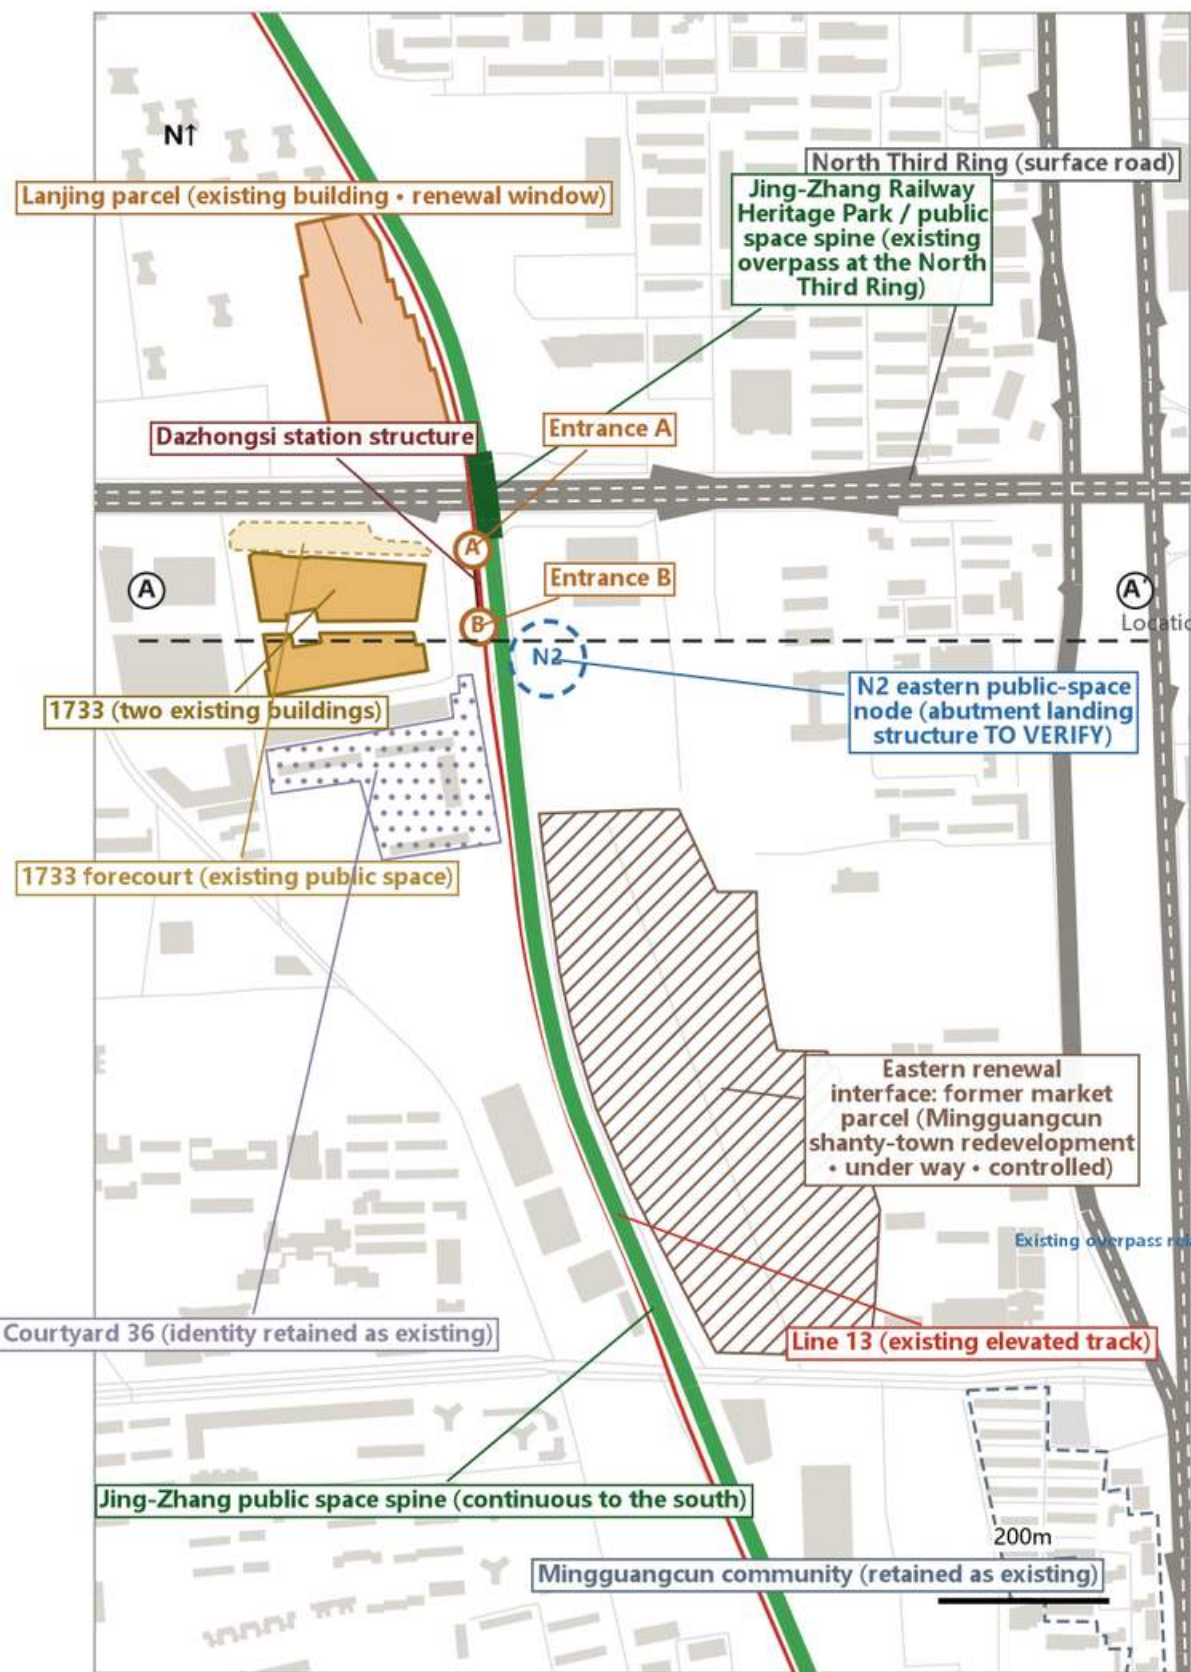

Location along the 9 km line | red frame = T1

VERIFIED FACT

Station structure and entrances A/B (verified positions); Line 13 = existing elevated track; the Jing-Zhang public space spine is continuous and passes over at the North Third Ring; the North Third Ring = surface road; the two existing 1733 buildings and the forecourt; the Lanjing parcel lies north of the North Third Ring; the former market parcel (eastern renewal interface), Courtyard 36 and Mingguangcun retain their existing identity. Exact relative levels of the two elevated systems; bridge clearances; internal levels of the station; stairs / lifts / escalators; the N2 abutment landing structure; specific building heights. The section at lower right shows indicative relative levels only.

DESIGN AUTHORITY

The station forecourt and arrival sequence can be designed directly. The 1733 / former market parcel / Lanjing interfaces are reconstructed under control as renewal proceeds. The station structure, track, bridge and North Third Ring are existing works and are not altered. The N3A gateway is held only as a conservative protective



Entrance / forecourt | Entrance A, Feb 2025 (CC BY-SA 4.0) Tight against the building base and railings, with no forecourt to guide arrival



Entrance / forecourt | Entrance B, Apr 2021 (CC BY-SA 4.0) The entrance abuts the road, with nothing organised towards the 1733 forecourt



Lanjing parcel | released by the Municipal Commission of Planning and Natural Resources, Jun 2026 The renewal interface is in a window of redefinition




Station structure and the interfaces on both sides (CC BY-SA 3.0) Stretched along the road, with the character of a transport facility

Site photographs | Wikimedia Commons CC BY-SA ×3 (RobertSchwandl / N509FZ / Siyuwj) Municipal Commission of Planning and Natural Resources, public release ×1


EXISTING RELATION SECTION A—A' (west → east, passing south of Entrance B; section line shown on the left)

Plan relations and the sequence of objects are verified; the vertical dimension shows indicative relative levels only — exact levels, clearances and structure await specialist verification (TO VERIFY)

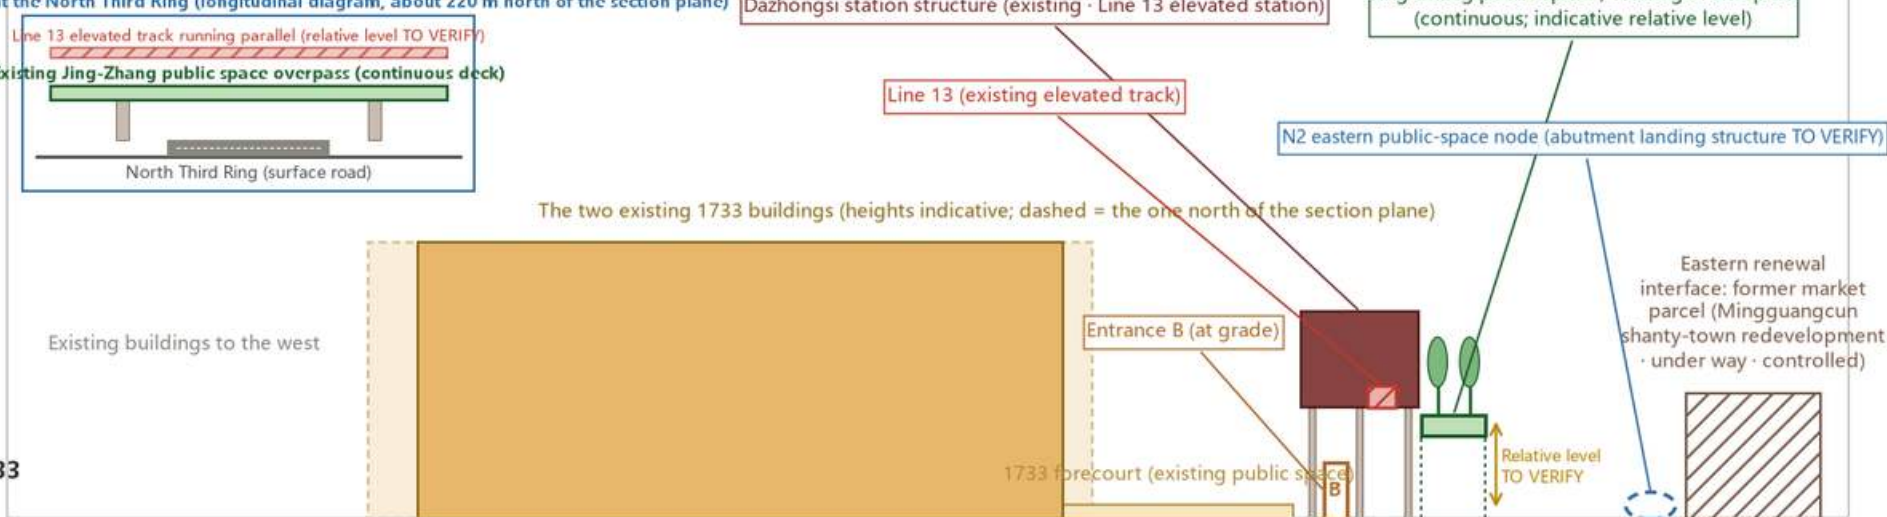

Horizontal positions are projected along A—A' from OSM geometry (in metres, no exaggeration); building heights and track / deck levels are indicative.

- the Jing-Zhang public space spine
- Existing overpass section (deck)
- Line 13 existing elevated track
- North Third Ring surface road
- The two existing 1733 buildings
- 1733 forecourt
- Dazhongsi station structure
- Entrances A / B (verified positions)
- Lanjing parcel (existing building)
- Eastern renewal interface: former market parcel (under way • controlled)
- N2 (structure TO VERIFY)
- Section line A—A' (section, lower right)

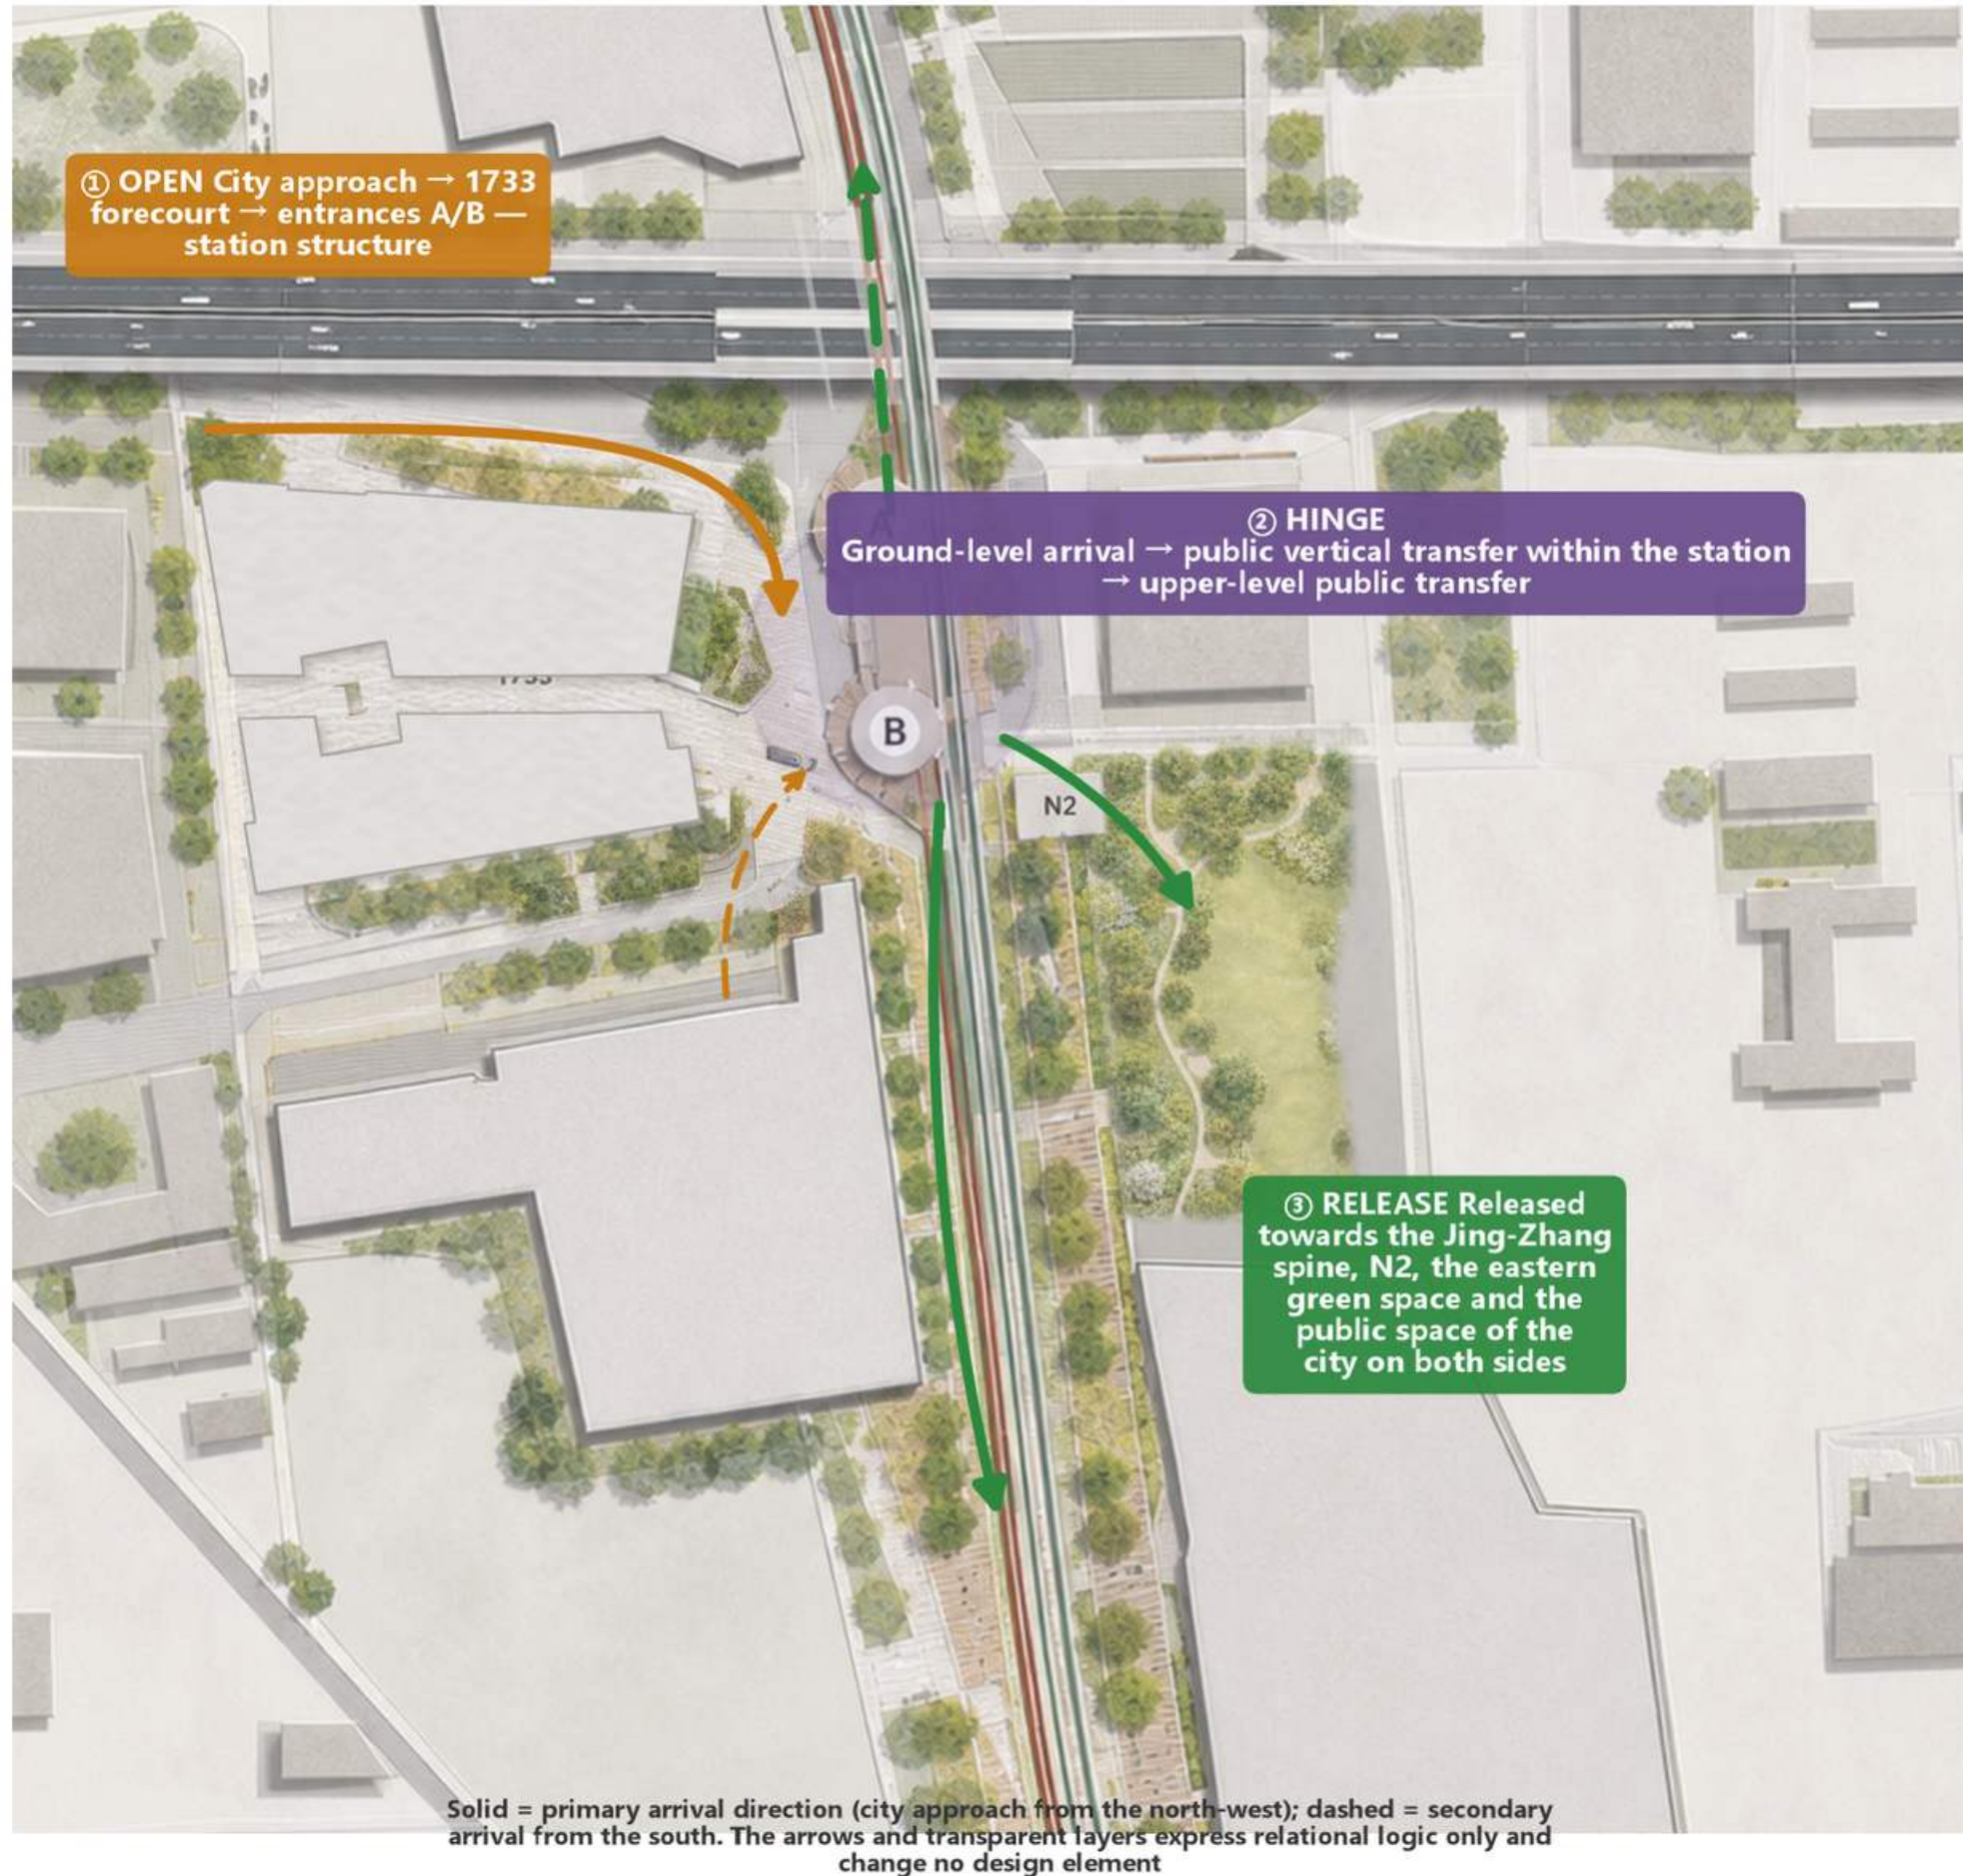

① OPEN

The object is the public space of the 1733 forecourt, not the buildings themselves. From the city side (mainly the streets to the north-west, secondarily from the south) → 1733 forecourt → entrances A/B → station structure, forming a clear ARRIVE

chain; open the forecourt and lead arriving movement to the station.

② HINGE


The ground-level arrival deck takes up the 1733 forecourt and entrances A/B; the station forms a two-level public transfer hinge; the upper public transfer level meets the Line 13 platform and the Jing-Zhang Railway Heritage Park deck, while linking 1733 to the west with the N2 public space to the east (exact levels and vertical circulation to be verified).

③ RELEASE

From the spatial hinge in the station area the relation is released further to the north-south Jing-Zhang spine, N2, the eastern green space and the public space of

Open on hinge - release: a broken arrival chain is organised into one continuous public space

Exact levels, vertical circulation inside the station and the abutment structure are to be verified; no new rail-crossing works are proposed.

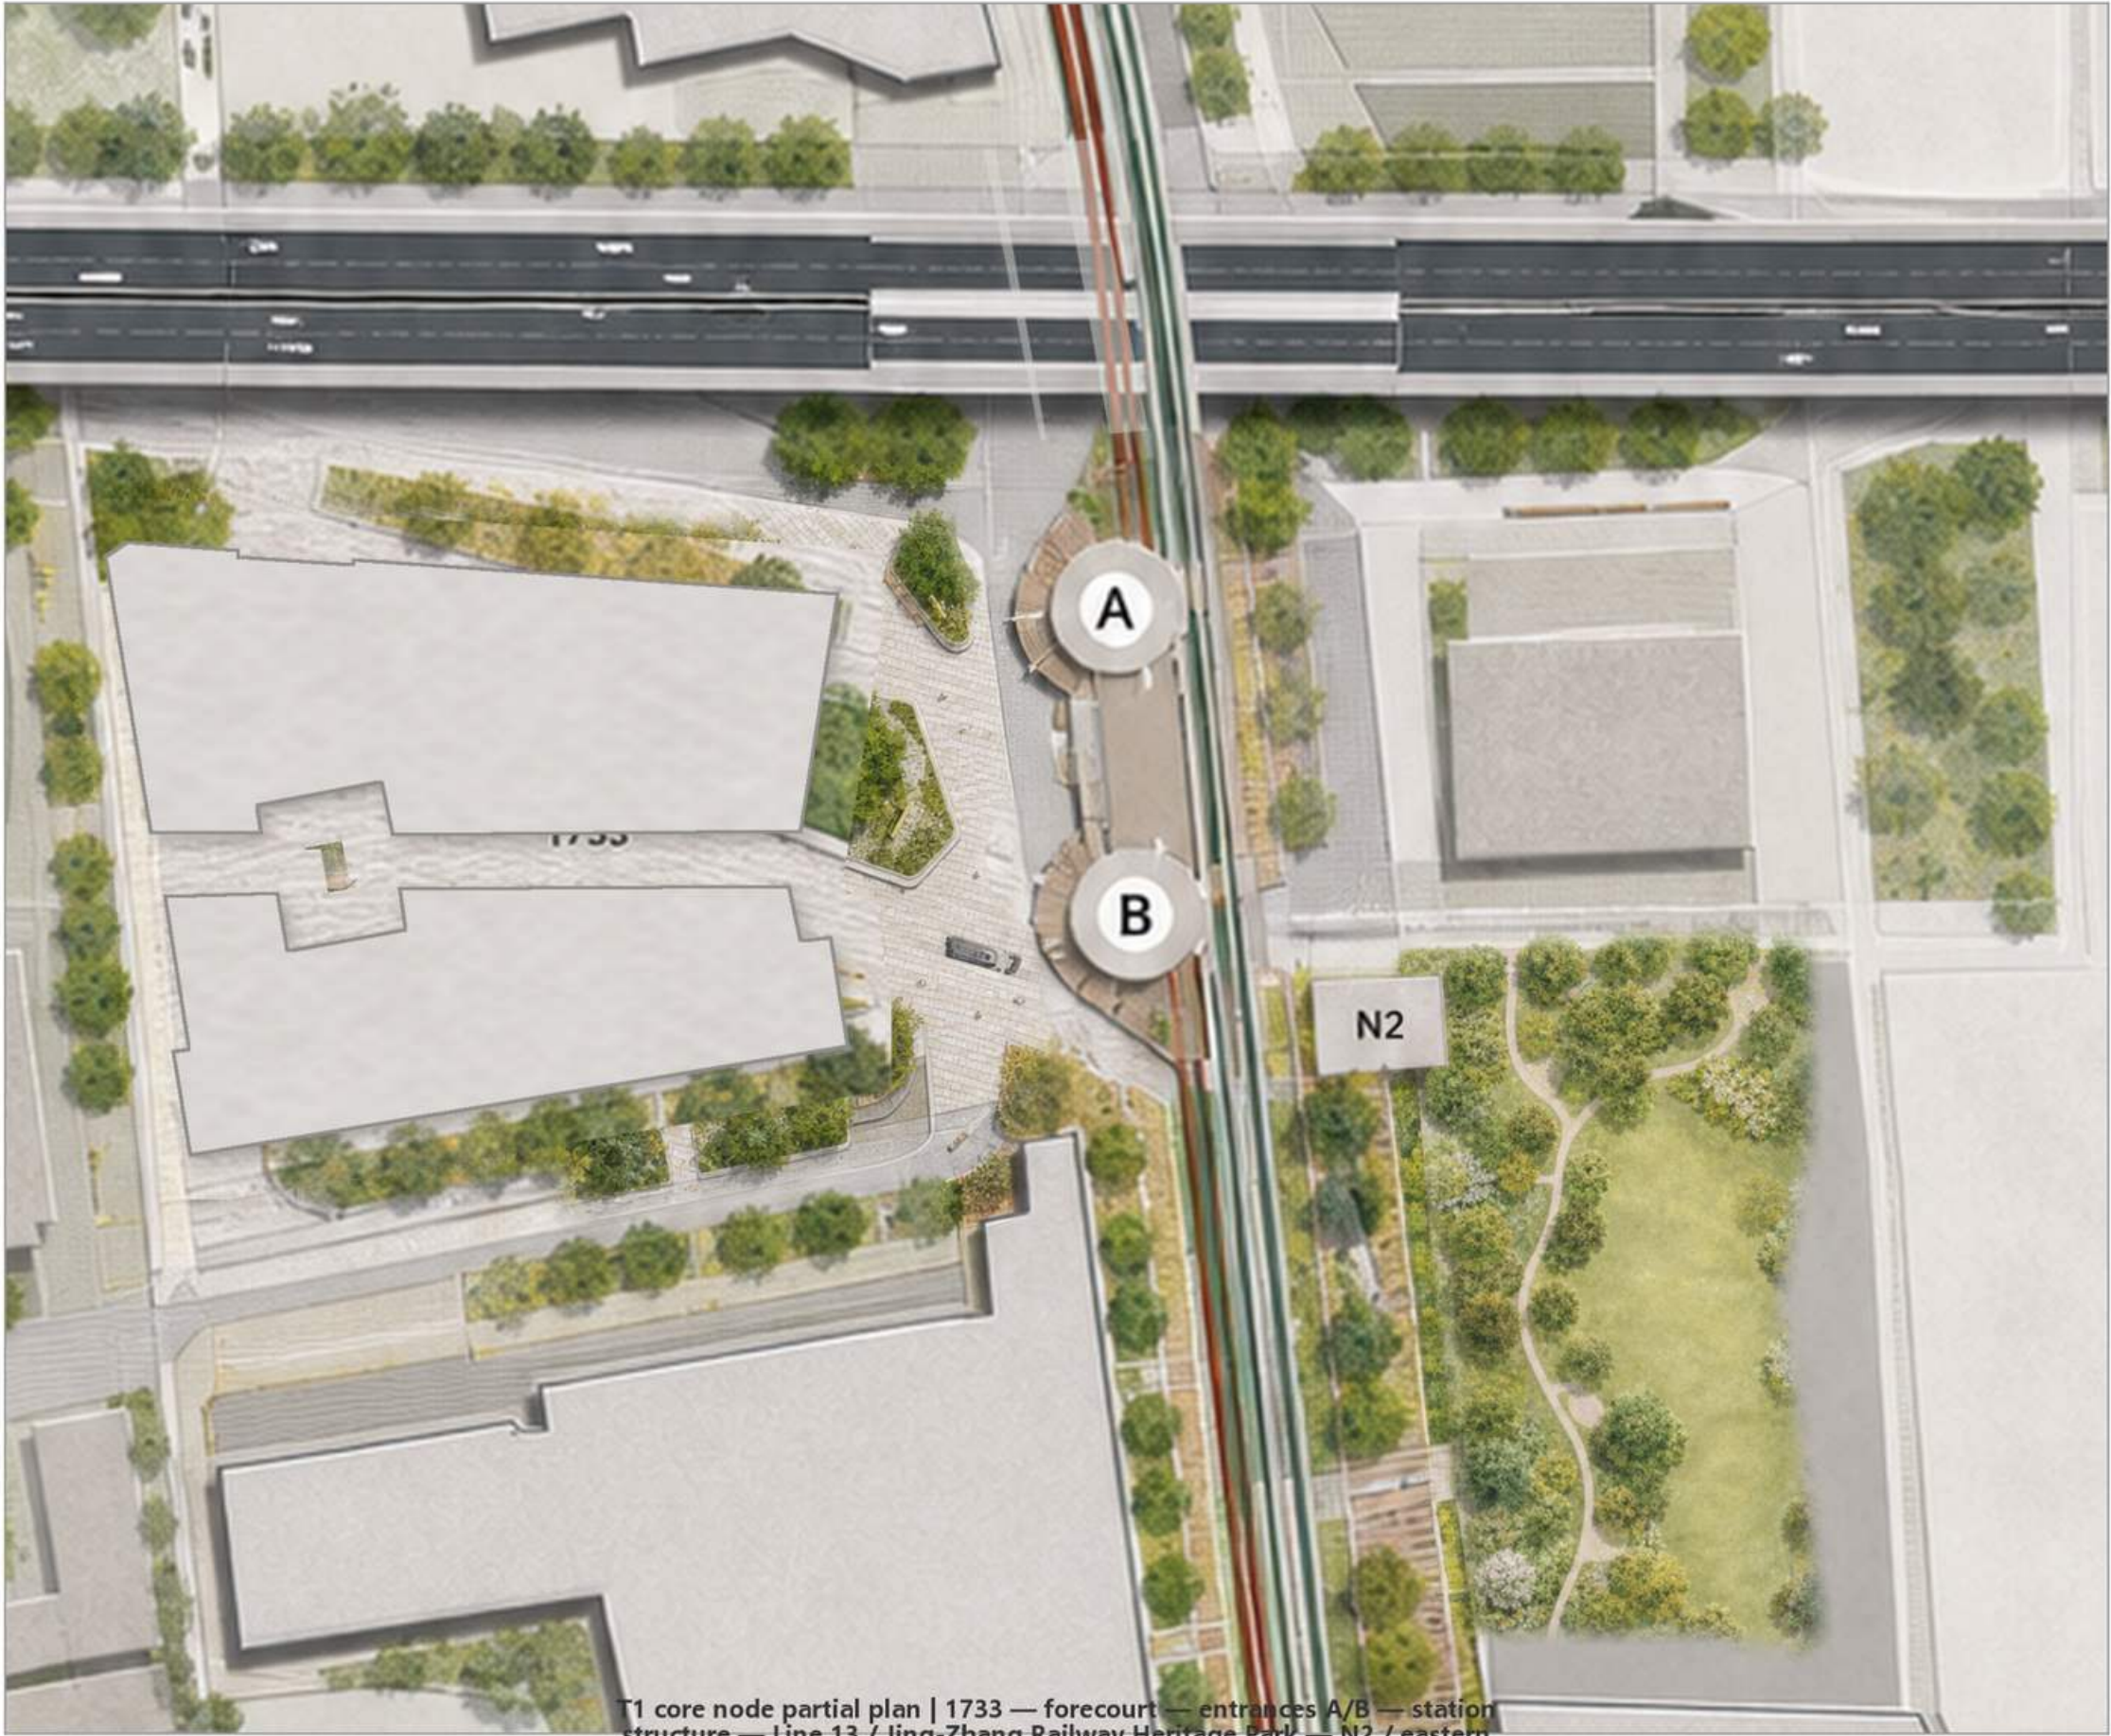

T1 core node partial plan | 1733 — forecourt — entrances A/B — station structure — Line 13 / Jing-Zhang Railway Heritage Park — N2 / eastern interface

Core design moves

① OPEN: city approach → 1733 forecourt → entrances A/B ② HINGE: two-level public transfer hinge within the station ③ RELEASE: towards the Jing-Zhang Railway Heritage Park, the N2 / eastern public space and the city on both sides

Key

The two existing 1733 buildings Forecourt paving = public space that can be designed directly A / B = existing station entrances (positions verified) Station structure = existing Line 13 elevated station Green band = public space of the Jing-Zhang Railway Heritage

Status marks

- public-space node
- ✓ VERIFIED: plan relations of 1733 / entrances A-B / station structure / Line 13 / Jing-Zhang / North Third Ring
- DESIGN-DEFINED: forecourt arrival, the public hinge in the station, upper-level public transfer, the heritage park interface
- △ TO VERIFY: exact levels, vertical circulation inside the station, engineering interfaces, N2 landing conditions
- NOT PROPOSED AT THIS STAGE: unverified new rail-crossing works

T1 DAZHONGSI: Key Design Section, Spatial Experience and Implementation Boundary

T1 key design section | city ground level → two-level public hinge within the station → upper-level public transfer → Line 13 + Jing-Zhang Railway Heritage Park



Ground-level arrival | 1733 forecourt


Two-level public hinge Upper-level public transfer Line 13 platform

Jing-Zhang Heritage Park deck

Spatial experience | core node aerial view (supporting)



Chain of spatial relations | section relations and implementation boundary

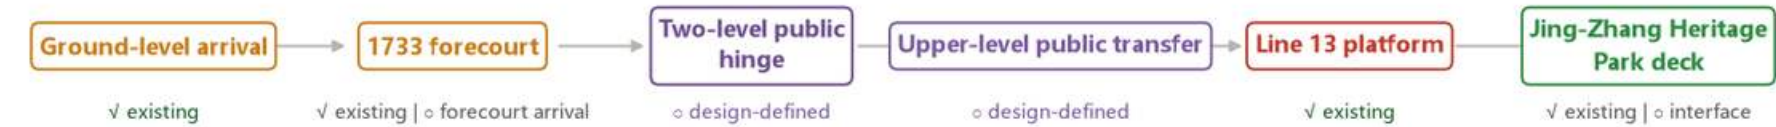

✓ VERIFIED

1733 · A/B · station structure · Line 13 · Jing-Zhang · North Third Ring plan relations
The key existing objects and their plan relations rest on factual evidence.

△ TO VERIFY

Exact levels · vertical circulation inside the station · engineering interfaces · N2 landing conditions
Further specialist verification is required before the next stage.

○ DESIGN-DEFINED

Forecourt arrival · public hinge · upper-level transfer · park interface
This proposal defines the relational organisation and the spatial intervention.

— NOT PROPOSED AT THIS STAGE

Additional new rail-crossing works
No design commitment is made on engineering conditions that lack evidence.

The Jing-Zhang Railway Heritage Park is an independent elevated public park band; there is no bridge, link or track-crossing deck between the station structure and the park; Line 13 is an independent elevated track.