



京张年轮：一圈年轮，两条曲线

百年京张 AI 创新带城市设计开源征集 · 概念方案

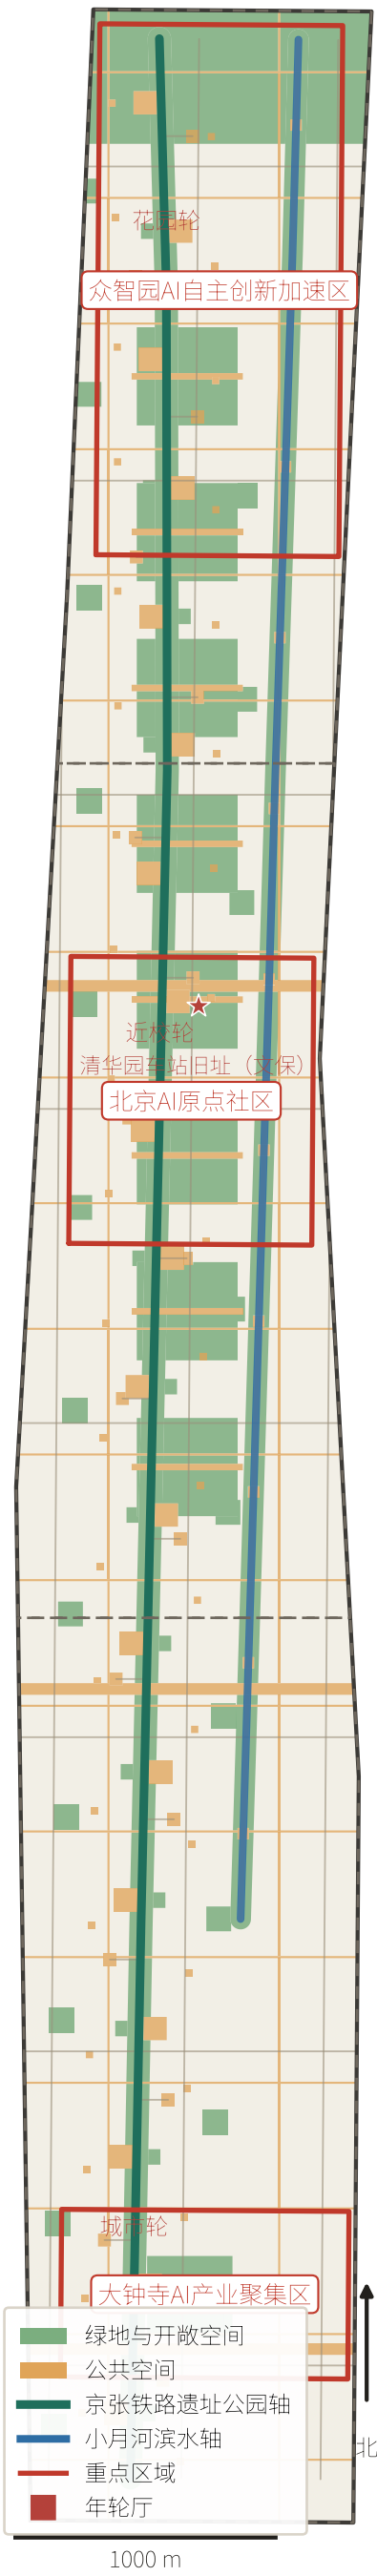

① 区位与三层范围

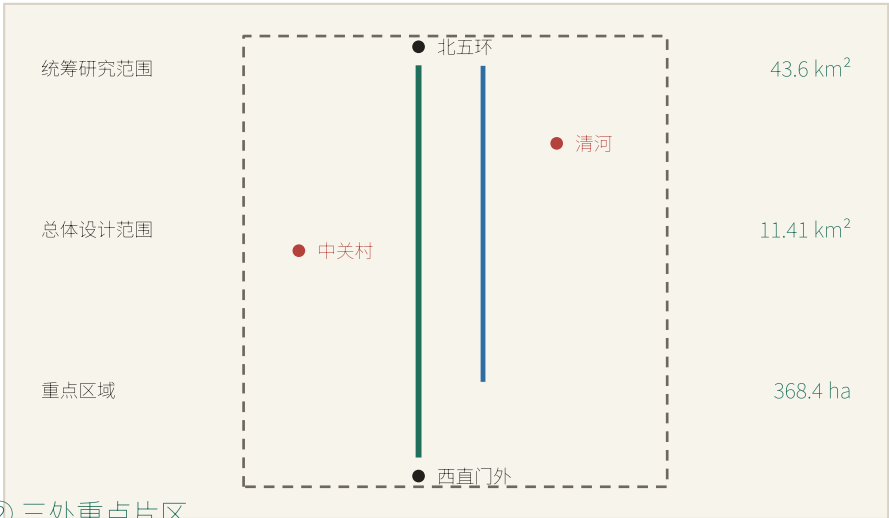

② 三处重点片区

A1
众智园 · 花园轮
192.1 ha
A2
AI 原点社区 · 近校轮
104.3 ha
A3
大钟寺 · 城市轮
72.0 ha

③ 关键结论

1,141.3 21.6% 10.5% 37

ha

场地面积

绿地占比

公共空间

新增体量


京张铁路遗址公园轴 9.7 km × 90 m

小月河滨水轴 6.4 km 治理段 × 80 m (图上绘制 6.2 km)


【注】场地边界为组织方仓库临时粗略几何 (PROVISIONAL_REPOSITORY)，非官方红线。

01 场地总览：双轴夹一城

9.7 km 技术史轴 + 6.4 km 治理段生态轴（图上绘制 6.2 km），中间夹住八大学院与中关村

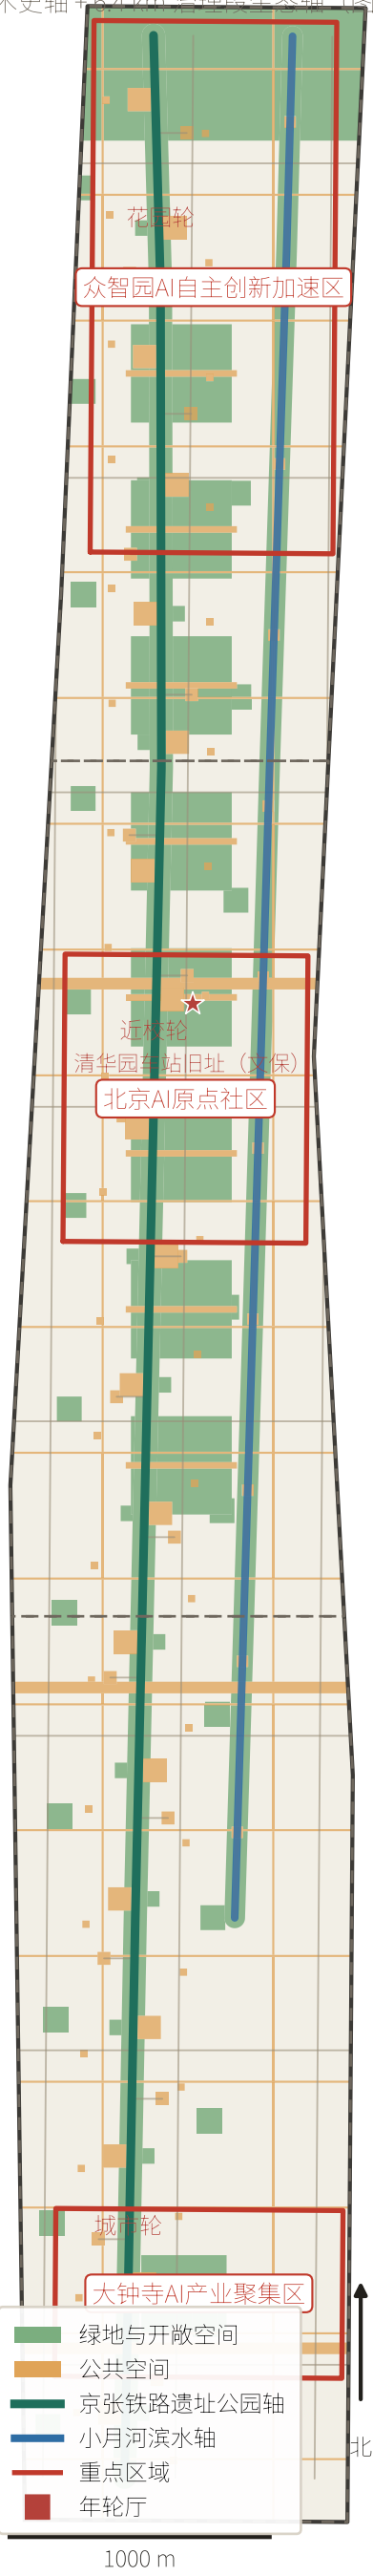

① 区位与三层范围

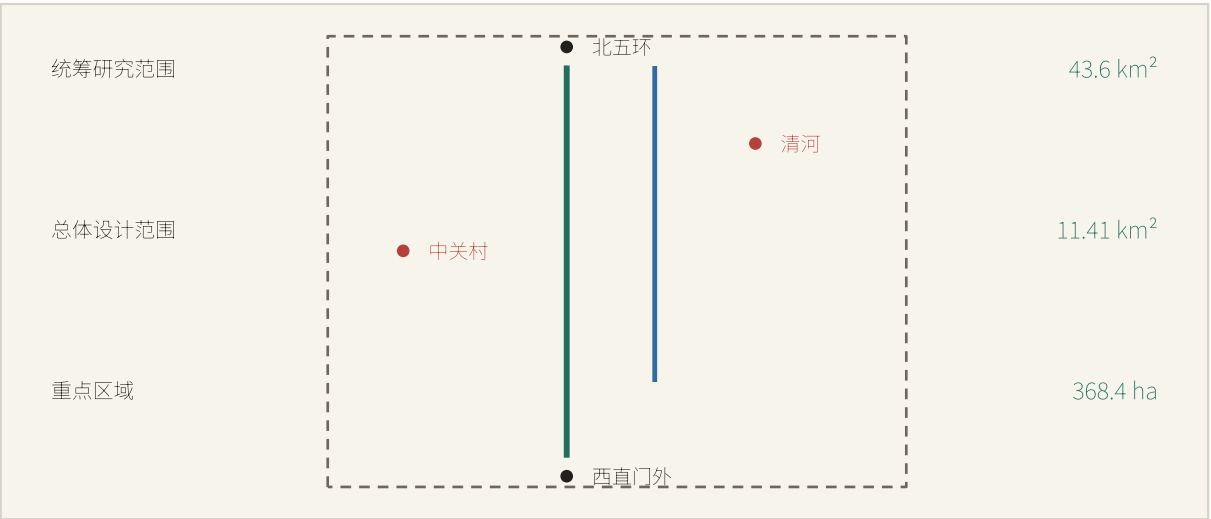

② 双轴

京张铁路遗址公园轴

9.7 km × 90 m

小月河滨水轴

6.4 km 治理段 × 80 m

③ 六段分区

D1 清河·众智园段

D2 学院路北·八大学院段

D3 AI原点社区·五道口段

D4 中关村·知春路段

D5 大钟寺·北下关段

D6 西直门外·南端段

④ 关键数字

19

117

22

37

里 · 每里 496.8 m


1909—2025 年轮

条绿道


处新增概念体量

02 用地结构：三分与剖分

用地为对场地边界的严格剖分：无缝隙、无重叠、面积可复算

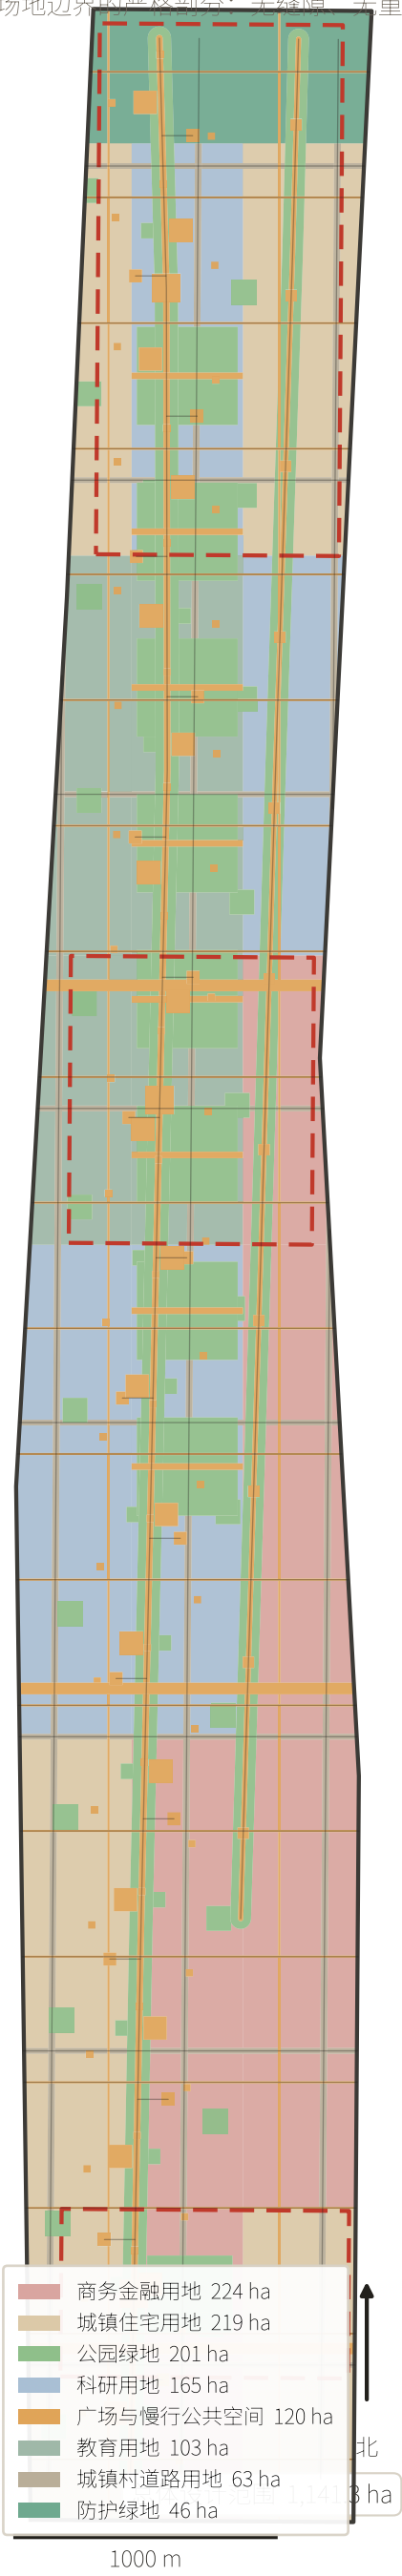

① 用地构成

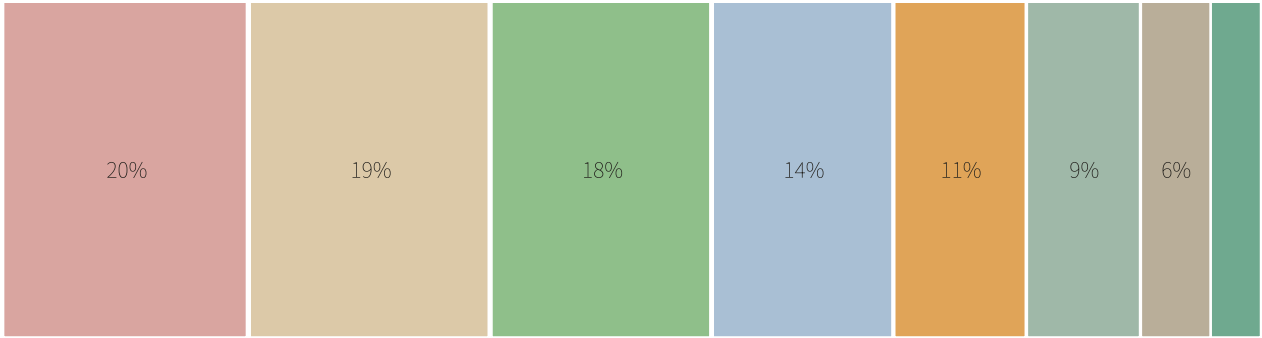

国土空间用地分类（自然资发〔2023〕234号）场地子集


② 用地代码与面积

0902	商务金融用地	223.8 ha
0701	城镇住宅用地	219.4 ha
1401	公园绿地	200.8 ha
0802	科研用地	164.7 ha
1403	广场与慢行公共空间	120.3 ha
0804	教育用地	103.4 ha
1207	城镇村道路用地	63.4 ha
1402	防护绿地	45.5 ha

合计 = 场地面积 1,141.3 ha：用地为严格剖分，无缝隙、无重叠。

03 三处重点片区

三处片区各自对应一种年轮厅原型

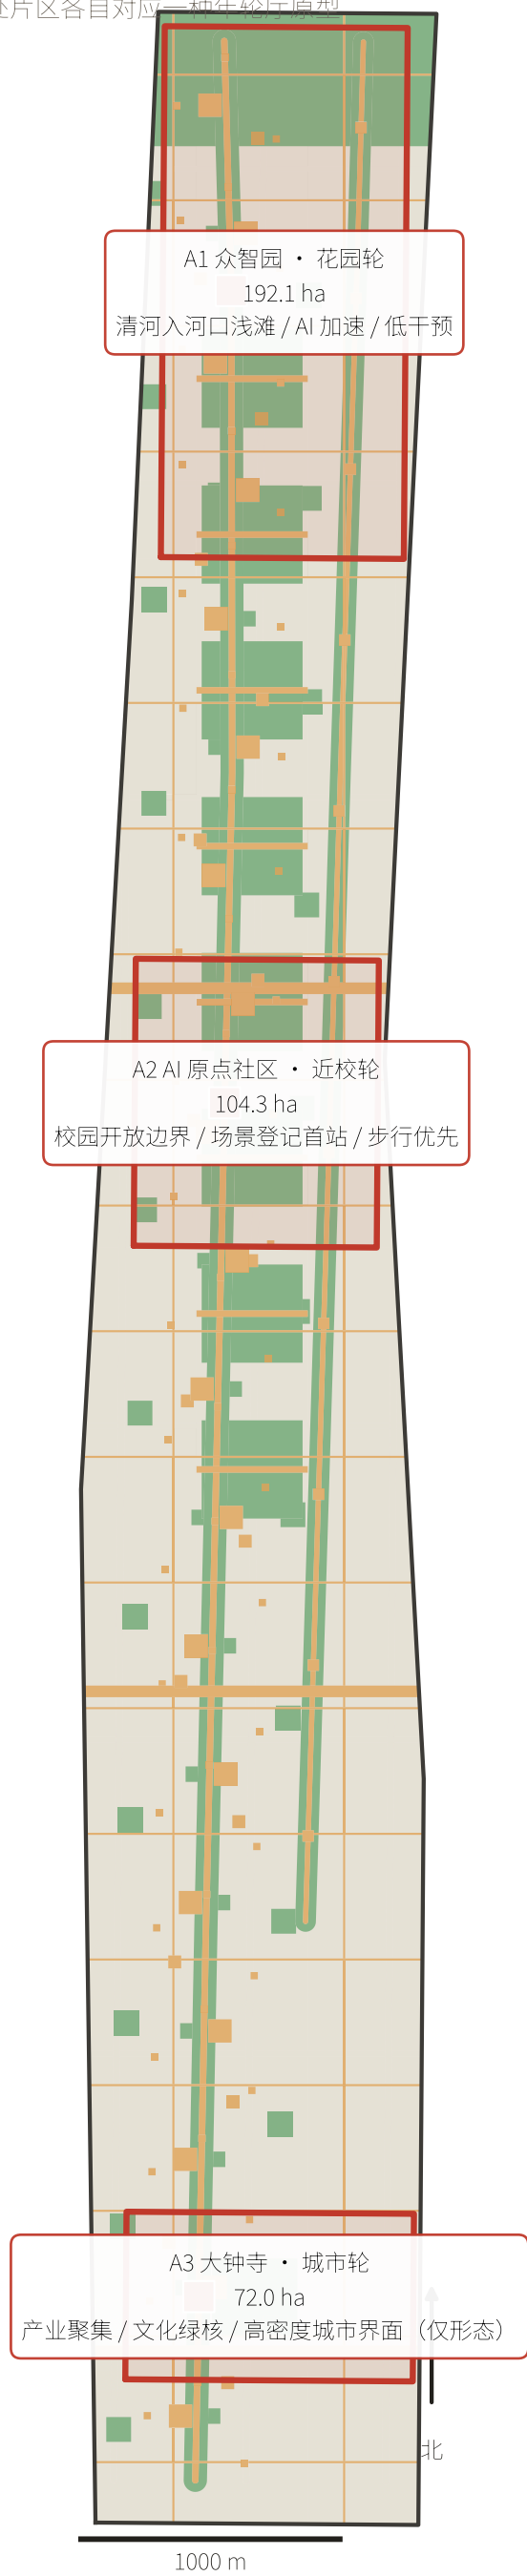

A1

众智园 · 花园轮

192.1 ha

- 清河入河口生态浅滩湿地
- 低干预：只做加法不做减法

A2

AI 原点社区 · 近校轮

104.3 ha

- 校园边界向城市打开（概念选项，~25 m）
须经权利人同意与专项设计
- 场景登记首站：先试、可退

A3

大钟寺 · 城市轮


三处片区与三座年轮厅——对应

三处重点片区(夹塘村、界里方包)临时粗略开发强度指标(SIONAL_REPOSITORY)，面积以公告值 192.1 / 104.3 / 72.0 ha 为准；本方案不声称红线或精确面积。

- 大钟寺文化绿核
- 轨道接驳与公共空间复合

04 慢行与蓝绿系统

22 条绿道 + 双轴慢行主径，东西缝合被铁路与河道切断的街区

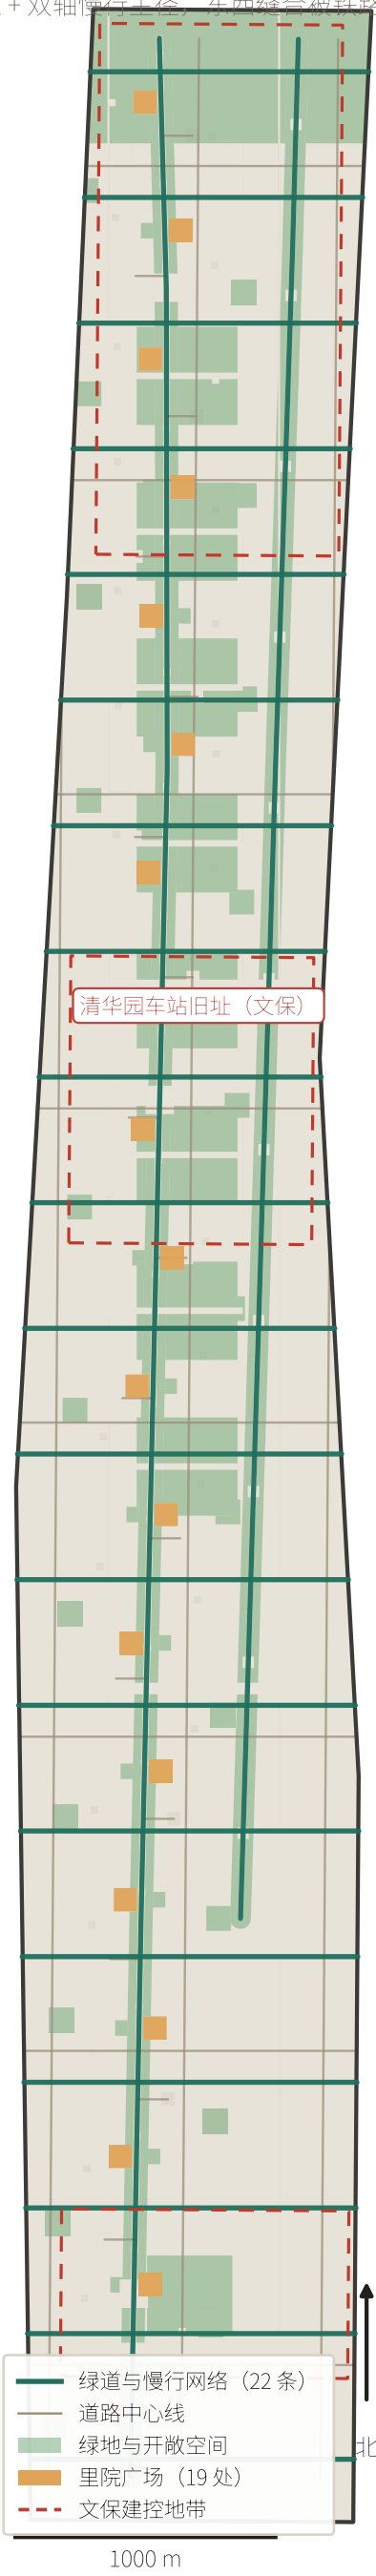

① 慢行网络

绿道总长	40.3 km
绿道条数	22
里院广场	19
接驳 / 滨水驿站	17 / 11
道路中心线	50

② 文保避让

★ 清华园车站旧址（文保）

保护范围与I类建控地带按保守外包近似表达（低置信）；新增体量与建控地带的最小筛查距离 ≈ 12.2 m（基于近似外包，待文物主管部门矢量复核）。控制地带内新建檐口限高 9 m（概念建议）。

③ 测试道路分级

开放	限制	禁入
允许低速配送与接驳测试	限时段、限速度、需人工复核	涉密院所、部队、校园红线内不测试

A · 提交几何复算值

A · 提交几何复算值


site_area_sqm	11,412,825.386 sqm
PROVISIONAL_REPOSITORY 边界 · EPSG:4548	
green_space_area_sqm	2,463,013.830 sqm
green_space.geojson 并集	
public_space_area_sqm	1,203,476.584 sqm
public_space.geojson 并集	
building_footprint_area_sqm	15,855.006 sqm
37 处新增概念体量	
green_ratio	0.2158 ratio
绿地/场地，非法定指标	
public_space_ratio	0.1054 ratio
公共空间/场地	

B · 证据链：每个数字都能追到文件

geometry/site_boundary.geojson	PROV-SITE-001	provisional_boundaries
geometry/green_space.geojson	49 feats	EPSG:4548 UTM
geometry/public_space.geojson	145 feats	EPSG:4548 UTM
geometry/buildings.geojson	37 feats	EPSG:4548 UTM
geometry/land_use.geojson	223 feats	严格剖分：无缝
metrics.json	status=known	scripts/spatial_metrics

C · 未知项：如实留白，不编造

- floor_area_ratio — 控规缺失，现状建筑底数缺失

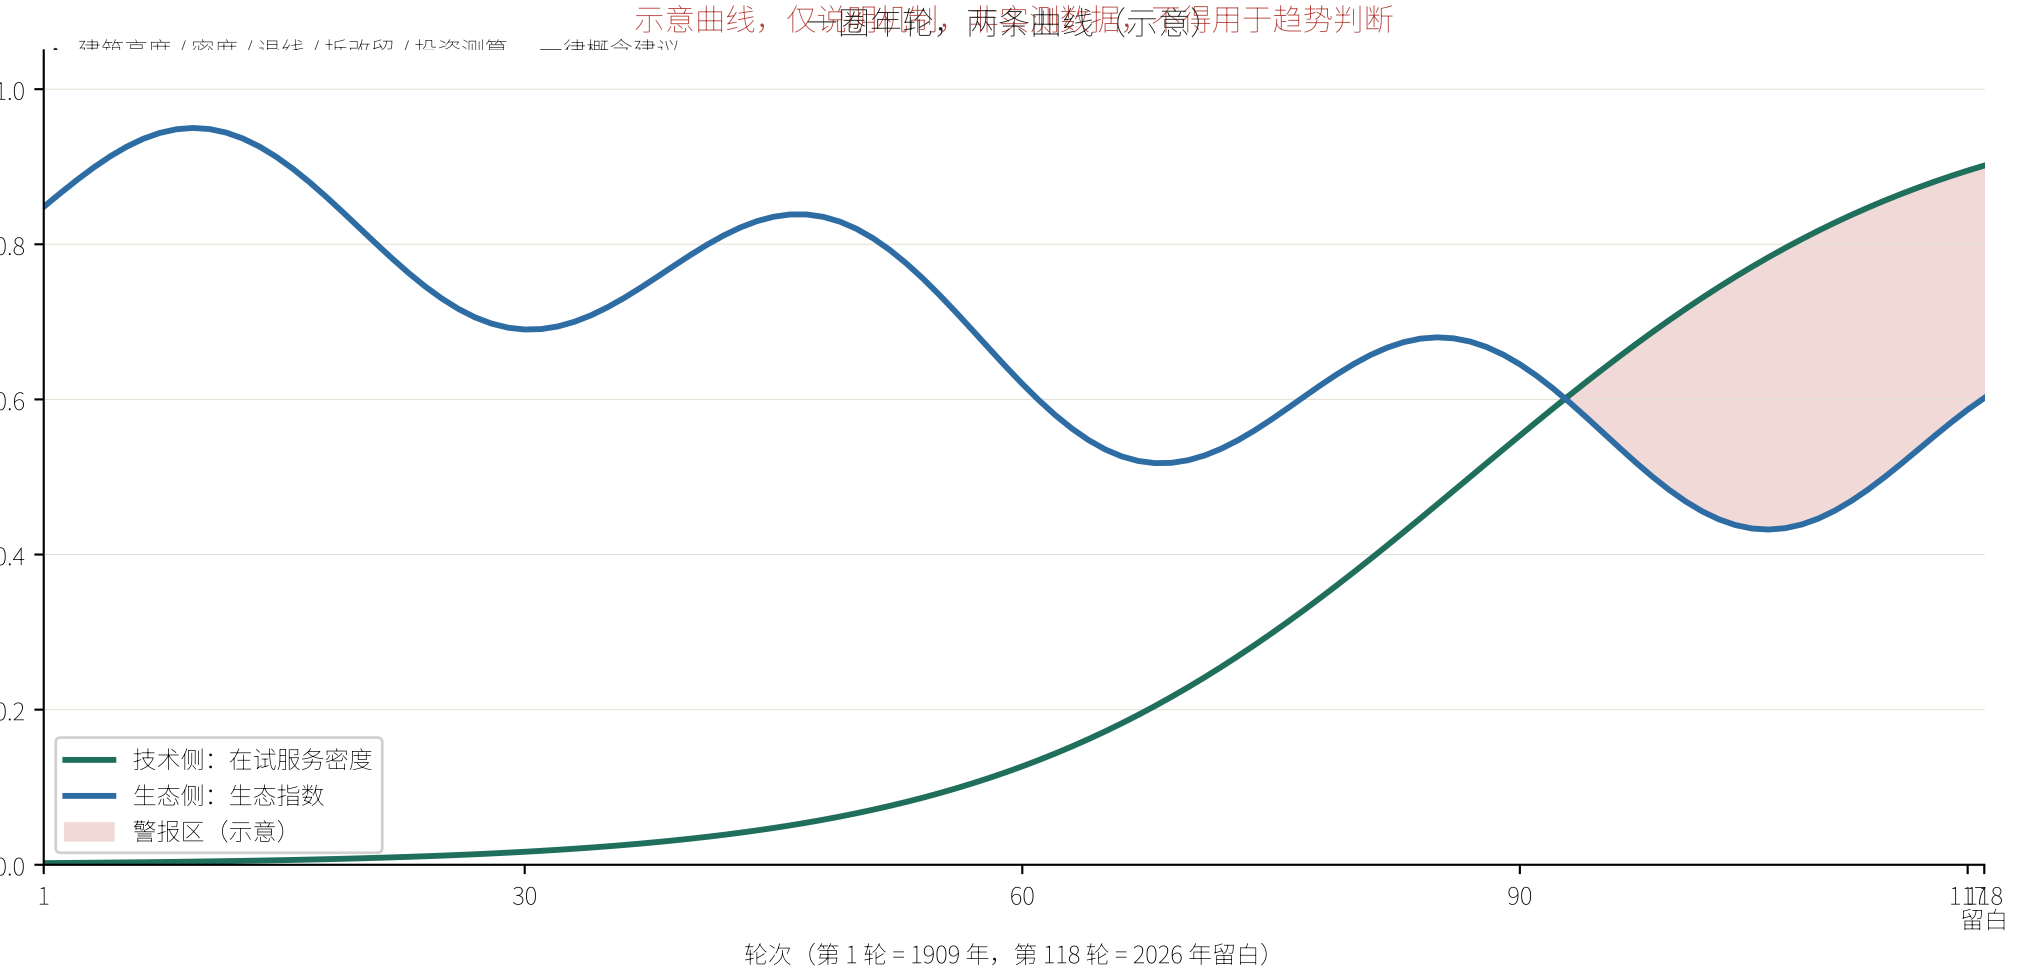

本方案放弃什么

01 放弃全线贯通

涉密院所、部队与部分高校红线内的段落不打通，承认断点，用借道绕行与界面化处理替代。

02 放弃无人化

保留早点摊主、修车师傅、门卫、保洁、驿站管理员，且不把他们的岗位计入效率优化目标。

03 放弃实时全域感知

只在非禁入区布设，数据不出院——院所与社区的数据留在本地服务器。

04 放弃控规类结论

容积率、高度、密度、绿地率、退线、拆改留、道路线位、投资测算一律只写概念建议。

05 放弃一次性建成

十年三期，前三年只做能做的；涉及权属突破的段落承认可能推不动。

06 放弃「优化市井」这个提法本身

改为先试、可退、居民说了算：有期限（12个月）、可退出、有对照（A/B）、结果公开。