

ONE ROUTE, FOUR STATES · JURY SUMMARY

4 m route unbroken; AI on one side; staffed Porch stays open



ONE PUBLIC ROUTE, FOUR CIVIC STATES

Ordinary service first; AI occupies one side; staffed Receipt Porch stays open



S7 OPEN DAY · PUBLIC CROSS RUNS INDEPENDENTLY

CONCEPT-GENERATED / NOT FIELD EVIDENCE; use vector model for dimensions

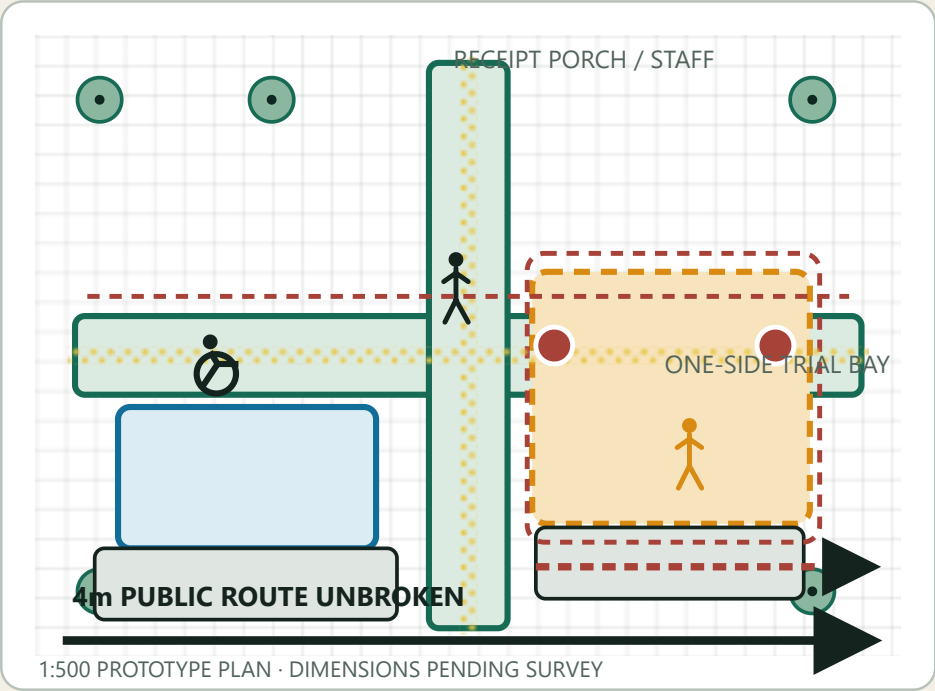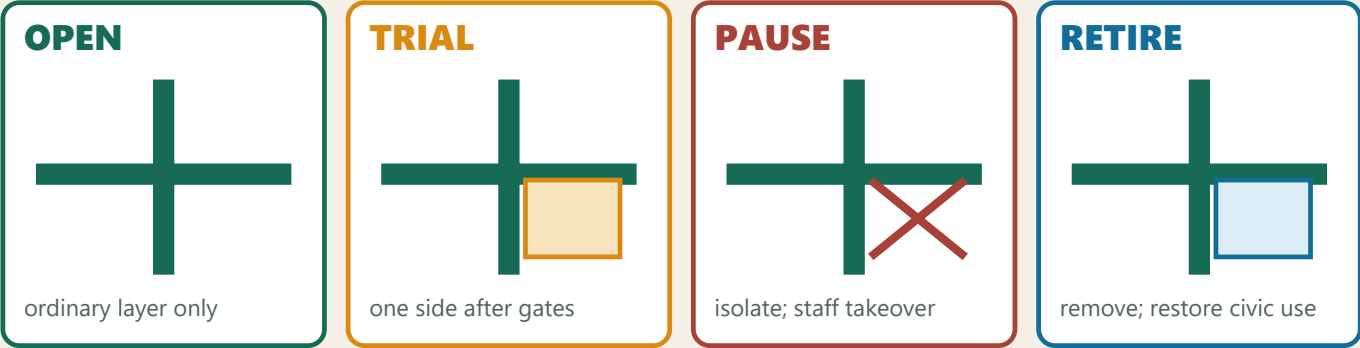

4m INVARIANT

unbroken in OPEN / TRIAL /
PAUSE / RETIRE

AI ON ONE SIDE

bay cannot enter public, fire
or removal routes


STAFFED SERVICE STAYS

state, appeal, decision and
recovery remain visible

90-SECOND JURY ROUTE

spatial conclusion → prototype → decision → next gate → context

90-SECOND JURY ROUTE · SPACE FIRST, THEN EVIDENCE

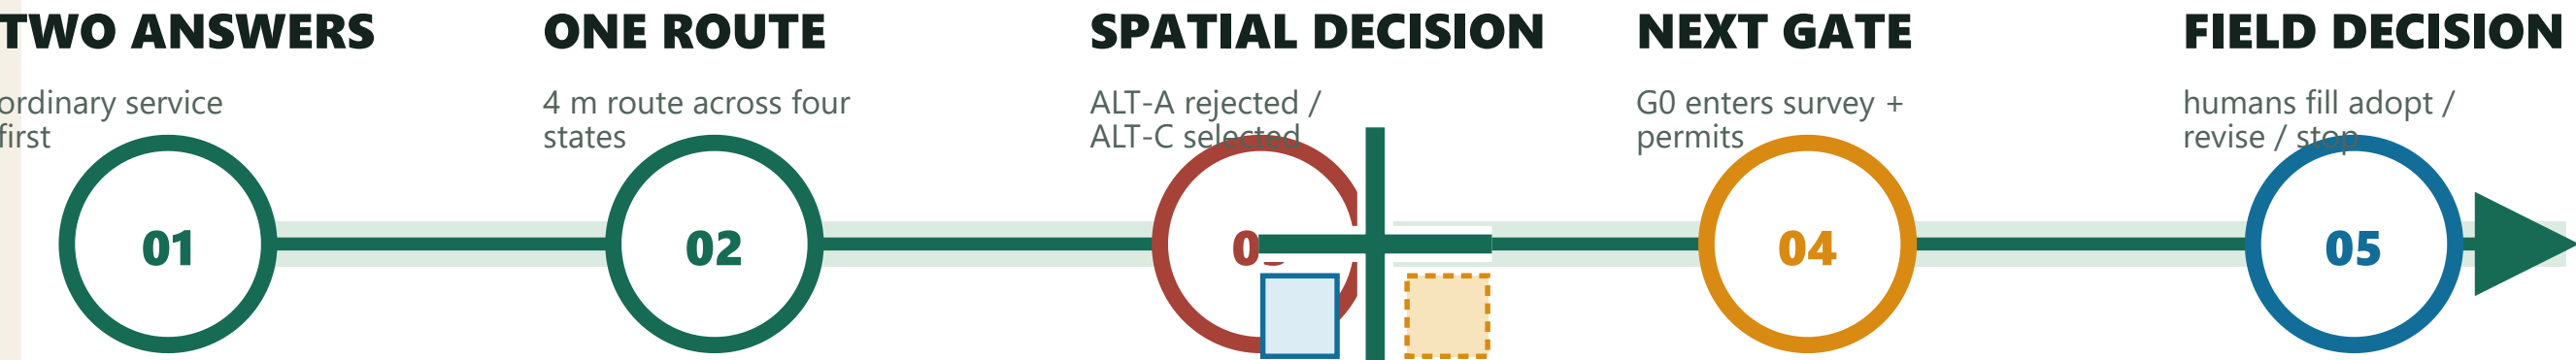

5 sec: one route / four states · 90 sec: decision + next gate · 10 min: component, owner, stop, recovery

Approved context locates the scheme but does not replace the mechanism; field unknowns remain blank.

PUBLIC SOURCES, STATUS + PRECISION

published, approved, design and unknown stay distinct

EVIDENCE STATUS + PRECISION BOUNDARY · FOUR STATES NEVER MIX

EXISTING PUBLISHED

Phase II completion and reported use

APPROVED CONTEXT

1,668.2 ha, 9 km, belt-axis-centres-nodes

DESIGN PROPOSAL

4 m route, one-side bay, Receipt Porch

UNKNOWN

survey, title, entrances, utilities, permits, performance

Public reporting proves published status; it does not replace participant fieldwork, survey, title or acceptance.


Official 1,668.2 ha context and submitted 11.4 sq km provisional geometry are separately recorded.

APPROVED CONTEXT + OPERATING OVERLAY

spine/stations/wings form a stoppable overlay

JING-ZHANG OPERATING LAYER ON APPROVED CONTEXT

Planning is the credible base; the civic cross and stations are the design protagonists

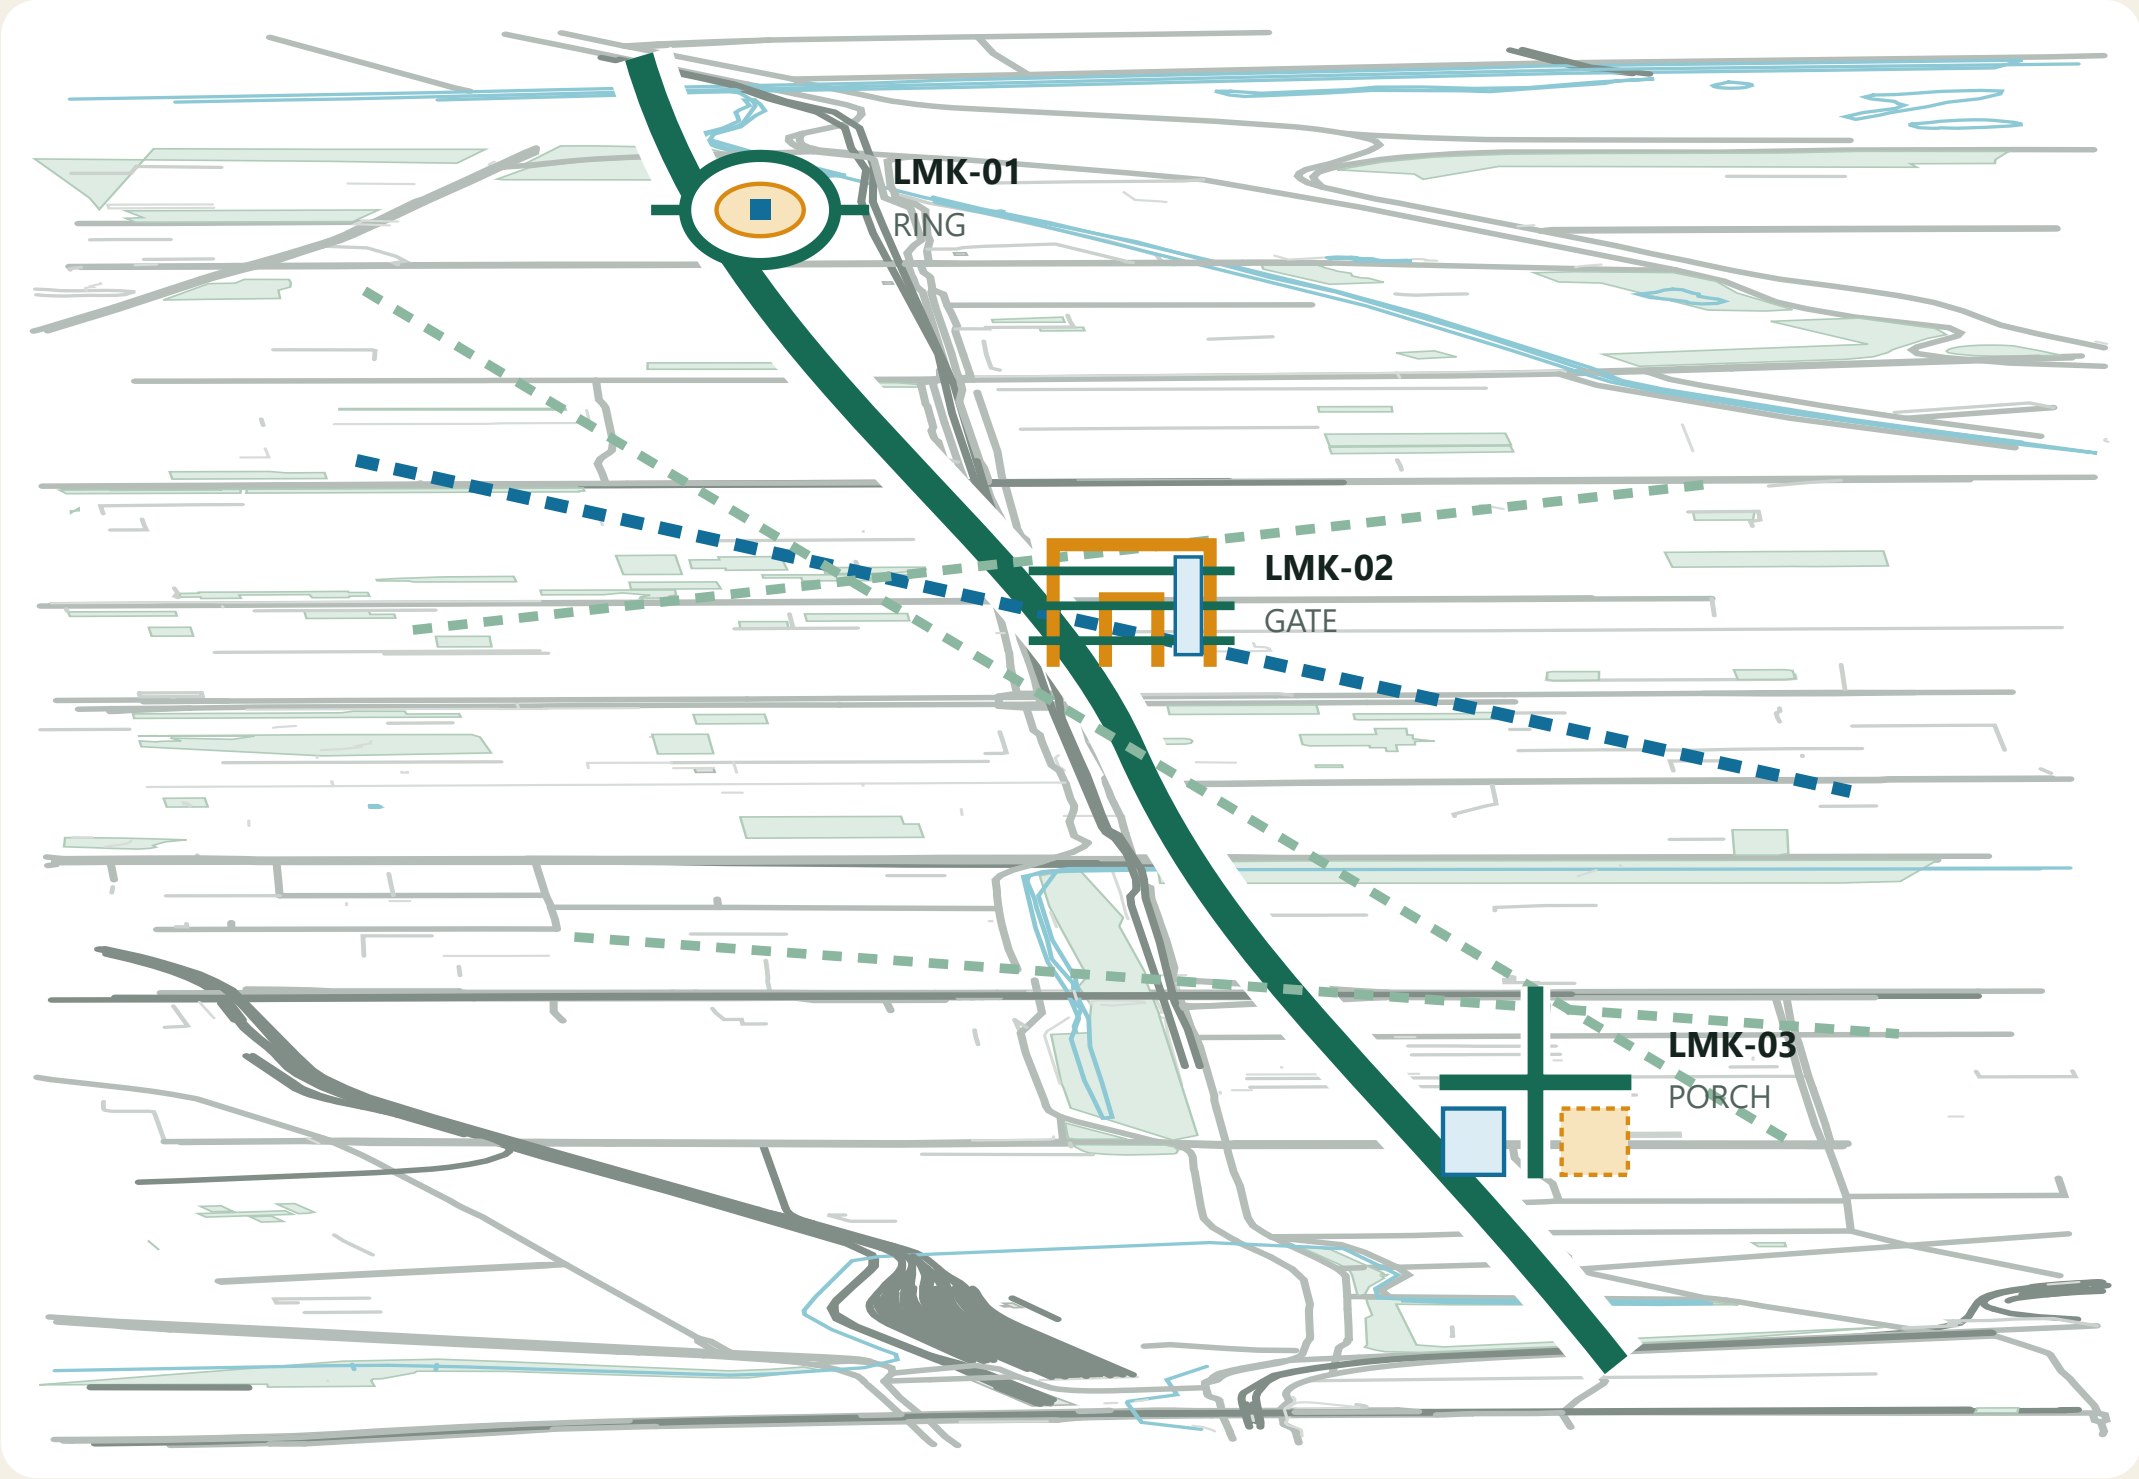

PUBLISHED GREEN BELT

spine/stations/wings = stoppable, removable overlay

EXISTING / PUBLISHED

9 km belt, slow-mobility links, Dazhongsi centre

DESIGN PROPOSAL

4 m route, one-side bay, staffed Porch

INTERFACE WINDOWS

Ring bypass / Gate passage / Porch cross

UNKNOWN

survey, title, entrances, utilities, permits


Map data © OpenStreetMap contributors · ODbL · 2026-08-13

DAZHONGSI GROUND INTERFACE

public, transit, blue-green and temporary trial

DAZHONGSI GROUND INTERFACE · PUBLIC / TRANSIT / BLUE-GREEN

1:2000 concept plan + one continuous longitudinal transect

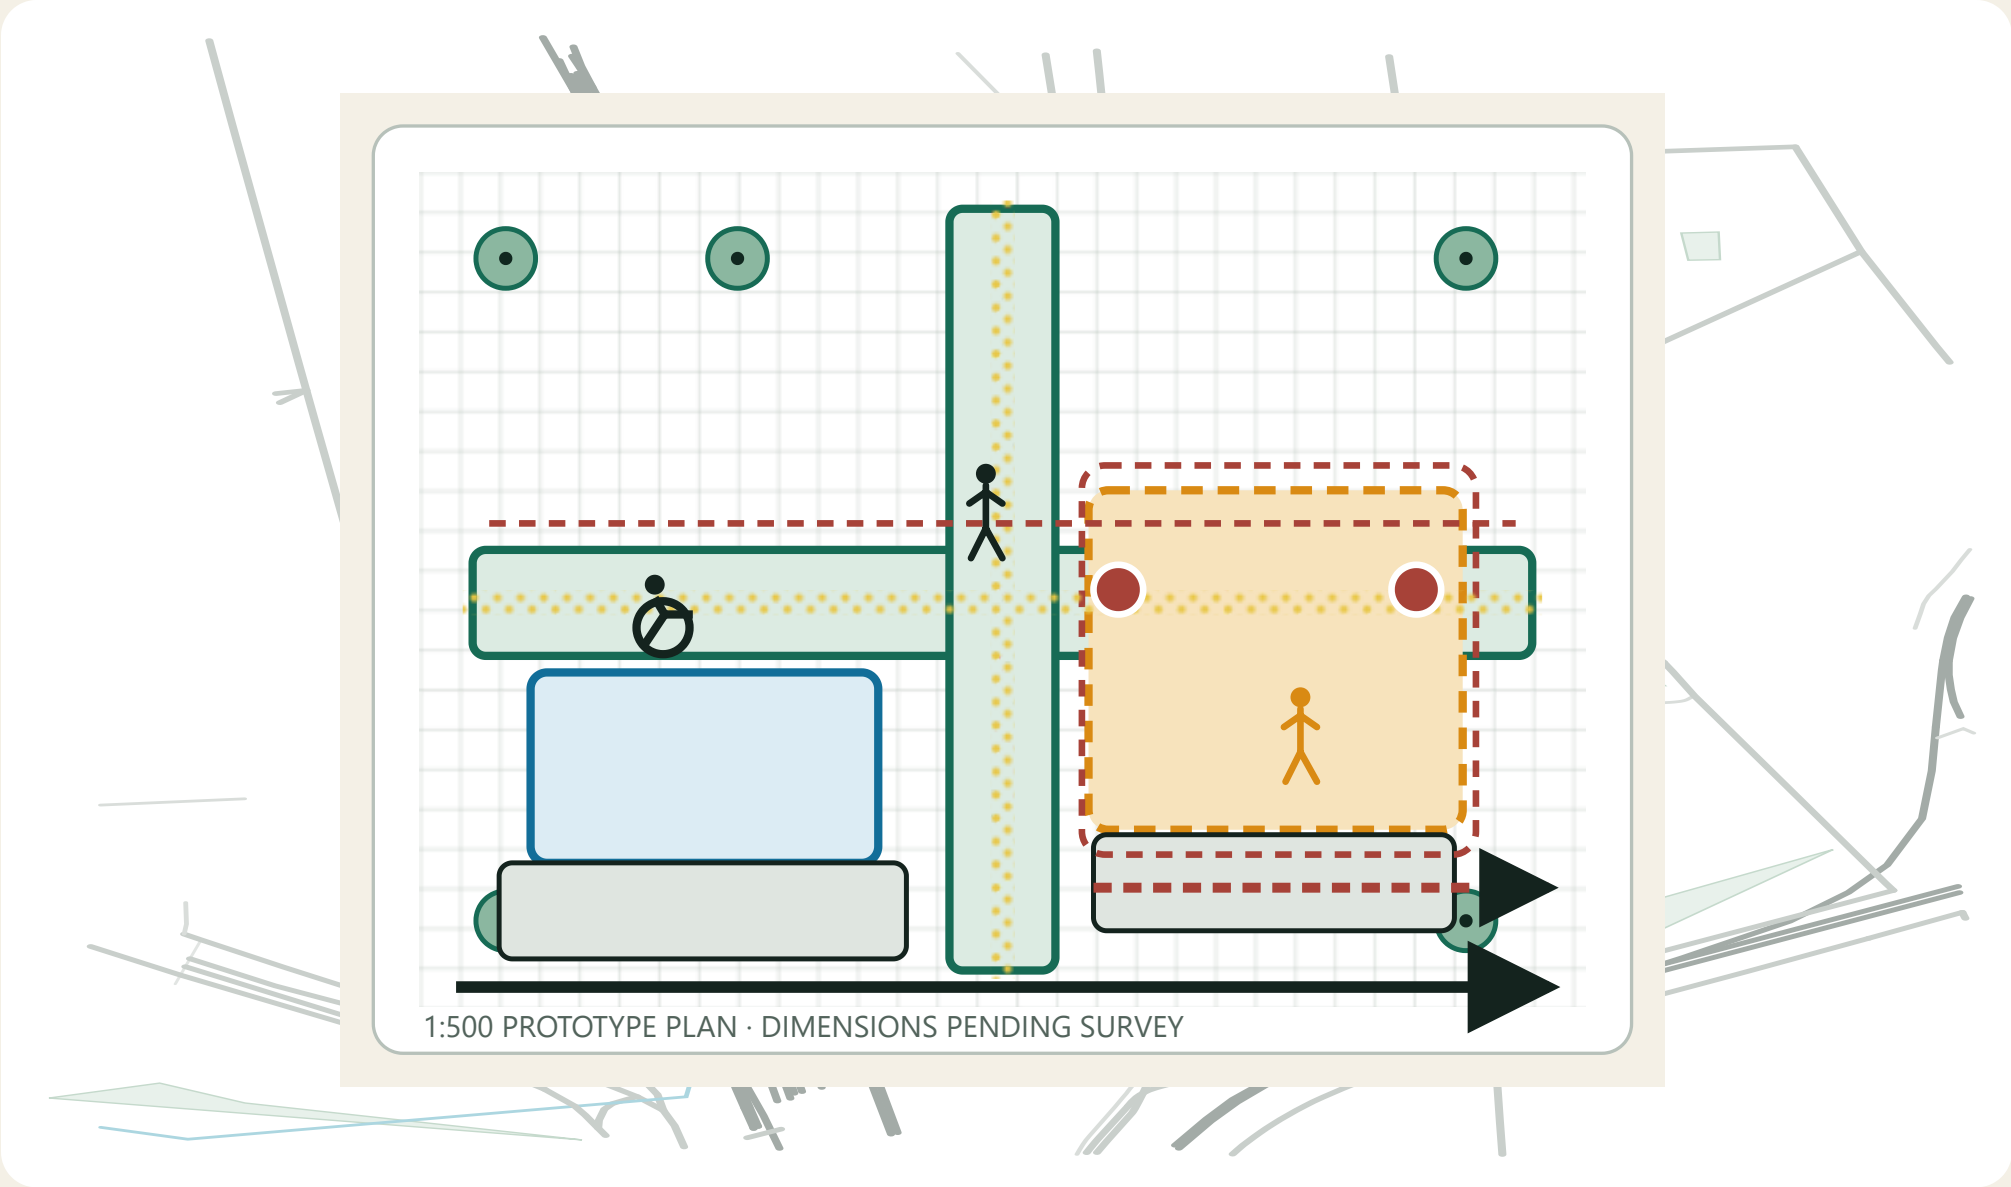


PUBLIC GROUND
route / waiting / shade /
staffed service

TRANSIT
rail direction / transit /
crossing

BLUE-GREEN
tree pits / rainwater / egress

TEMPORARY
one-side trial bay / reversible
buffer

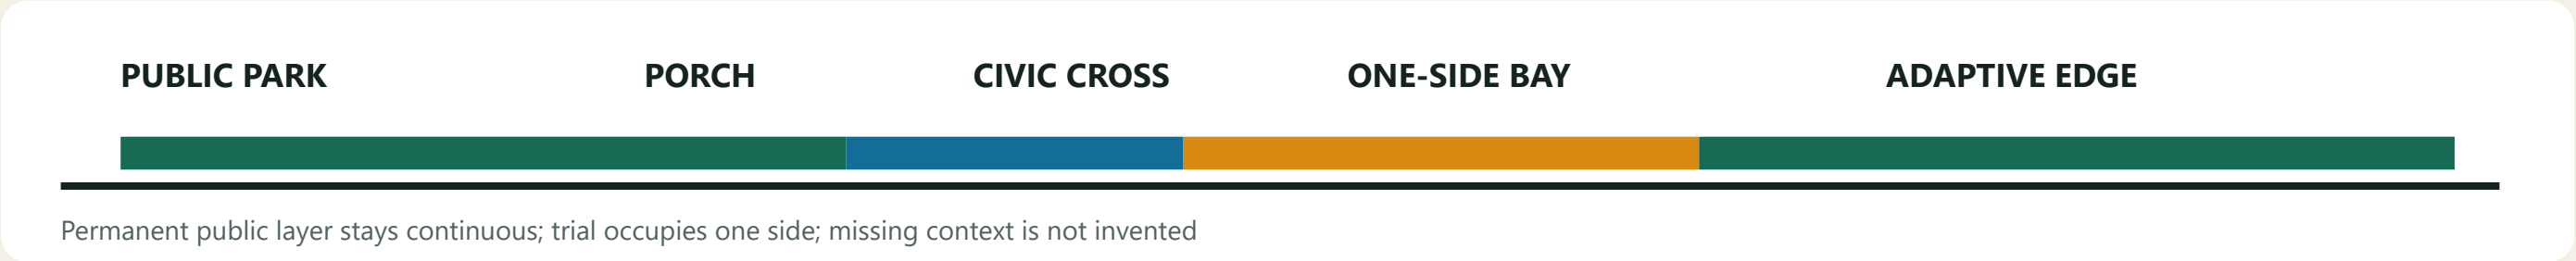

THREE-LANDMARK ARCHITECTURAL FAMILY

verification as Ring, translation as Gate, decision as Porch



RING, GATE, PORCH · ONE MATERIAL FAMILY, THREE DISTINCT TYPES

S7 occupies 60%; entrances, staffed interface and back-of-house visible




DAZHONGSI · ORDINARY OPEN DAY

CONCEPT-GENERATED / NOT FIELD EVIDENCE; use vector model for dimensions

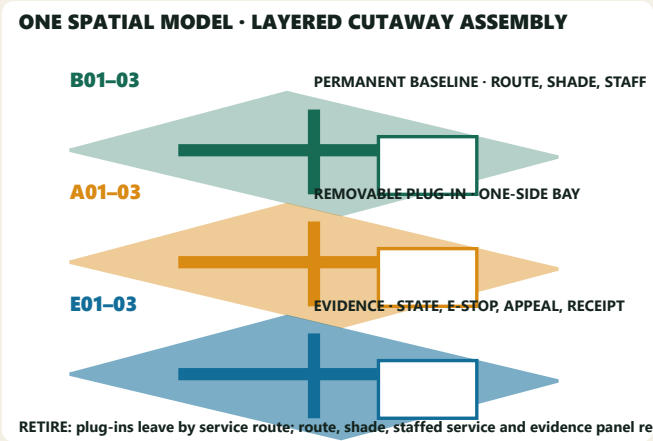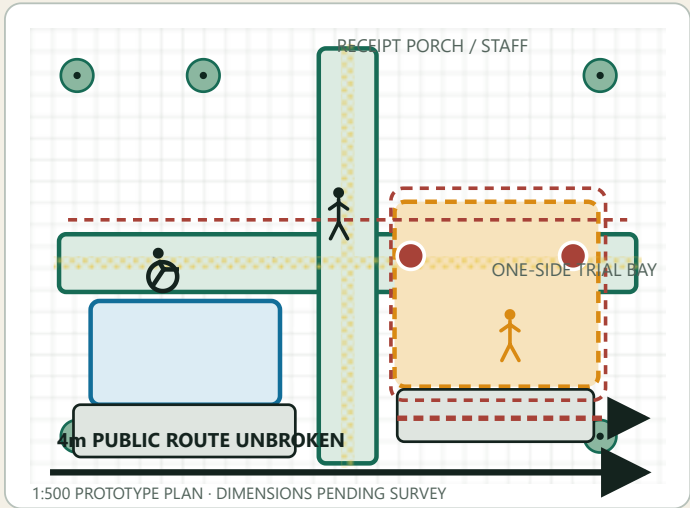


RETIRE: plug-ins leave by service route; route, shade, staffed service and evidence panel rem

VERIFICATION RING · PUBLIC OUTER / TEST INNER

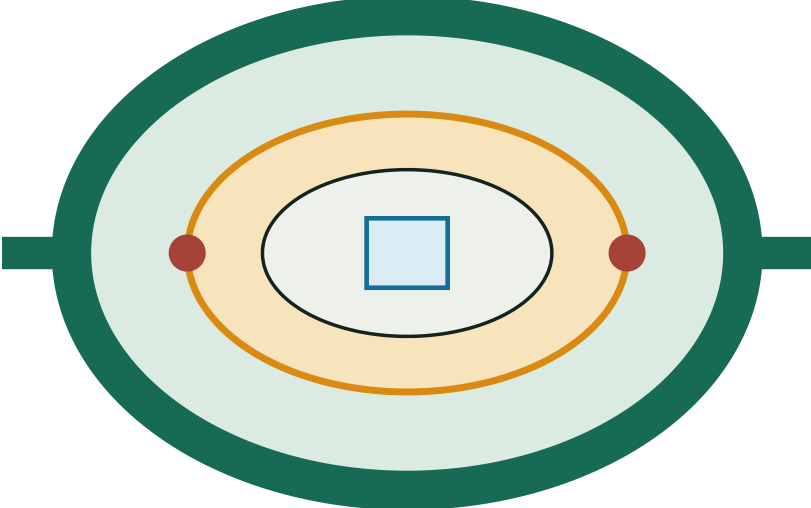

When inner court closes, public ring, observation and east equipment exit rem

TRANSLATION GATE · 3 PASSAGES + STAFF

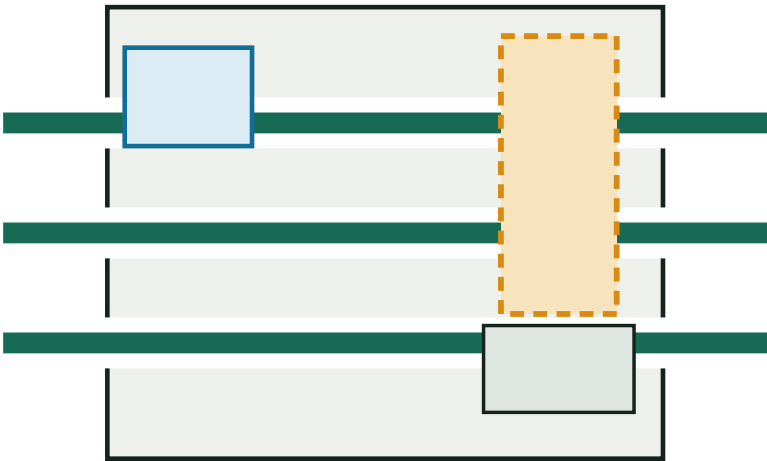

Plug-in wall closes at night; static signs, staffed desk and routes remain

T2/S2 have entry, closure and equipment exit; S7 same camera proves the public route stays

FIVE REGIONAL EXCHANGE CONTRACTS

problem, capability, validation, evidence, owner and exit

FIVE REGIONAL EXCHANGE CONTRACTS · EACH CAN FAIL AND EXIT

BEIWEI COMMUNITY

resident issue → S5/S6 →
access/climate evidence

FUTURE SCIENCE CITY

research task → T1 →
reproducibility report

HUAIROU SCIENCE CITY

instrument condition → T3 →
energy/offline log

E-TOWN

manufacture/maintenance → T2/S7
→ safety/retirement list

JING-JIN-JI

cross-region issue → stations →
reusable knowledge

Institutions are suggested roles, not partnerships; invalid rights, baseline or permits stop exchange.

ZHONGZHIYUAN · VERIFICATION RING


public outer ring independent of controlled inner court



ZHONGZHIYUAN · VERIFICATION RING

CONCEPT-GENERATED / NOT FIELD EVIDENCE; use vector model for dimensions

VERIFICATION RING · PUBLIC OUTER / TEST INNER

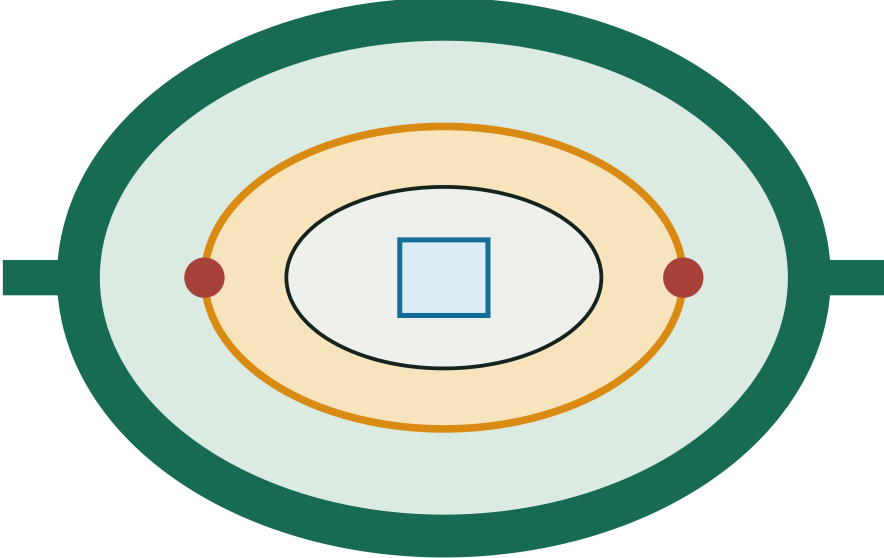

When inner court closes, public ring, observation and east equipment ex

PUBLIC BYPASS


Outer ring continues when inner court closes

FAILURE DISPLAY + EXIT

Dual e-stop, observation and east exit visible

AI ORIGIN · TRANSLATION GATE


three account-free routes pass staffed service and closable plug-ins

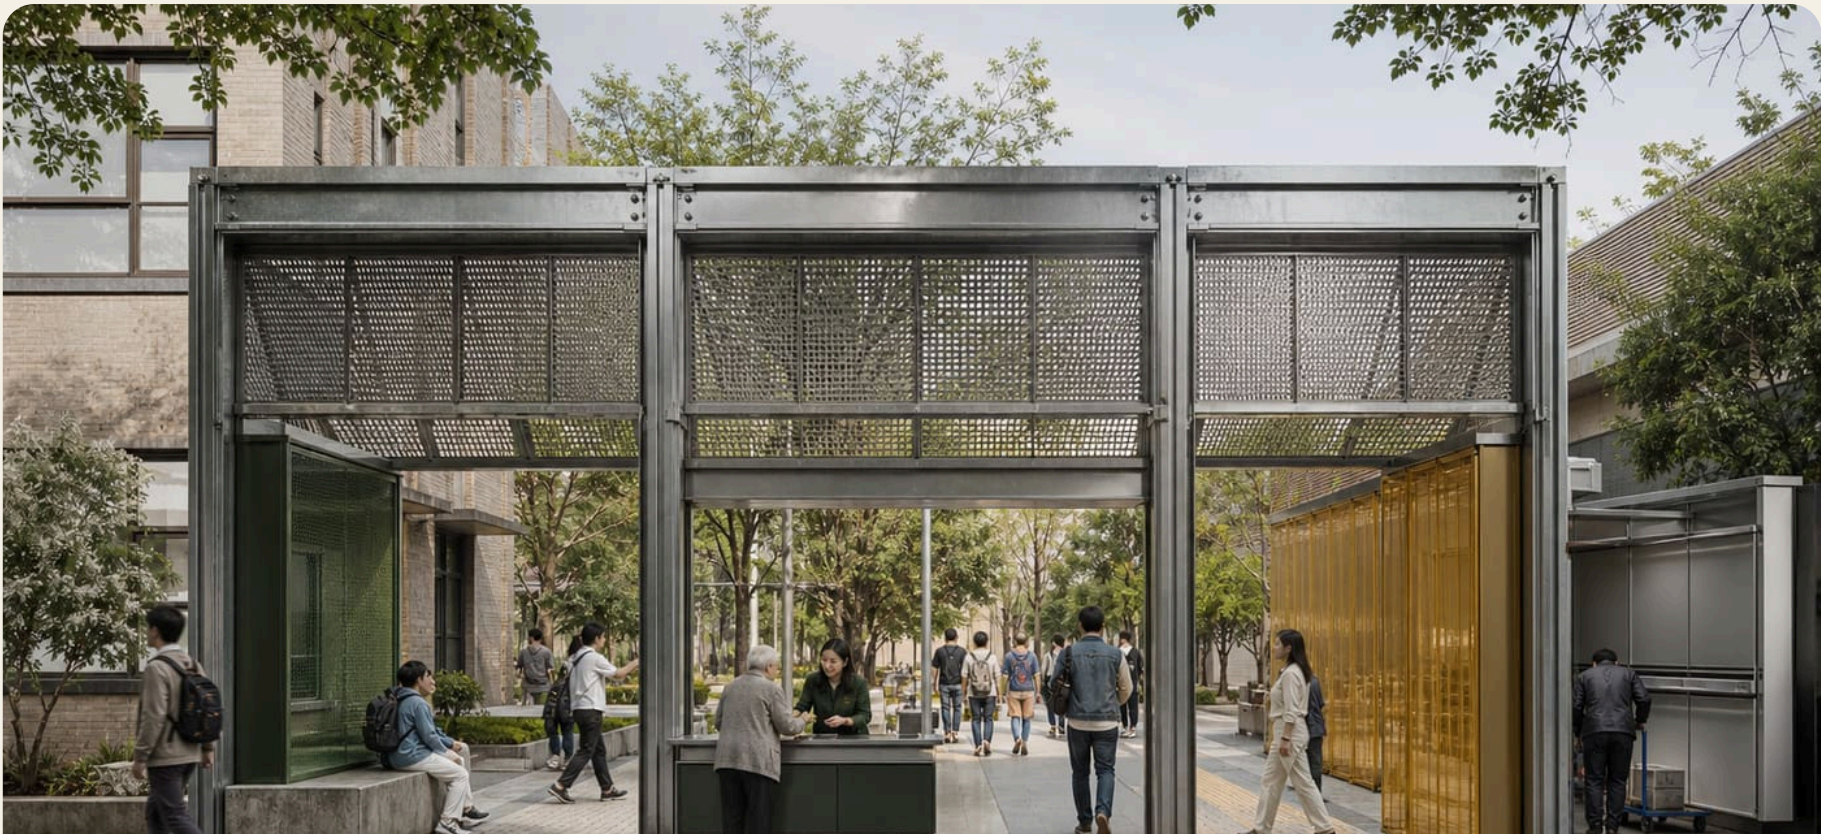

AI ORIGIN · TRANSLATION GATE

CONCEPT-GENERATED / NOT FIELD EVIDENCE; use vector model for dimensions

TRANSLATION GATE · 3 PASSAGES + STAFF

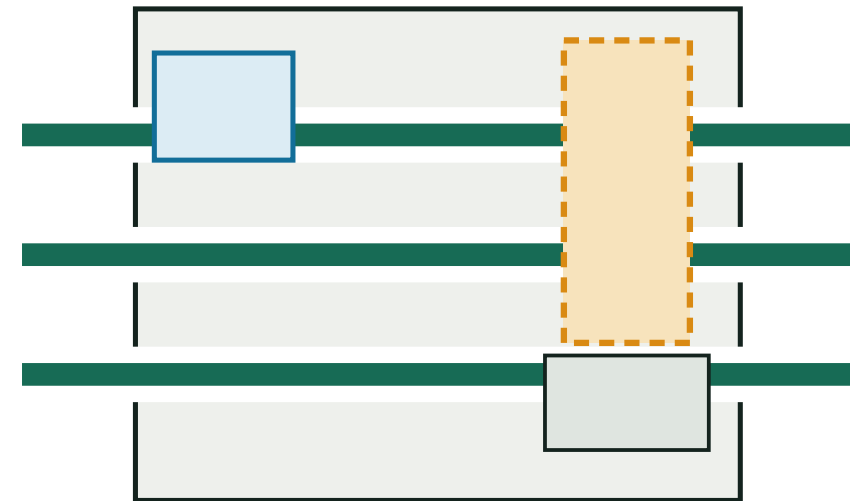

Plug-in wall closes at night; static signs, staffed desk and routes remain

ACCOUNT-FREE PASSAGE

Three routes and staffed desk remain complete

PLUG-IN WALL + REVIEW


Plug-ins close at night; staff service continues

S7 ALTERNATIVES + SPATIAL DECISION

one yardstick rejects the option that cuts the route

ONE YARDSTICK · THREE OPTIONS, ONE PUBLIC REJECTION


ALT-A CENTRAL MIXING

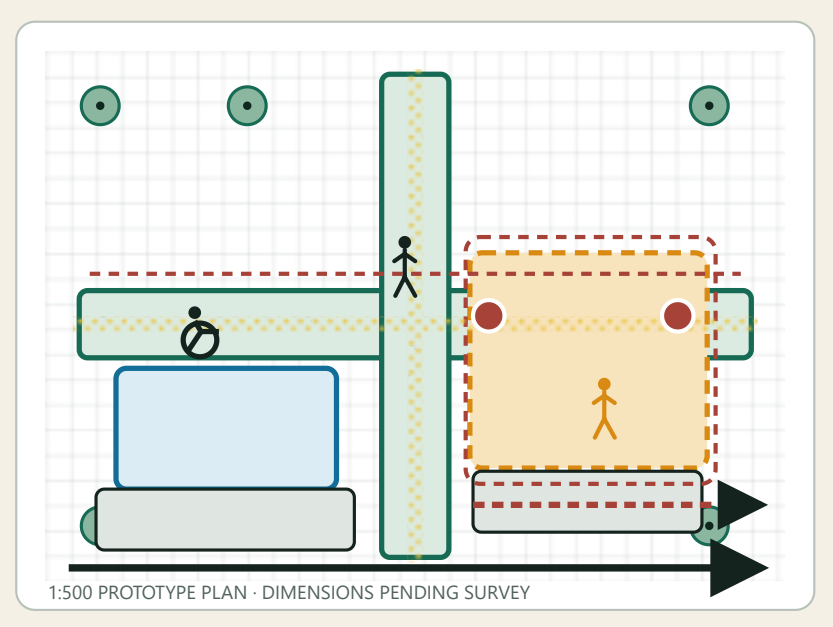

REJECT · CUTS PUBLIC CROSS

Hard conflict among public, fire and removal routes.


ALT-B SPLIT BAYS

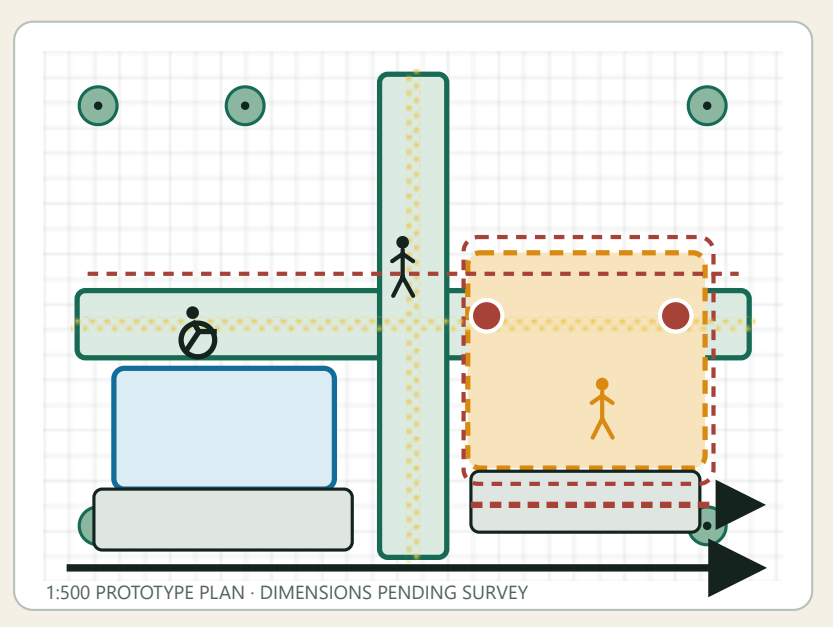

REVISE · FRAGMENTED CONTROL

Routes remain but posts and exit are dispersed.

ALT-C ONE-SIDE BAY

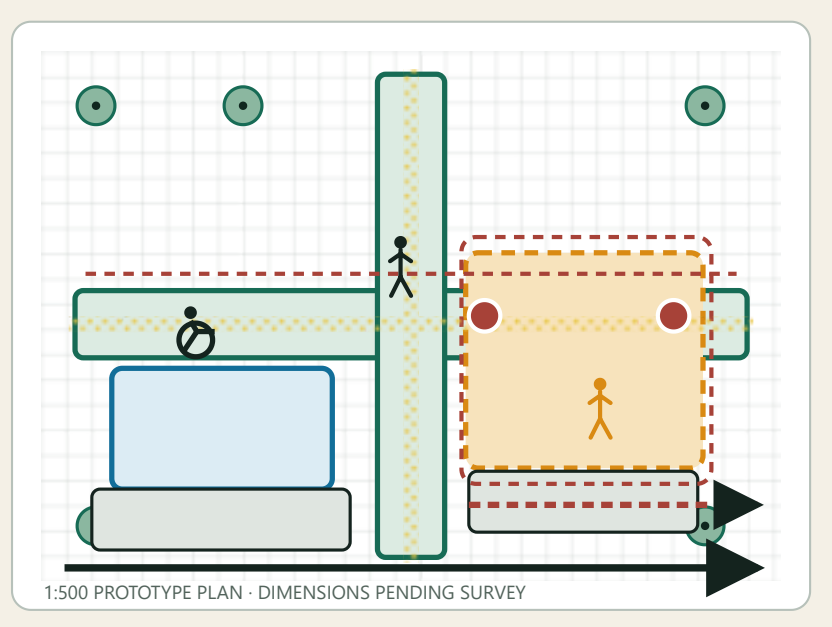

ADVANCE · ROUTE CONTINUOUS


AI is concentrated; posts, e-stop and exit are reachable.

Result comes from local-metric geometry audit; it is not field traffic, safety or acceptance evidence.

reject_design / revise_design / advance_design ≠ adopt / revise / stop

ALT-C 1:500 ARCHITECTURE–SITE PLAN


curb, ramp, tactile, waiting, blue-green, posts, fire and removal

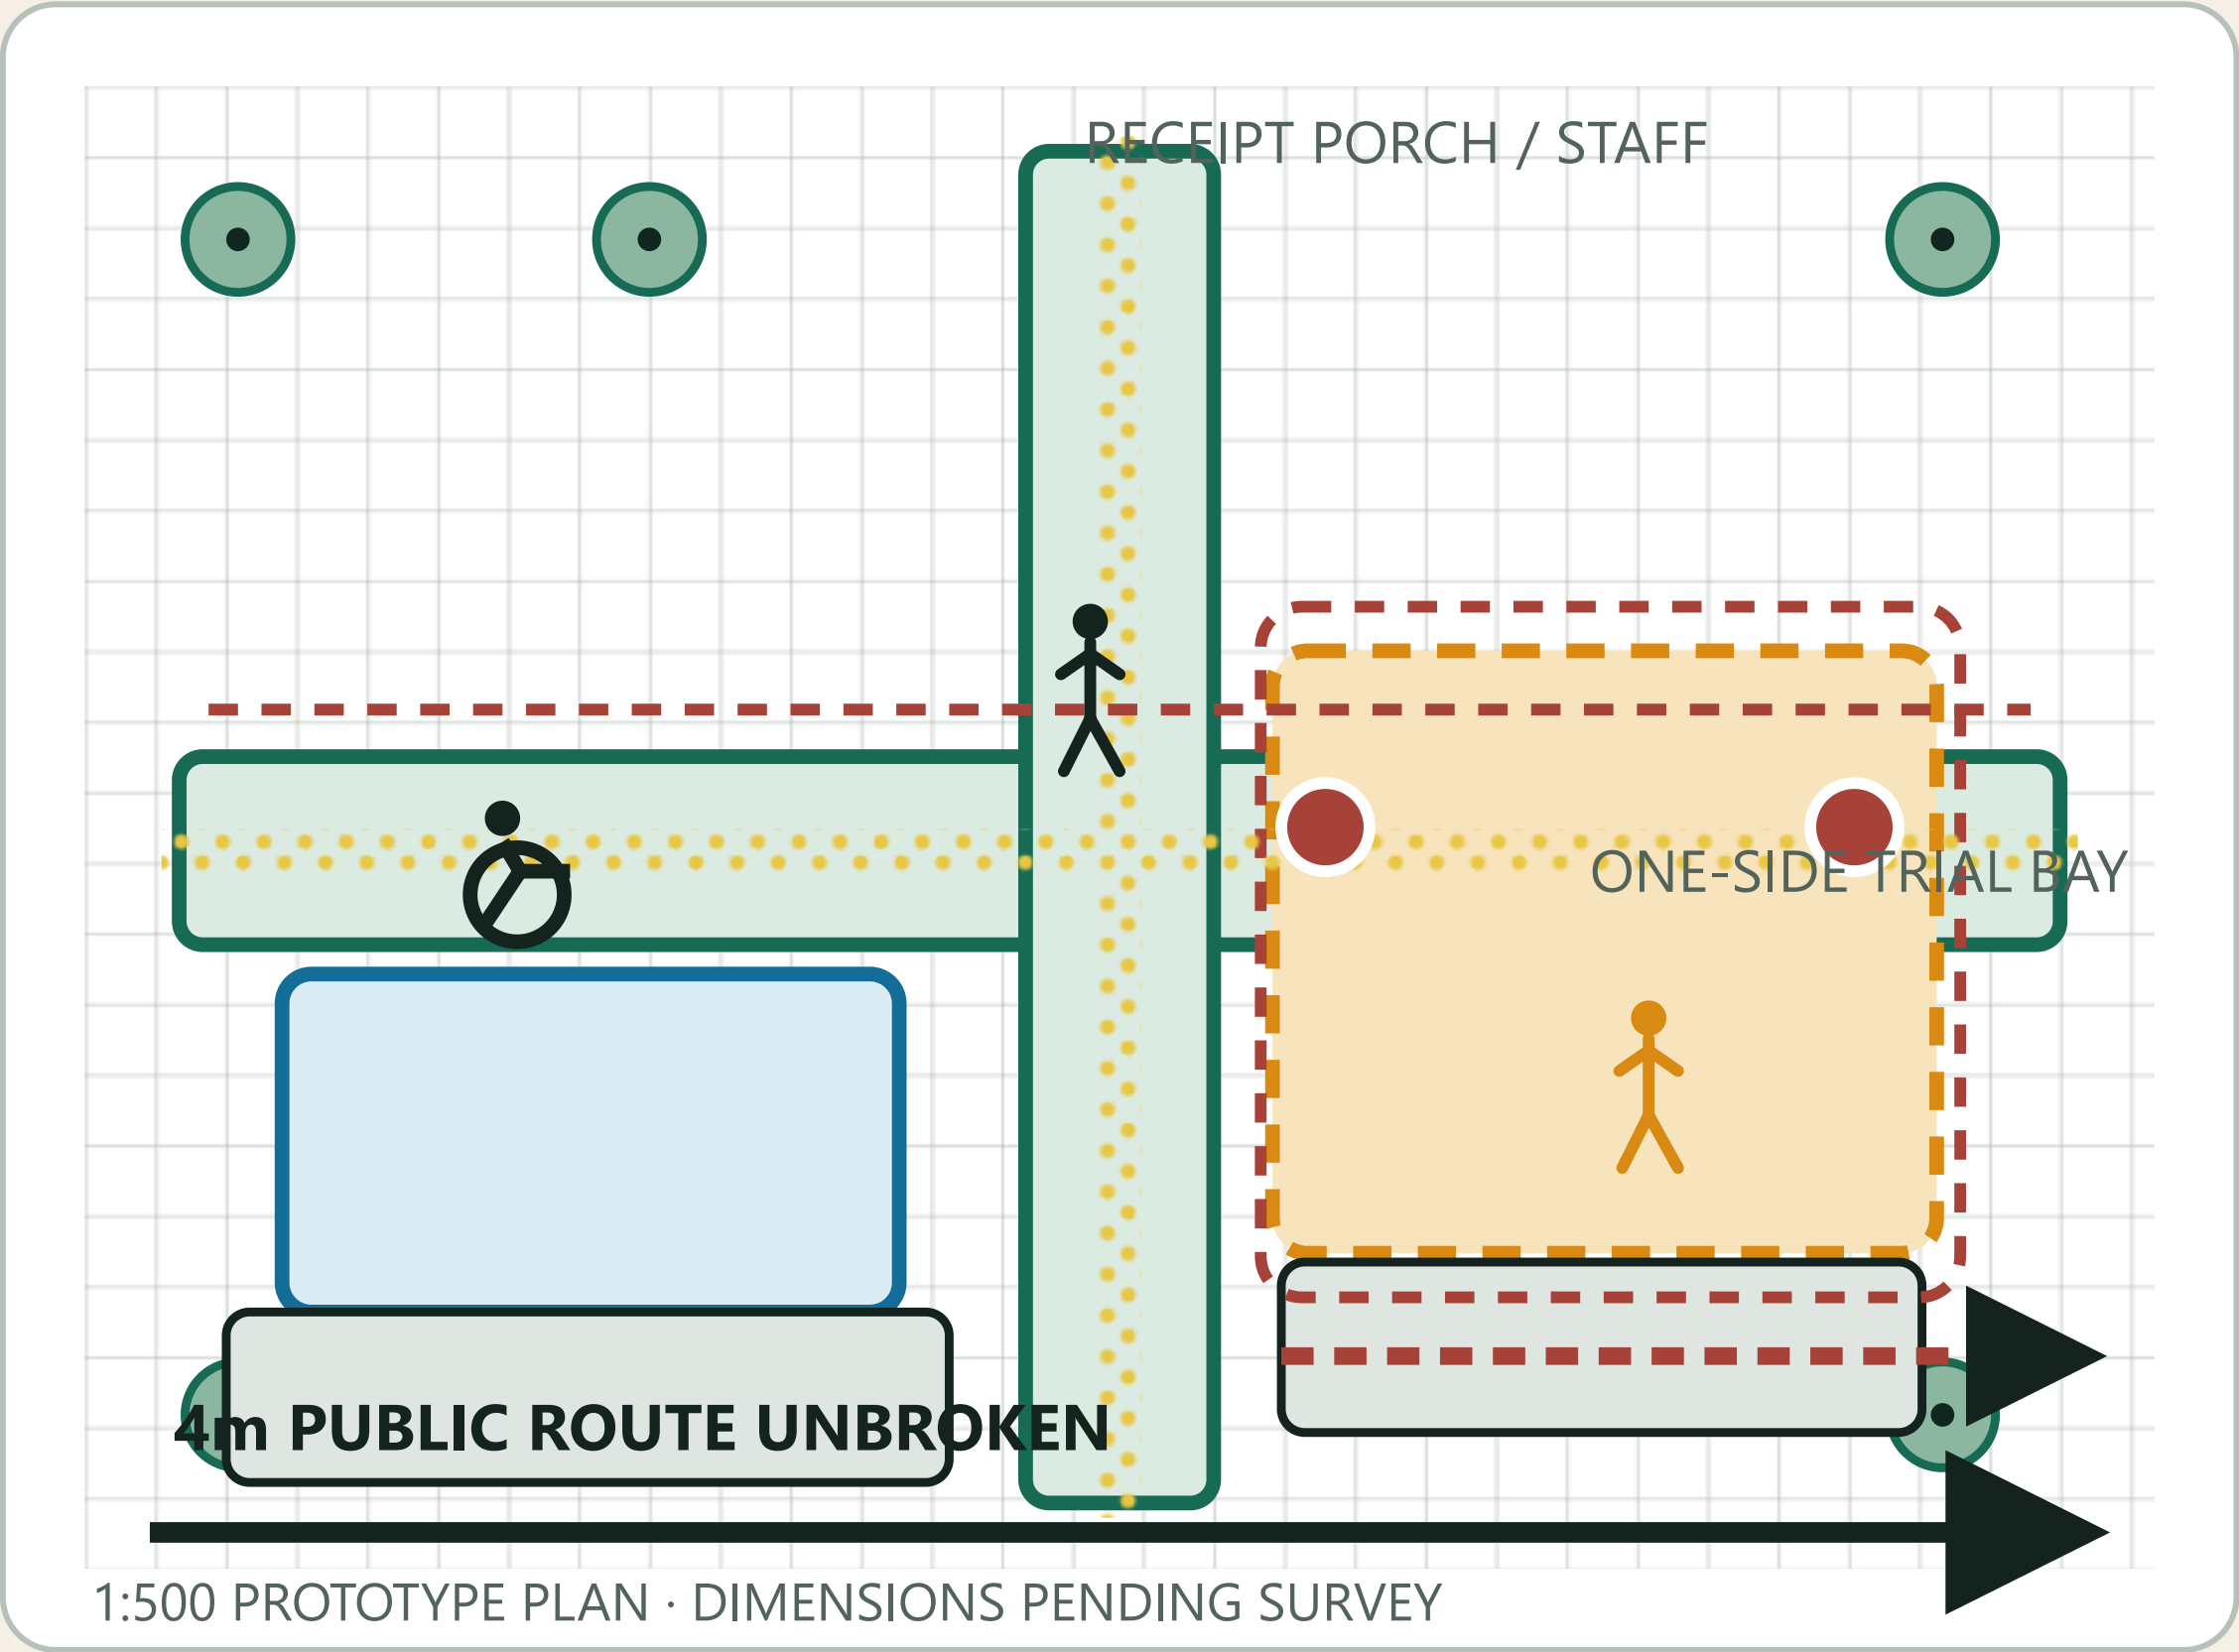

LIVED SECTIONS + REVERSIBLE NODES


ordinary and trial days share the public route

ORDINARY DAY · ROUTE, WAITING + STAFFED SERVICE

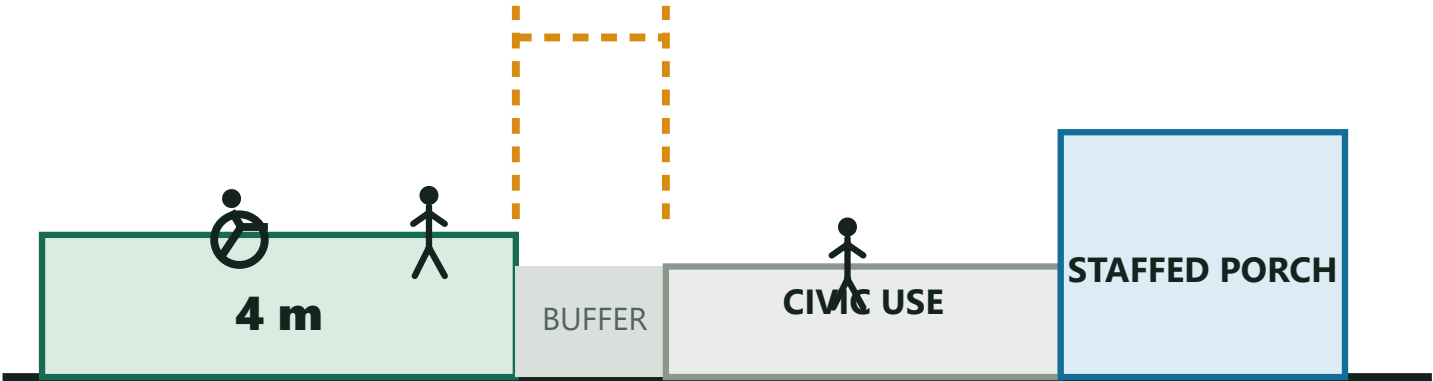


Structure, clearance, drainage, fire and durability are prototype assumptions pending review

TRIAL DAY · PUBLIC-BUFFER-BAY-PORCH

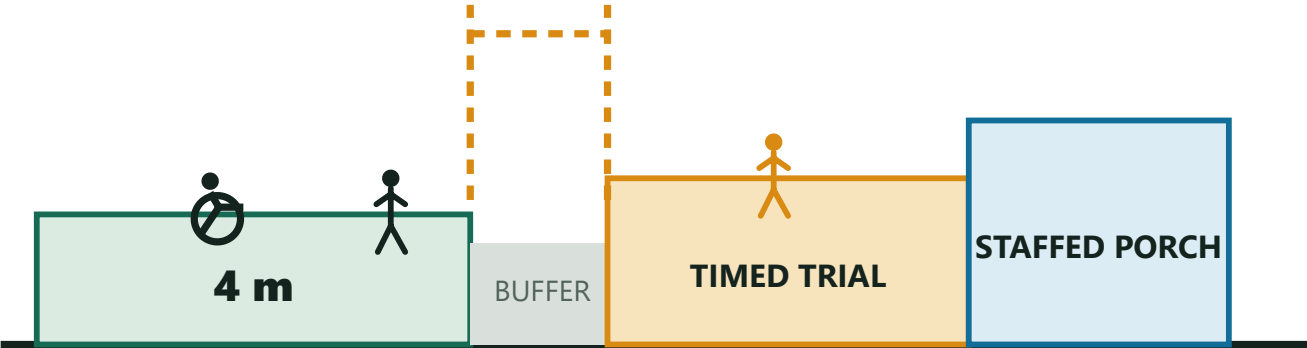

Structure, clearance, drainage, fire and durability are prototype assumptions pending review




1:50 / 1:20 REVERSIBLE NODES · PUBLIC LAYER FIRST

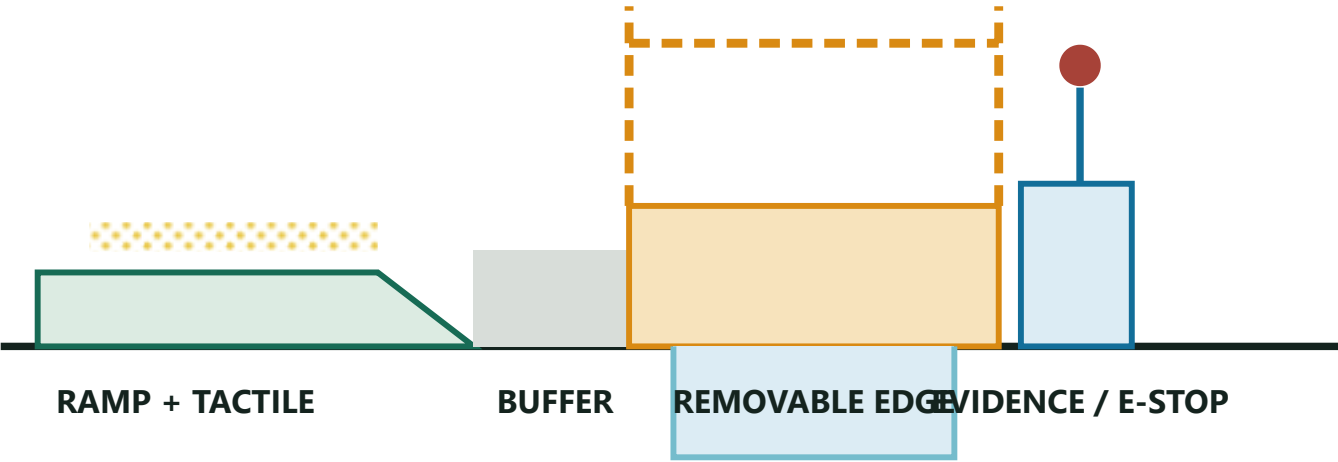

CUTAWAY, DAY/NIGHT + FOUR STATES

same camera, same geometry, different operating states

ONE SPATIAL MODEL · LAYERED CUTAWAY ASSEMBLY

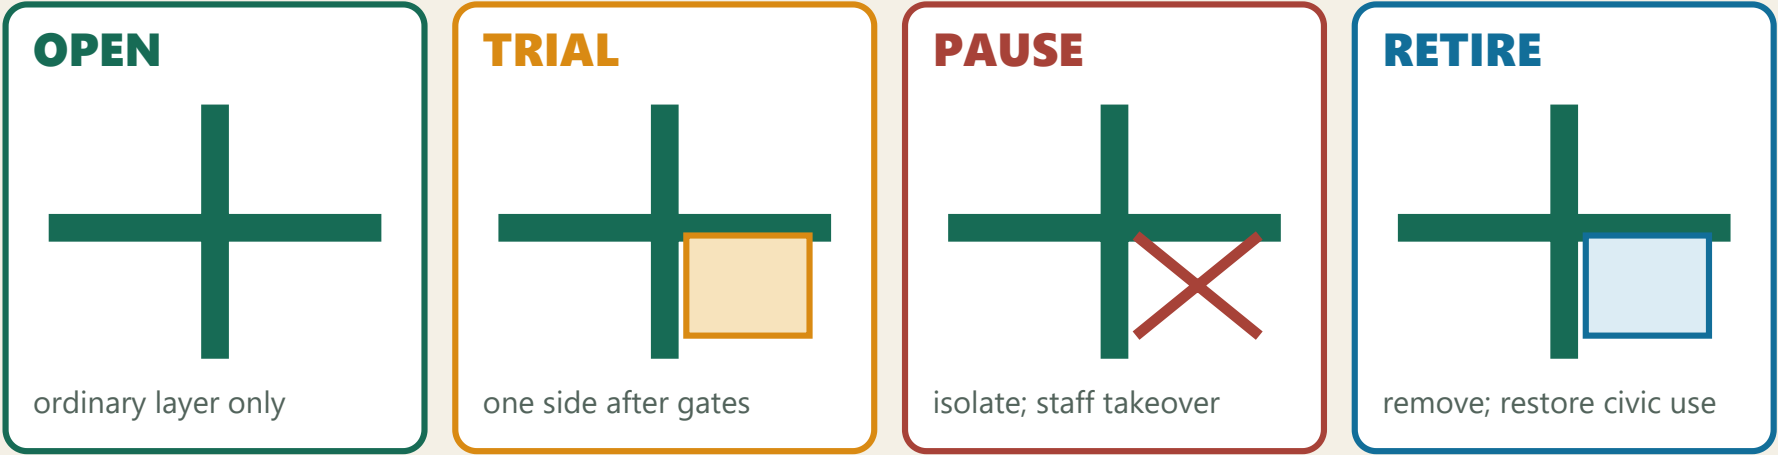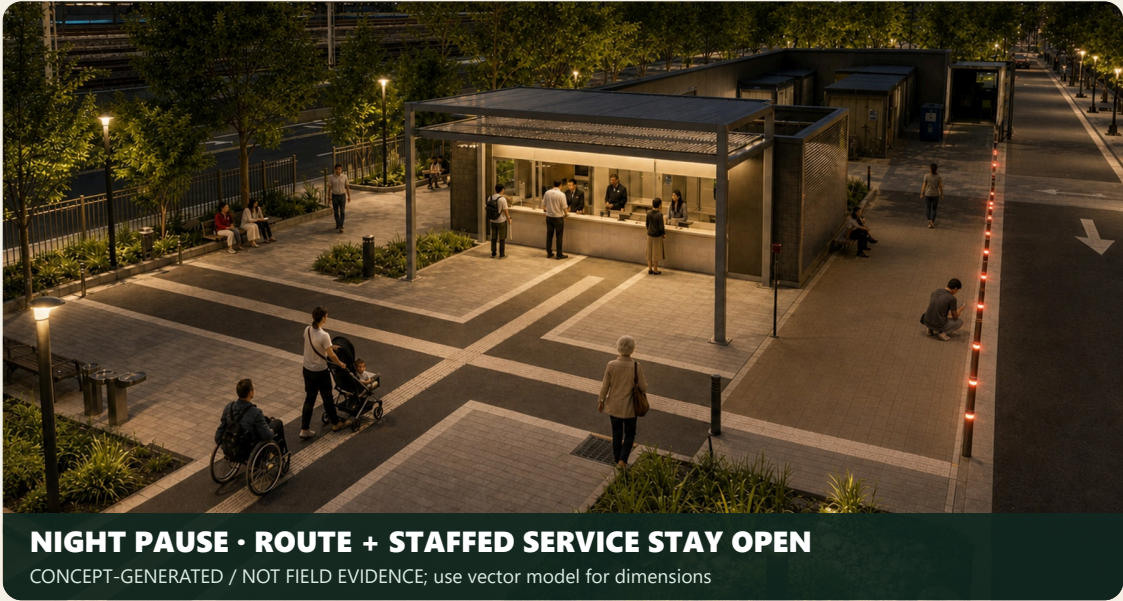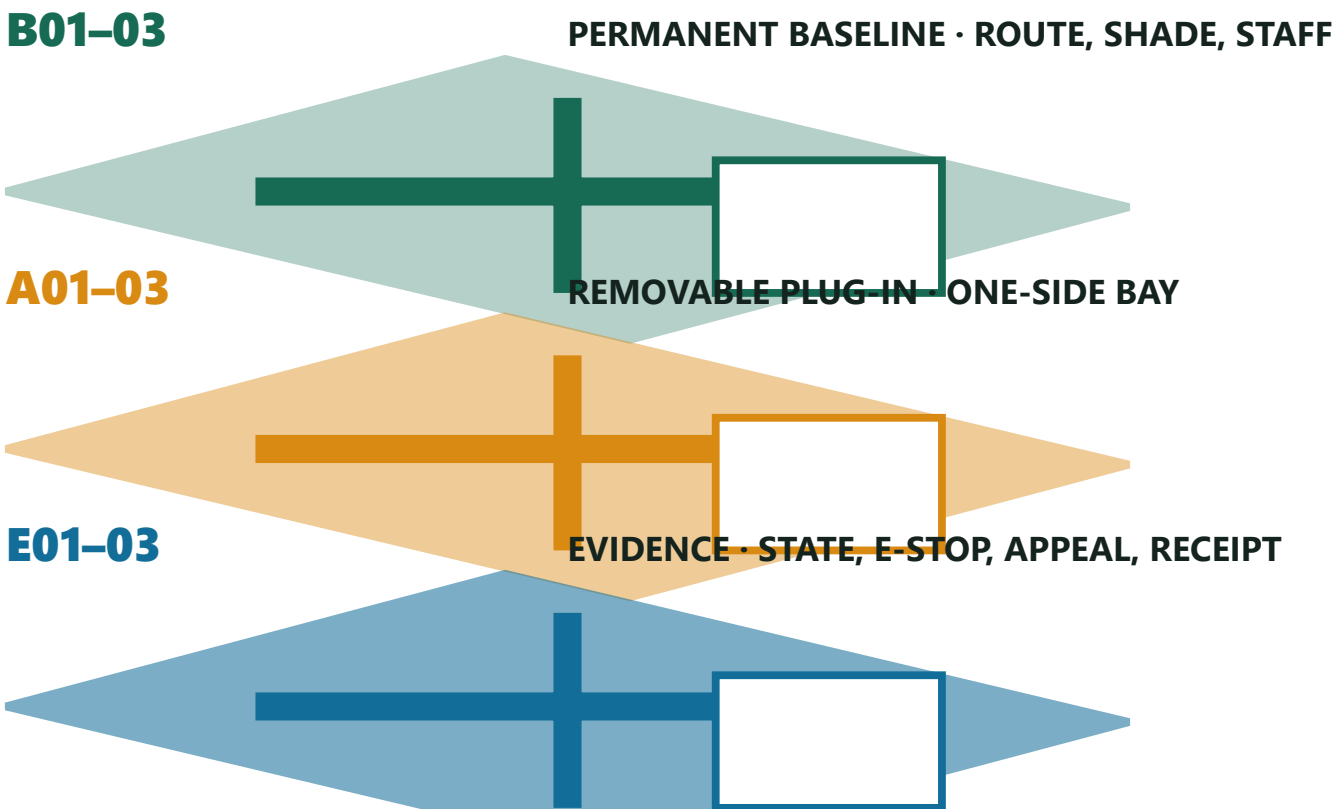

TWELVE SCENES, PERSONAS, EVIDENCE MILE + CIVIC YEAR

one Two-Answers protocol across distinct spatial addresses

TWELVE SCENES + SIX PERSONAS · ONE PROTOCOL, DISTINCT ADDRESSES

T1

Open model and data provenance reproduction

BASELINE FIRST
OWNER + MEASURE + STOP + RESTORE
REFERENCE

T2

Controlled robot–pedestrian–accessibility test

BASELINE FIRST
OWNER + MEASURE + STOP + RESTORE
SUPPORT

T3

Edge compute energy, noise and offline degradation test

BASELINE FIRST
OWNER + MEASURE + STOP + RESTORE
REFERENCE

S1

Staffed enterprise service with optional AI triage

BASELINE FIRST
OWNER + MEASURE + STOP + RESTORE
REFERENCE

S2

International arrival and civic-service navigation

BASELINE FIRST
OWNER + MEASURE + STOP + RESTORE
SUPPORT

S3

Open knowledge matching and community problem workshop

BASELINE FIRST
OWNER + MEASURE + STOP + RESTORE
REFERENCE

S4

Staffed Jing-Zhang heritage tour with optional AI narration

BASELINE FIRST
OWNER + MEASURE + STOP + RESTORE
REFERENCE

S5

Static accessible wayfinding with optional dynamic assistance

BASELINE FIRST
OWNER + MEASURE + STOP + RESTORE
REFERENCE

S6

Shade, rest and extreme-weather service prompts

BASELINE FIRST
OWNER + MEASURE + STOP + RESTORE
REFERENCE

S7

Conventional transit interchange with optional low-speed feeder

BASELINE FIRST
OWNER + MEASURE + STOP + RESTORE
HERO

S8

Staffed public-service desk with optional AI information guide

BASELINE FIRST
OWNER + MEASURE + STOP + RESTORE
REFERENCE

S9

Conventional event operations with aggregate flow assistance

BASELINE FIRST
OWNER + MEASURE + STOP + RESTORE
REFERENCE

PERSONAS · wheelchair / visual impairment / no-phone elder / resident-carer / international team / night staff

EVIDENCE MILE · verified fact → staffed interpretation → optional AI → correction receipt; each civic season archives knowledge.

COMPONENTS, PERMITS, RACI + ORDINARY OPEN DAY

90 days are five gates; failure blocks AI trial

ORDINARY OPEN DAY FIRST · 90 DAYS ARE FIVE ENTRY GATES

DAY 0–15
survey/title/entrance/utility/fire

FAIL → DO NOT ADVANCE

DAY 16–30
build public
route/waiting/shade/staff
only

FAIL → DO NOT ADVANCE

DAY 31–45
record 7 ordinary operating
days

FAIL → DO NOT ADVANCE

DAY 46–75
timed trial after permits +
posts

FAIL → DO NOT ADVANCE

DAY 76–90
stop drill/removal/public
receipt

FAIL → DO NOT ADVANCE

COMPONENT–PERMIT–MAINTENANCE LINKS TO DRAW

B01–03

route/shade/staff
daily; retain

A01–03

bay/cabinet/terminal
before trial; remove

E01–03

state/e-stop/receipt
open/close review; retain panel

MAT-01–05

dry frame/screen/base/paving/panel
specialist review; reversible

RESPONSIBILITY + NEXT GATE

01

VENUE LEAD

PENDING

02

BASELINE SERVICE

PENDING

03

SAFETY LEAD

PENDING

04

DATA RECORDER

PENDING

CURRENT GO · SURVEY + PERMIT PREP
PENDING_MARKET_QUOTE · NOT BUILT · NOT FIELD-RUN

Prices remain formulas only; failed permit, post, baseline or removal drill blocks AI trial.

METRICS, RECEIPT, RISK + NEXT GATE

known design, field unknown and human decision stay separate

EVIDENCE DESK · DESIGN CHOICE → PREPARATION → FIELD MEASUREMENT

Unknowns stay blank; G0 is the next step, not the hero

01

DESIGN CHOICE

ALT-A / REJECT

cuts public cross; fire/removal conflict

ALT-B / REVISE

routes stay; supervision/removal fragment

ALT-C / ADVANCE

one-side bay; 4 m route across four states

GEOMETRY AUDIT

21 hard gates; computation is not field performance

02

IMPLEMENTATION PREP

CURRENT G0

enter survey and permit preparation

EIGHT PERMITS

site/fire/access/power/network/traffic/equipment

FOUR POSTS

venue, baseline, safety, data

90-DAY FIVE GATES

failure returns to ordinary opening

03

FIELD MEASUREMENT

12 CONTRACTS

denominator, sample, owner, stop, recovery defined

FIELD RESULTS

0; footfall, safety, efficiency, energy unknown

BLANK RECEIPT

human committee fills adopt / revise / stop

EXIT + RESTORE

clock defined; duration awaits drill

Synthetic checks test rule consistency only; published facts, design assumptions and field unknowns remain separate.