


京张年轮 · 总体城市设计

9.7 km 技术史轴 + 6.2 km 生态轴，中间夹住八大学院与中关村

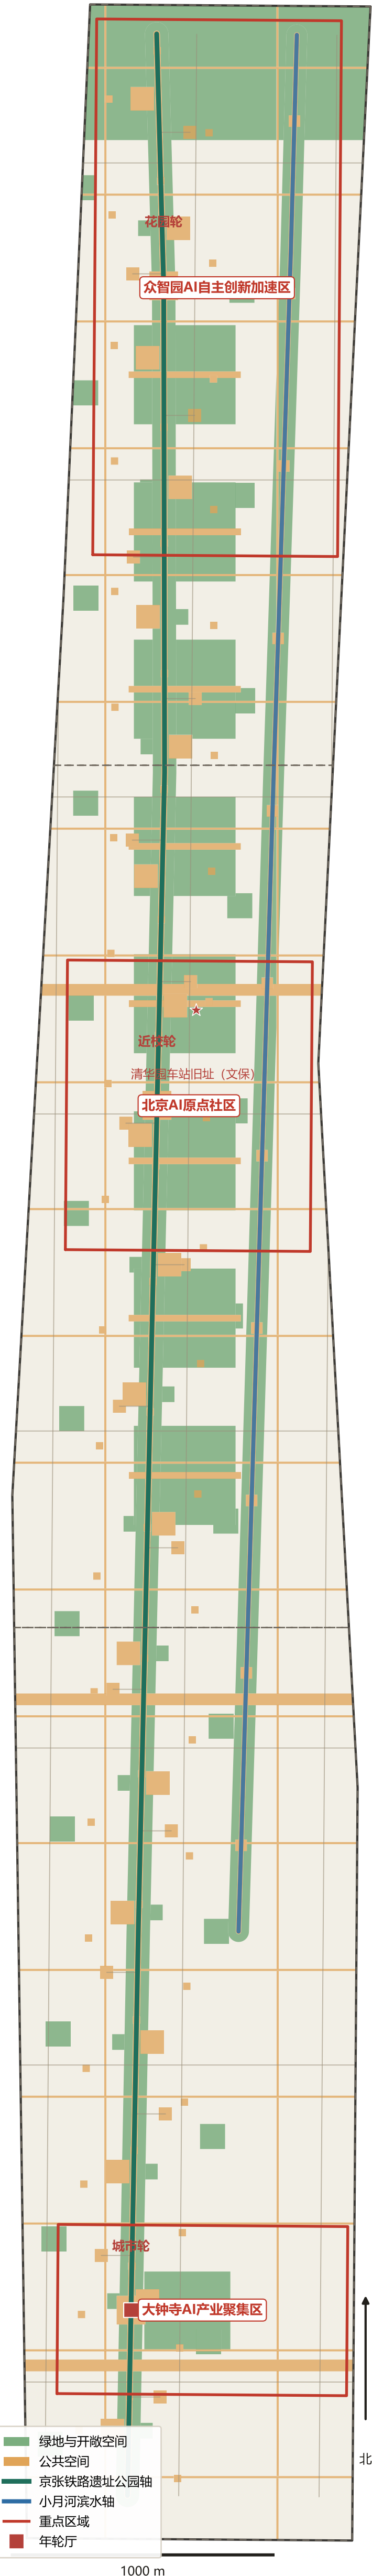

① 慢行网络

绿道总长	40.3 km
绿道条数	22
里院广场	19
接驳 / 滨水驿站	17 / 11
道路中心线	50

② 文保避让


★ 清华园车站旧址（文保）	保护范围与Ⅰ类建控地带按保守外包表达；新增体量与建控地带的最小净距 12.2 m，控制地带内新建檐口限高 9 m。
---------------	---

③ 测试道路分级

开放	限制	禁入
允许低速配送与接驳测试	限时段、限速度、需人工复核	涉密院所、部队、校园红线内不测试

京张年轮 · 用地结构与指标复算

用地为对场地边界的严格剖分：无缝隙、无重叠、面积可复算

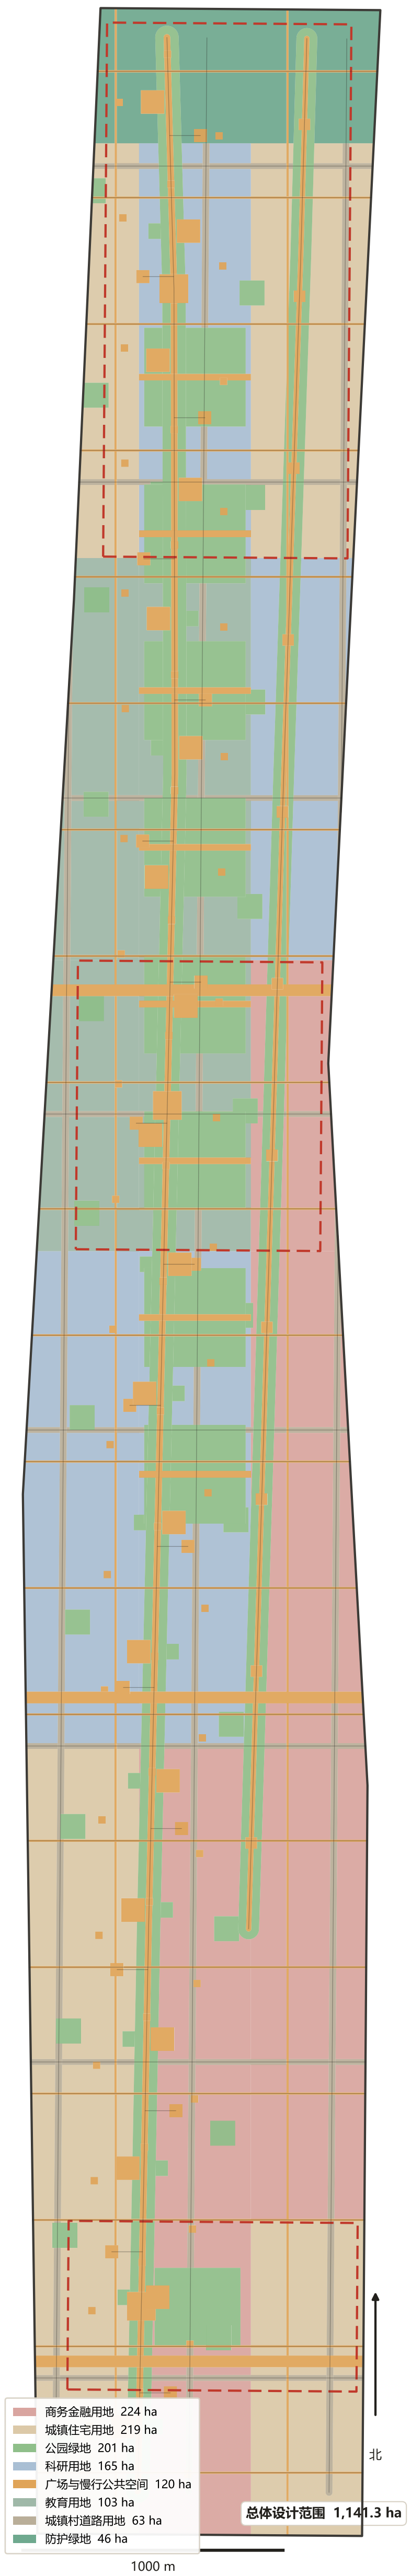

A · 提交几何复算值

A · 提交几何复算值

site_area	1,141,825.386	sqm	官方 provisional 边界 · EPSG:4548
green_space	2,463,201.830	sqm	green_space.geojson 并集
public_space	1,203,476.584	sqm	public_space.geojson 并集
building_footprint	15,155,200.6	sqm	37 处新增概念体量
green_ratio	0.2158	ratio	绿地/场地，非法定指标
public_space_ratio	0.1054	ratio	公共空间/场地

C · 未知项：如实留白，不编造

- floor_area_ratio — 控规缺失，现状建筑底数缺失
- 建筑高度 / 密度 / 退线 / 拆改留 / 投资测算 — 一律概念建议
- 官方 polygon 发布后，全部面积与比例须重算

B · 证据链：每个数字都能追到文件

geometry/site_boundary.geojson SITEb001/site-package/geometry/pro
geometry/green_space.geojson 461 feats EPSG:4548 U area
geometry/public_space.geojson 141 feats EPSG:4548 U area
geometry/buildings.geojson 37 feats EPSG:4548 U area
geometry/land_use.geojson 223 feats 严格剖分：无缝隙 / 无重叠
metrics.json status=known scripts/spatial_review.py 同管线复

