


The Jingzhang Rings: One Ring, Two Curves

Centennial Jingzhang AI Belt open design call · conceptual proposal


site_area_sqm	green_ratio	public_space_ratio	building_footprint_area_sqm
11,412,825	0.216	0.105	15,855
sqm	ratio	ratio	sqm

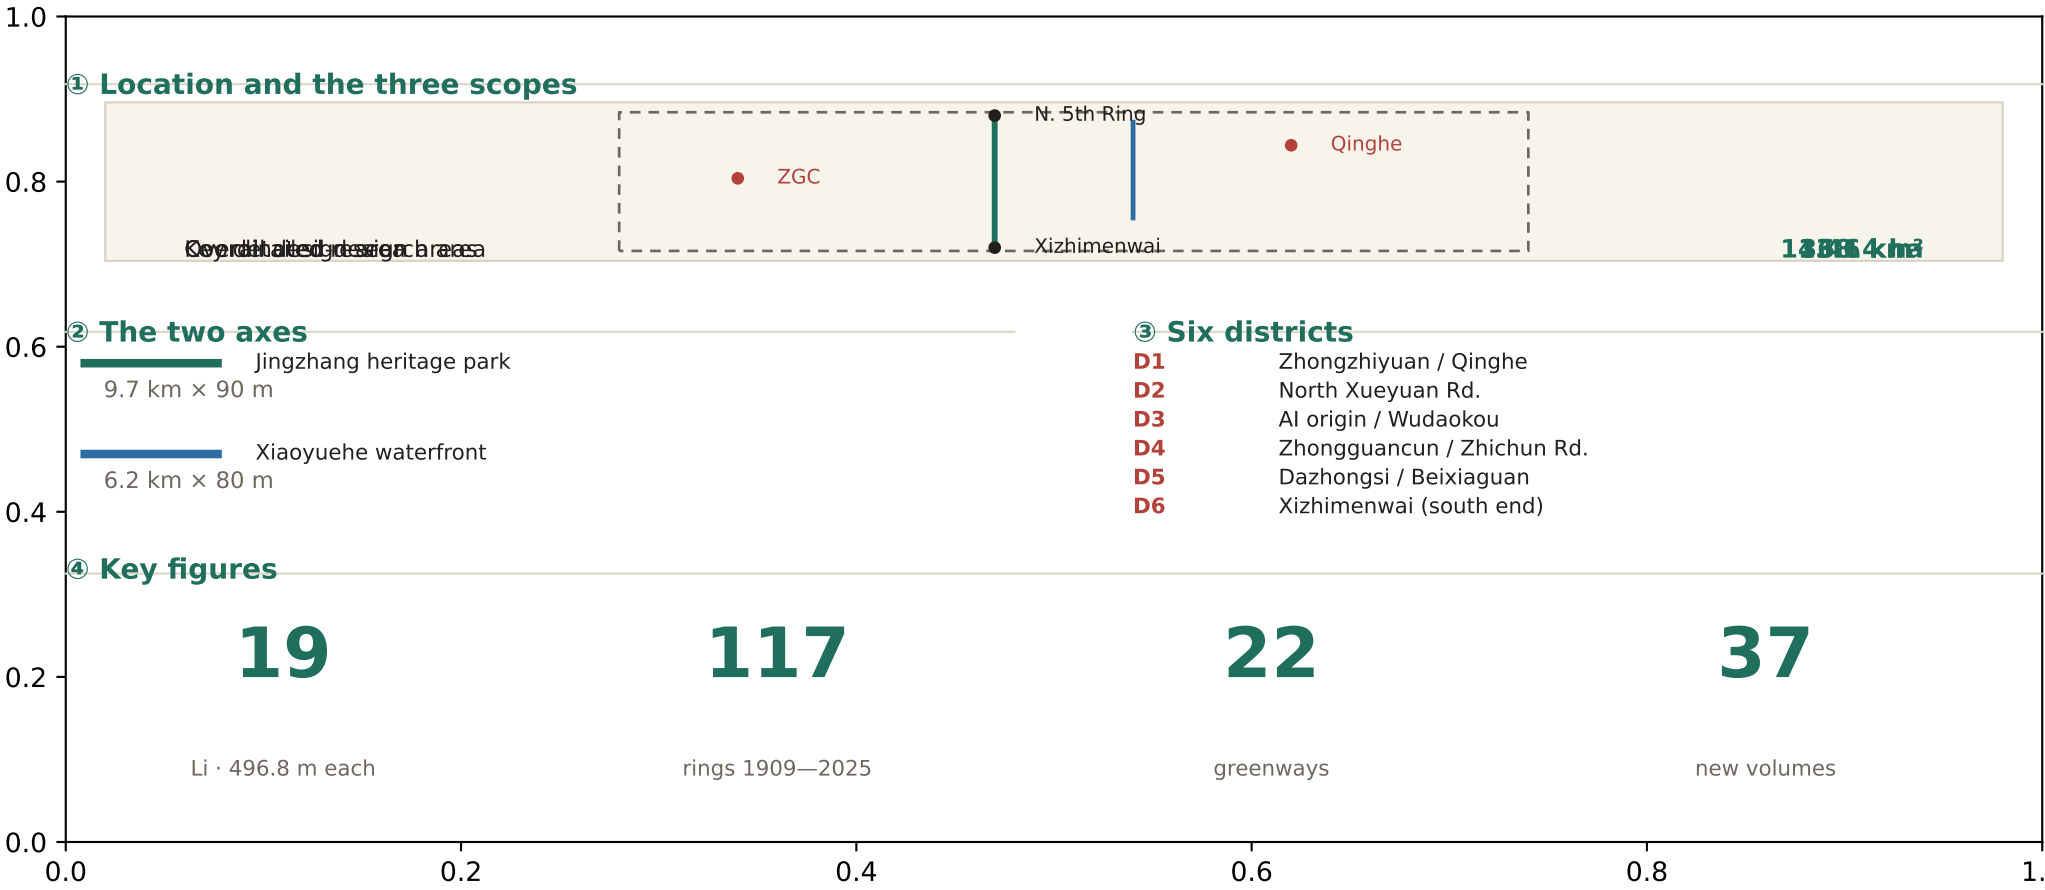


Conceptual explanatory layer. Site boundary and the three key areas use the official provisional geometry; not a redline or approval basis.

01 Site overview: a city held between two axes

A 9.7 km technology-history axis and a 6.2 km ecological axis hold the Eight Great Colleges and Zhongguancun between them

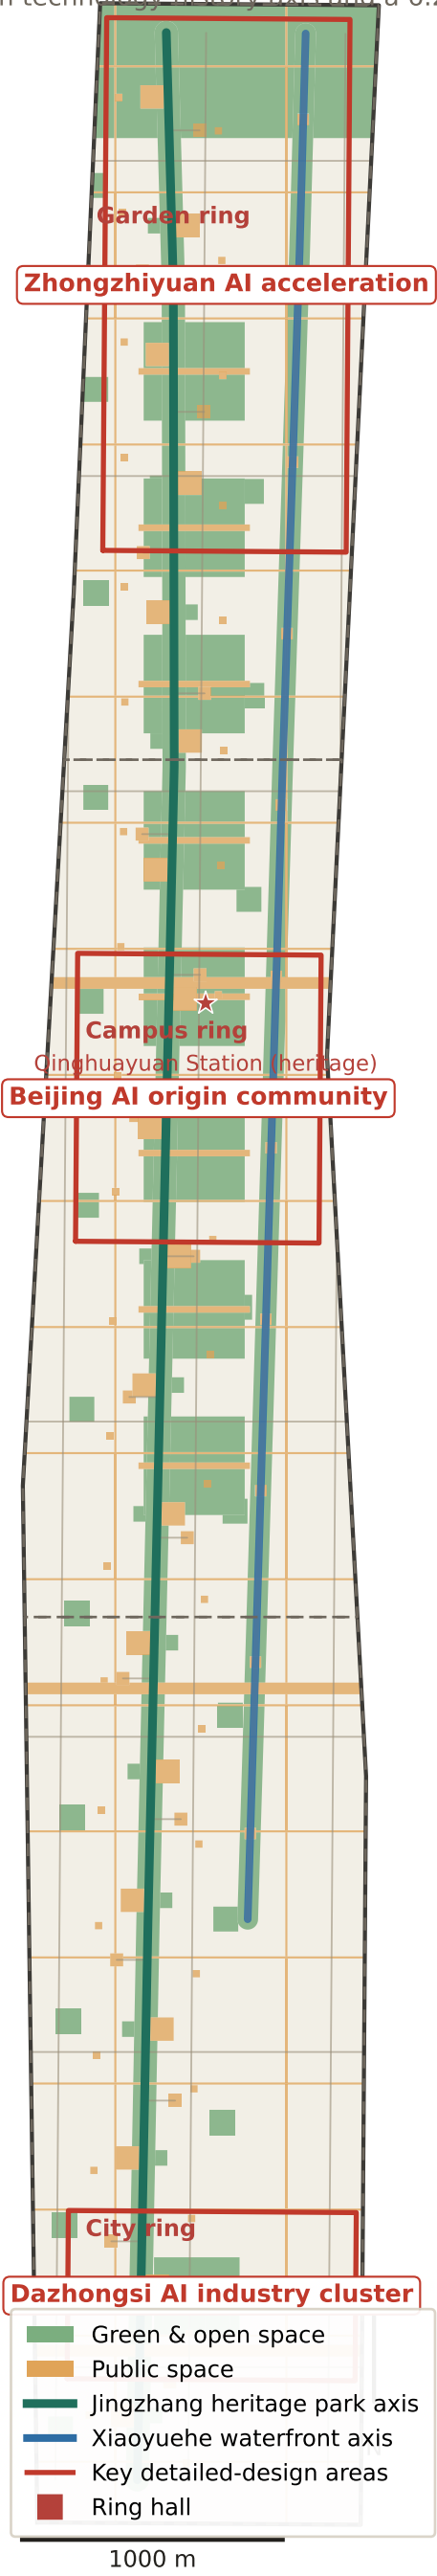

① Location and the three scopes

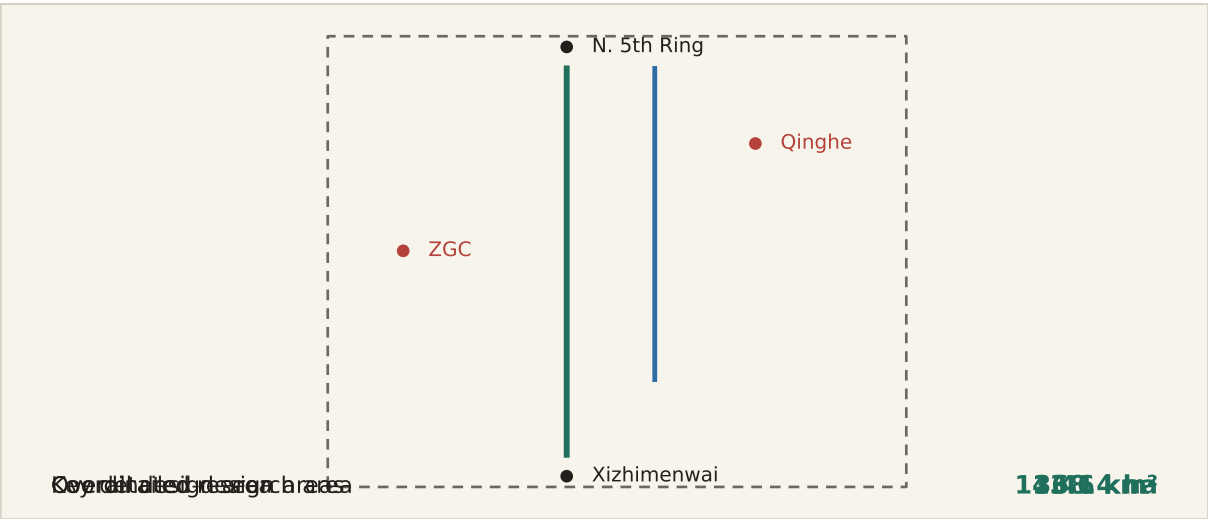

② The two axes

Jingzhang heritage park

9.7 km × 90 m

Xiaoyuehe waterfront

6.2 km × 80 m

③ Six districts


- D1 Zhongzhiyuan / Qinghe
- D2 North Xueyuan Rd.
- D3 AI origin / Wudaokou
- D4 Zhongguancun / Zhichun Rd.
- D5 Dazhongsi / Beixiaguan
- D6 Xizhimenwai (south end)

④ Key figures

19	117	22	37
Li · 496.8 m each	rings 1909—2025	greenways	new volumes

02 Land-use structure

Land use is a strict partition of the site: no gaps, no overlaps, areas recomputable

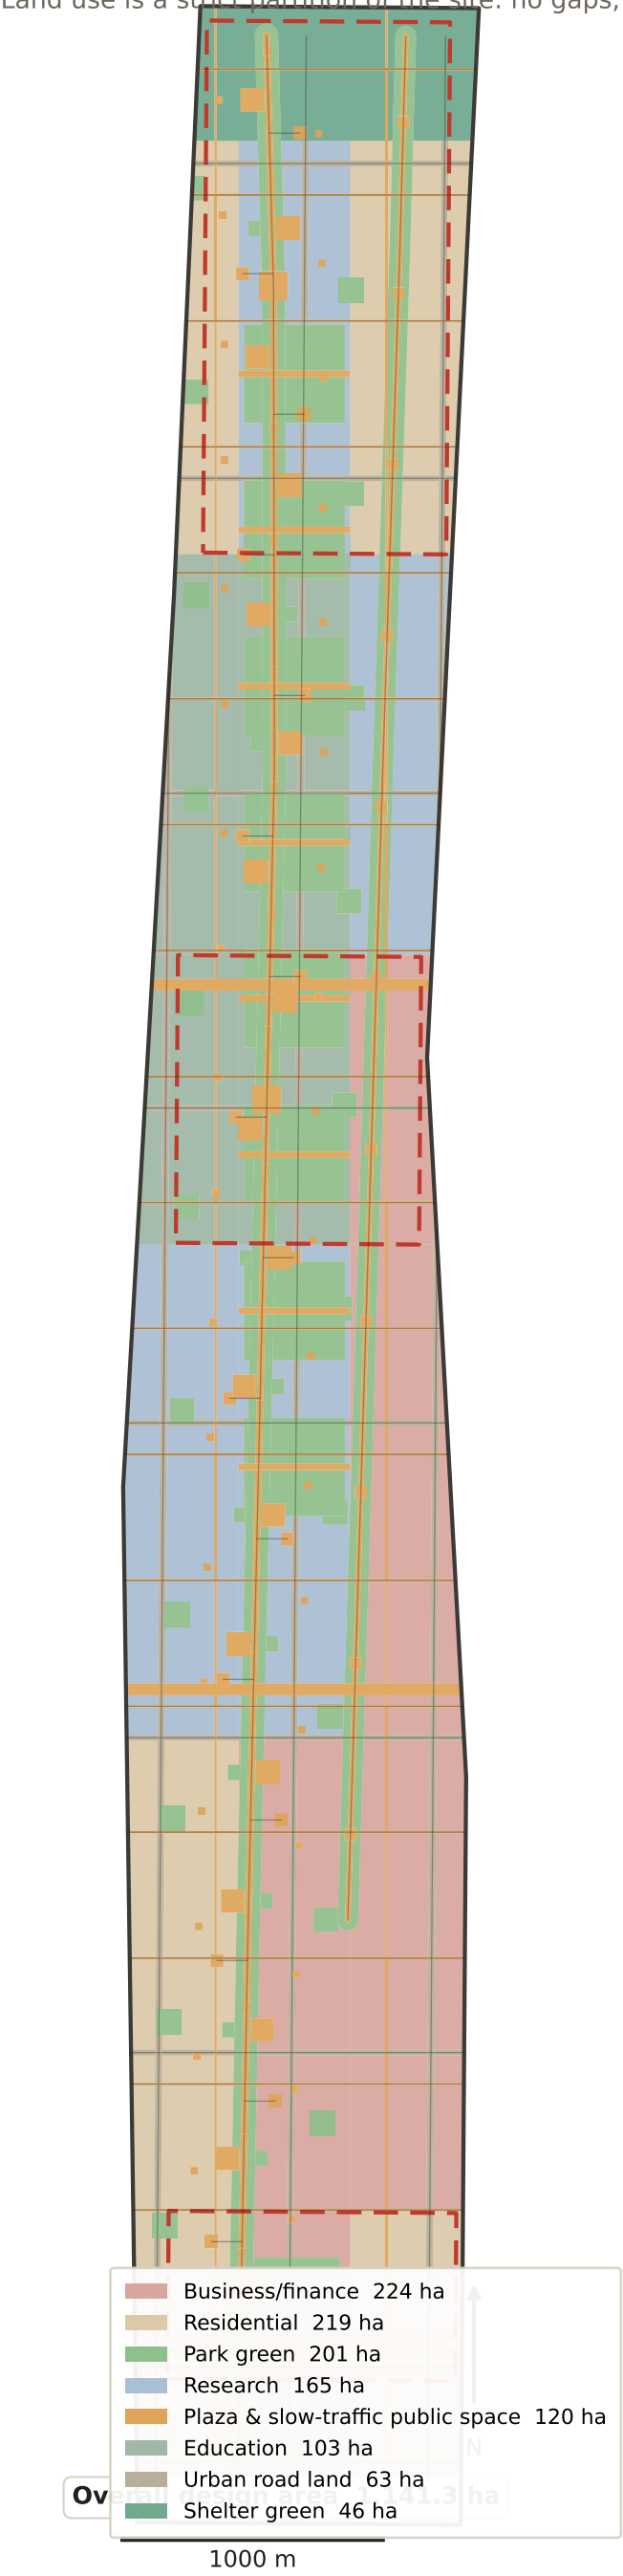

① Land-use composition



Project subset of the national land-use classification


② Codes and areas

0902	Business/finance	223.8 ha
0701	Residential	219.4 ha
1401	Park green	200.8 ha
0802	Research	164.7 ha
1403	Plaza & slow-traffic public space	120.3 ha
0804	Education	103.4 ha
1207	Urban road land	63.4 ha
1402	Shelter green	45.5 ha

Total = site area 1,141.3 ha: a strict partition, no gaps, no overlaps.

03 The three key areas

Each of the three areas matches one ring-hall archetype

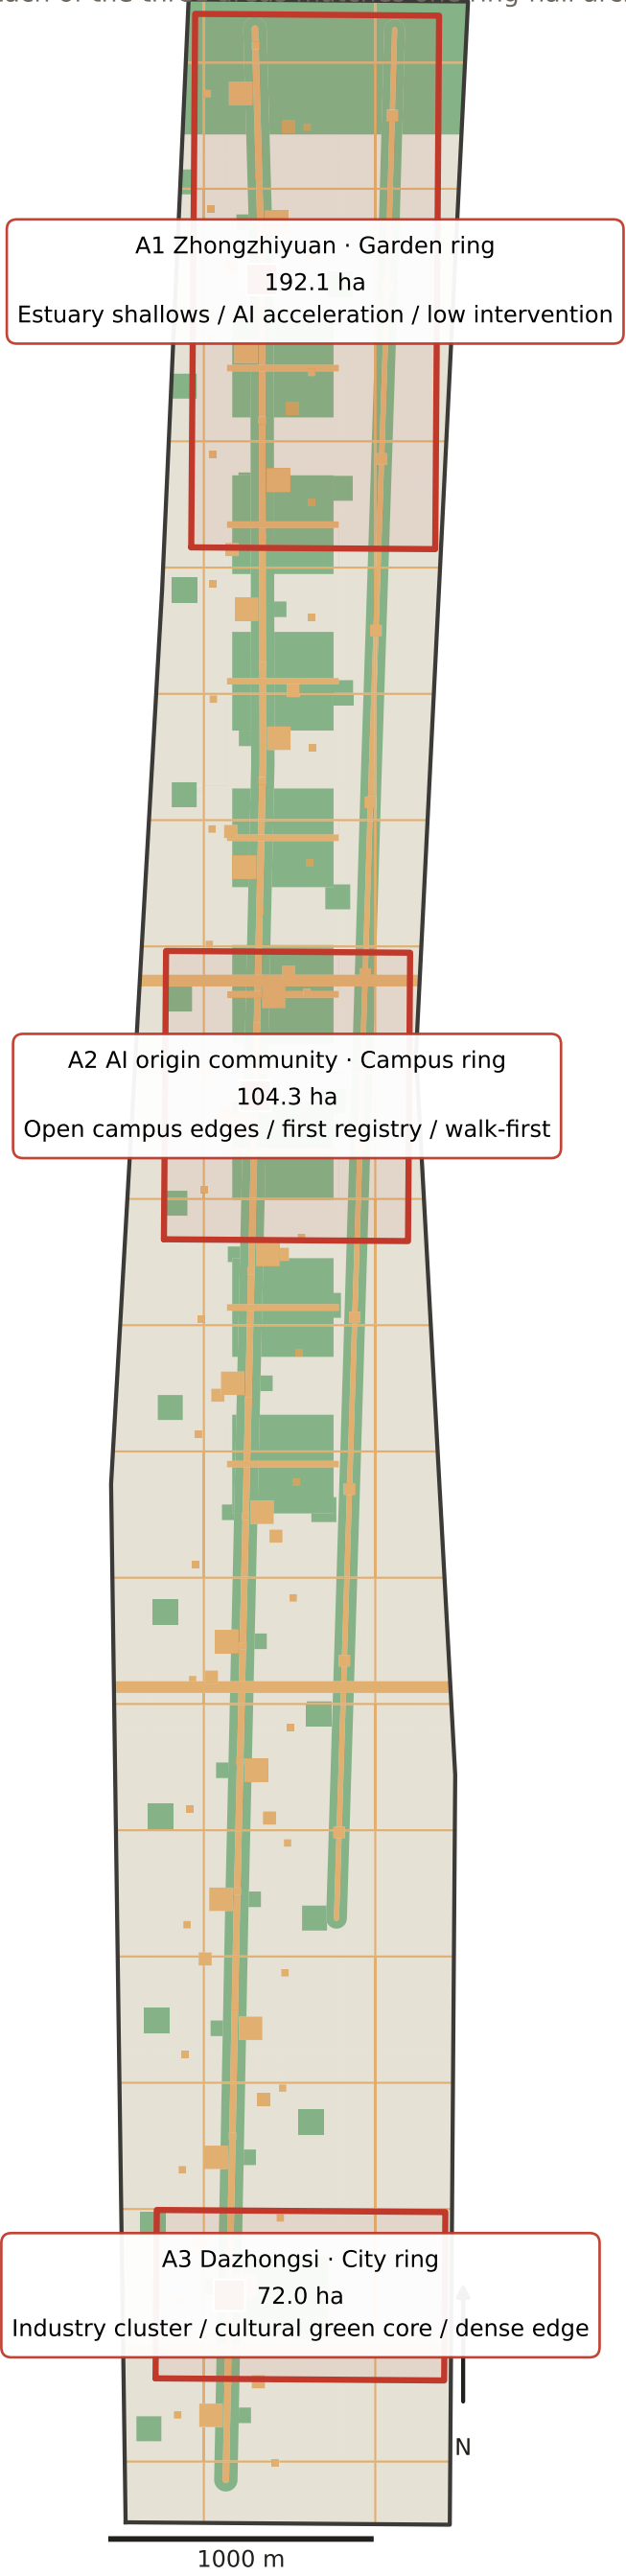

A1

Zhongzhiyuan · Garden ring

192.1 ha

- Estuary shallow-wetland buffer
- Additive only, nothing removed

A2

AI origin · Campus ring

104.3 ha

- Campus edges opened 25 m to the city
- First scenario registry: trial, reversible

A3

Dazhongsi · City ring


72.0 ha

Each area maps to one ring hall

- Dense urban edge for industry cluster
- The three key areas use the official provisional geometry; areas follow the announced 192.1 / 104.3 / 72.0 ha. No redline or precise-area claim is made.
- Dazhongsi cultural green core
- Transit interchange layered with public space

04 Slow traffic and blue-green system

22 greenways plus two axis promenades stitch across the rail and river cuts

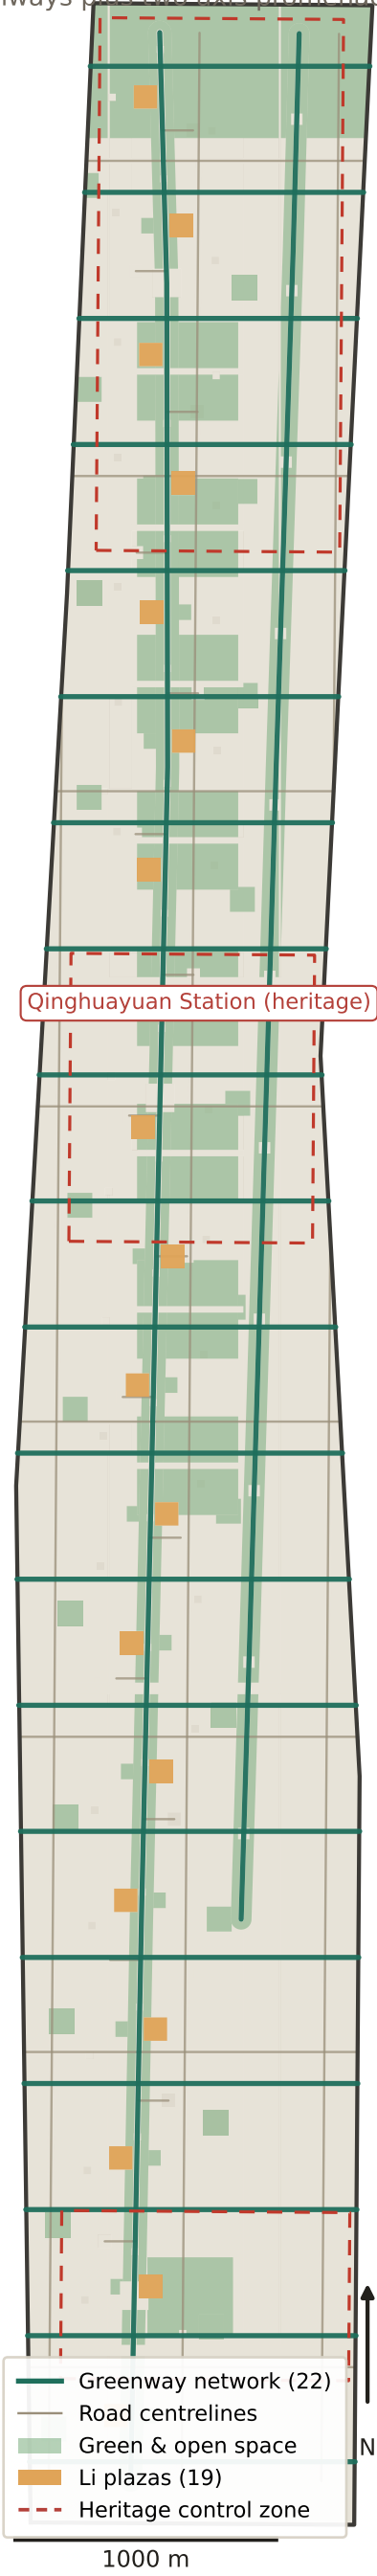

① Slow-traffic network

Greenway length	40.3 km
Greenway count	22
Li plazas	19
Interchange / waterfront	17 / 11
Road centrelines	50

② Heritage clearance

★ Qinghuayuan Station (heritage)

Protection and class-I control zones drawn as conservative envelopes; minimum clearance from new volumes is 12.2 m, and new eaves inside the control zone stay under 9 m.

③ Test-road grading

Open	Restricted	Closed
------	------------	--------

Low-speed delivery and interchange trials allowed, speed-limited, human review required inside secured or campus redlines


A · Recomputed from submitted geometry

A · Recomputed from submitted geometry

site_area_sqm	11,412,825.386	sqm	Official provisional boundary · EPSG:4548
green_space_area_sqm	2,463,013.830	sqm	union of green_space.geojson
public_space_area_sqm	1,203,476.584	sqm	union of public_space.geojson
building_footprint_area_sqm	15,855.006	sqm	37 new conceptual volumes
green_ratio	0.2158	ratio	green/site, not a statutory figure
public_space_ratio	0.1054	ratio	public space/site

B · Evidence chain: every number traces to a file

geometry/site_boundary.geojson	PROV-SITE-001	brief/site-package/geometry/provisional_boundaries.geojson
geometry/green_space.geojson	49 feats	EPSG:4548 u area
geometry/public_space.geojson	145 feats	EPSG:4548 u area

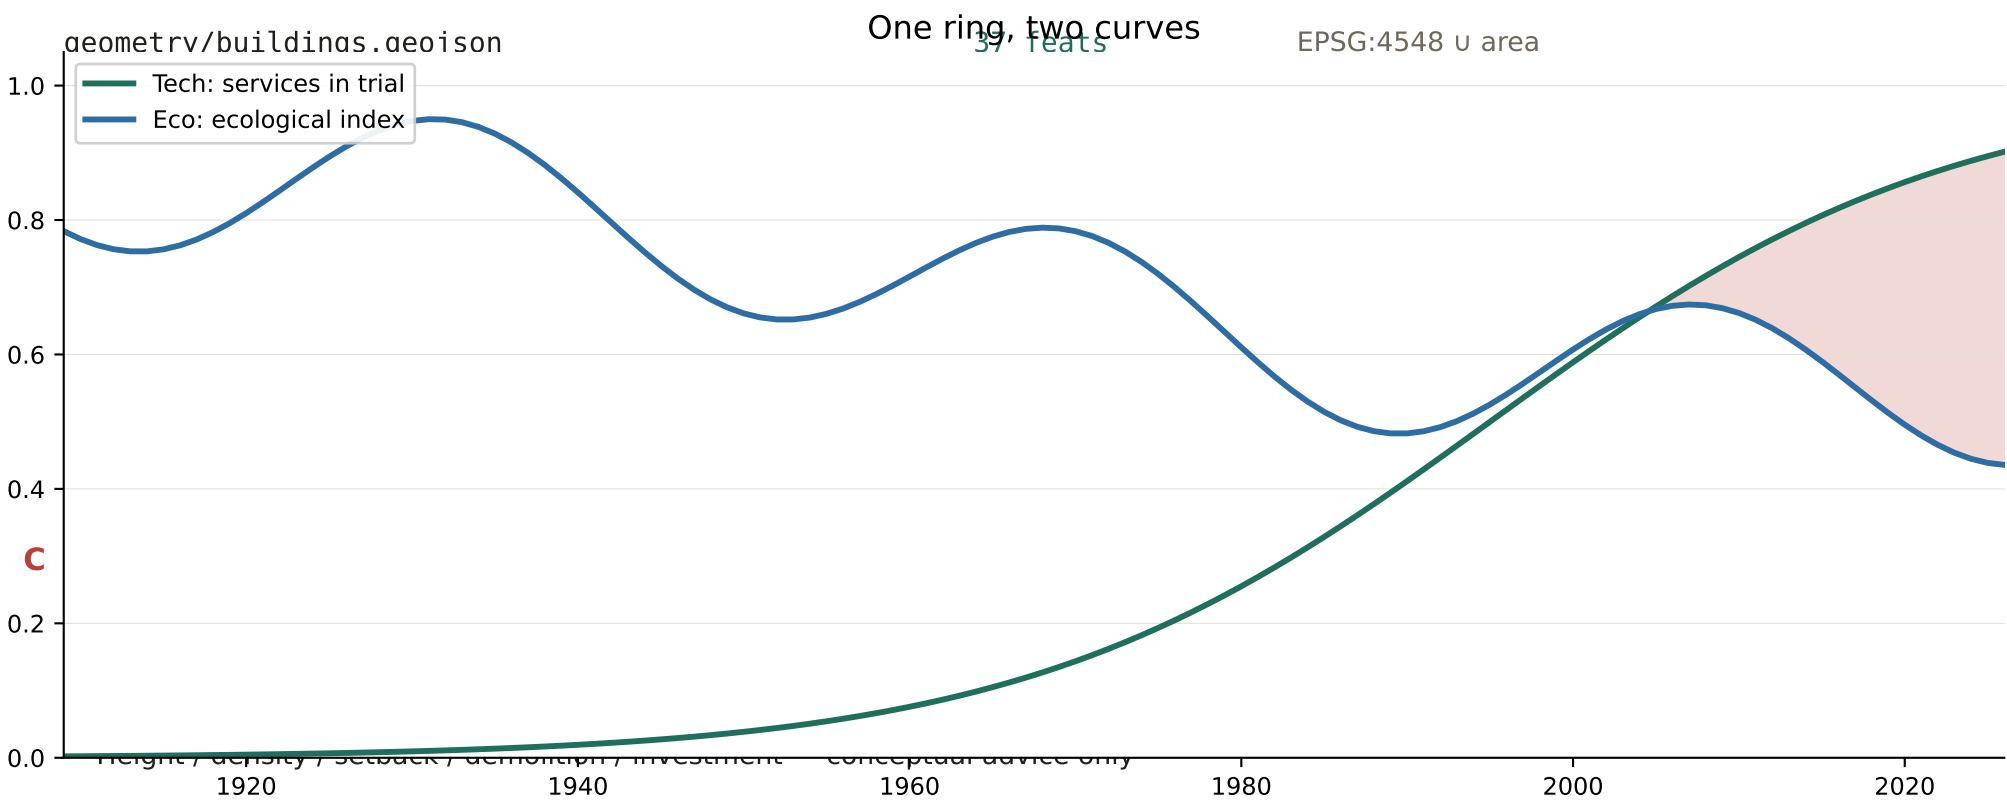

What this proposal gives up

01 Give up full continuity

Sections inside secured institutes, military and some campus redlines stay closed; gaps are met with detours and interface treatment.

02 Give up full automation

Keep breakfast vendors, repairers, guards, cleaners and station keepers, and never count their jobs as efficiency gains.

03 Give up city-wide realtime sensing

Deploy only outside no-go zones; data never leaves the campus or community server.

04 Give up regulatory conclusions

FAR, height, density, green ratio, setback, demolition, road alignment and investment stay conceptual only.

05 Give up one-shot delivery

Three phases over ten years; only the feasible gets built first, and rights-of-way blocks may stall.

06 Give up the very phrase “optimise the street”

Trial first, reversible, resident-decided: time-boxed (12 months), exitable, A/B compared, results public.