

京张年轮：一圈年轮，两条曲线

百年京张 AI 创新带城市设计开源征集 · 概念方案

site_area_sqm

11,412,825

sqm

green_ratio

0.216

ratio

public_space_ratio


0.105

ratio

building_footprint_area_sqm

15,855


sqm

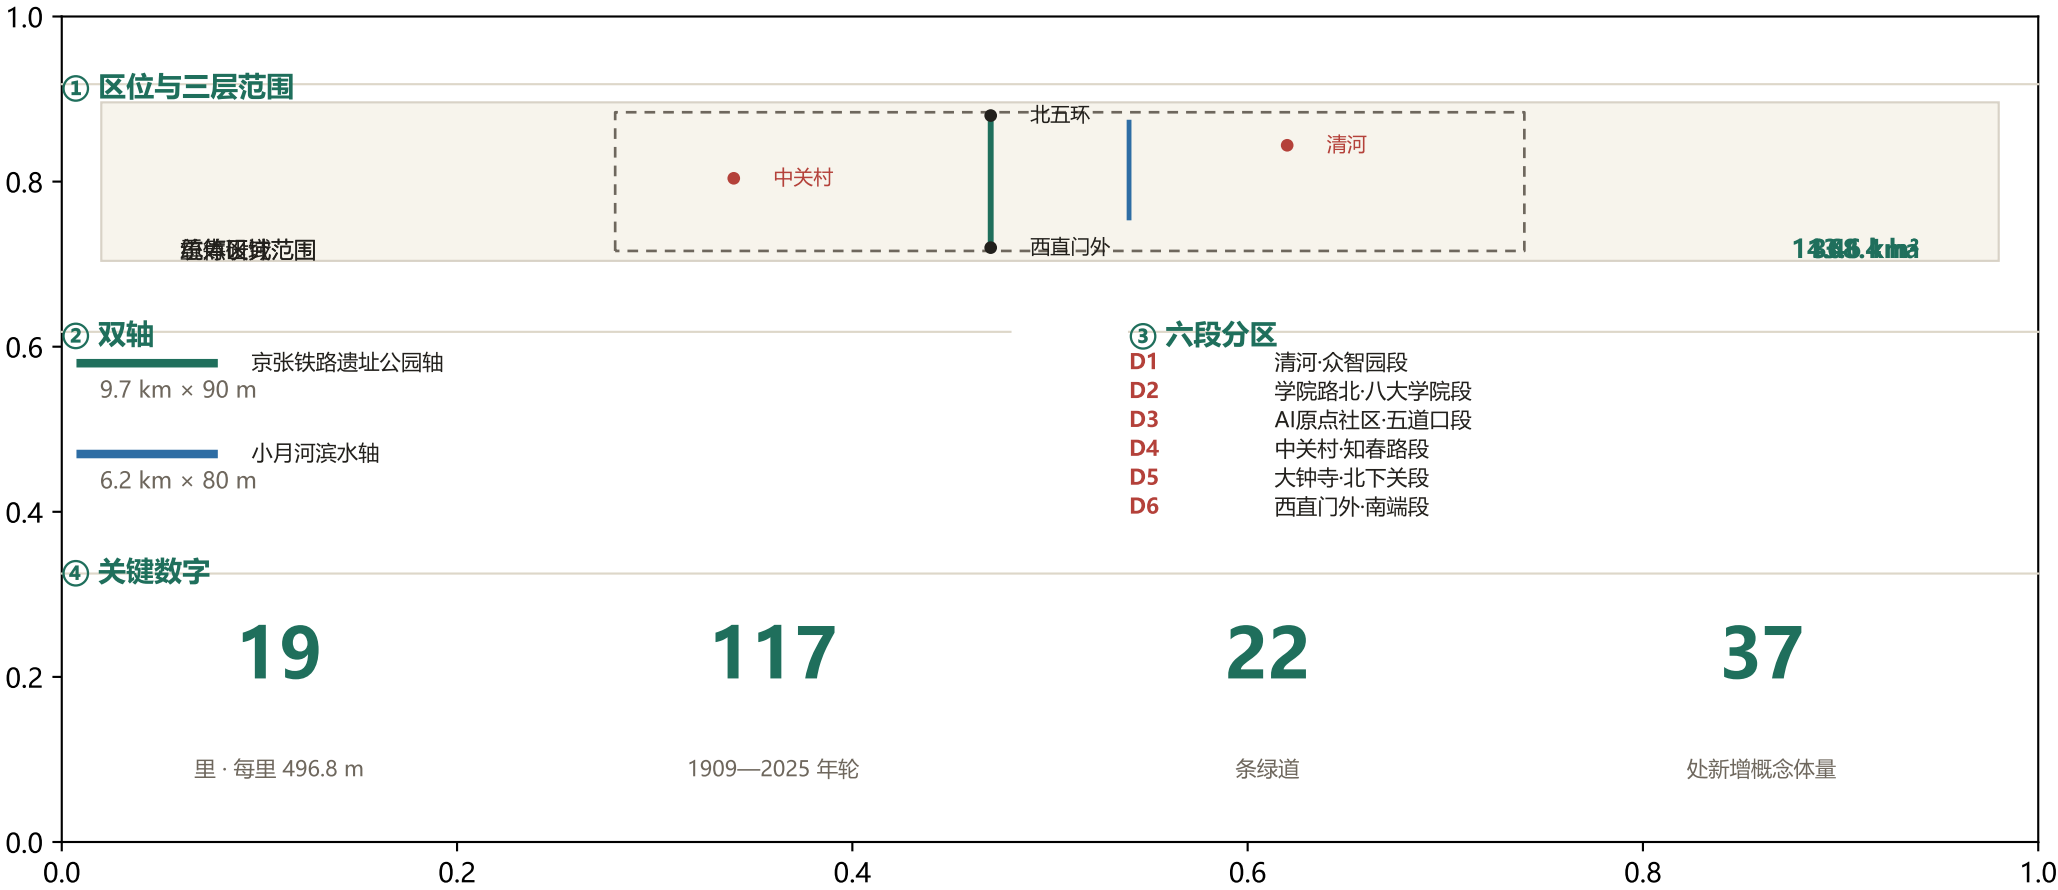


本图为概念设计解释层；场地边界与三处重点片区采用官方 provisional 几何，不得作为红线或审批依据。

01 场地总览：双轴夹一城

9.7 km 技术史轴 + 6.2 km 生态轴，中间夹住八大学院与中关村

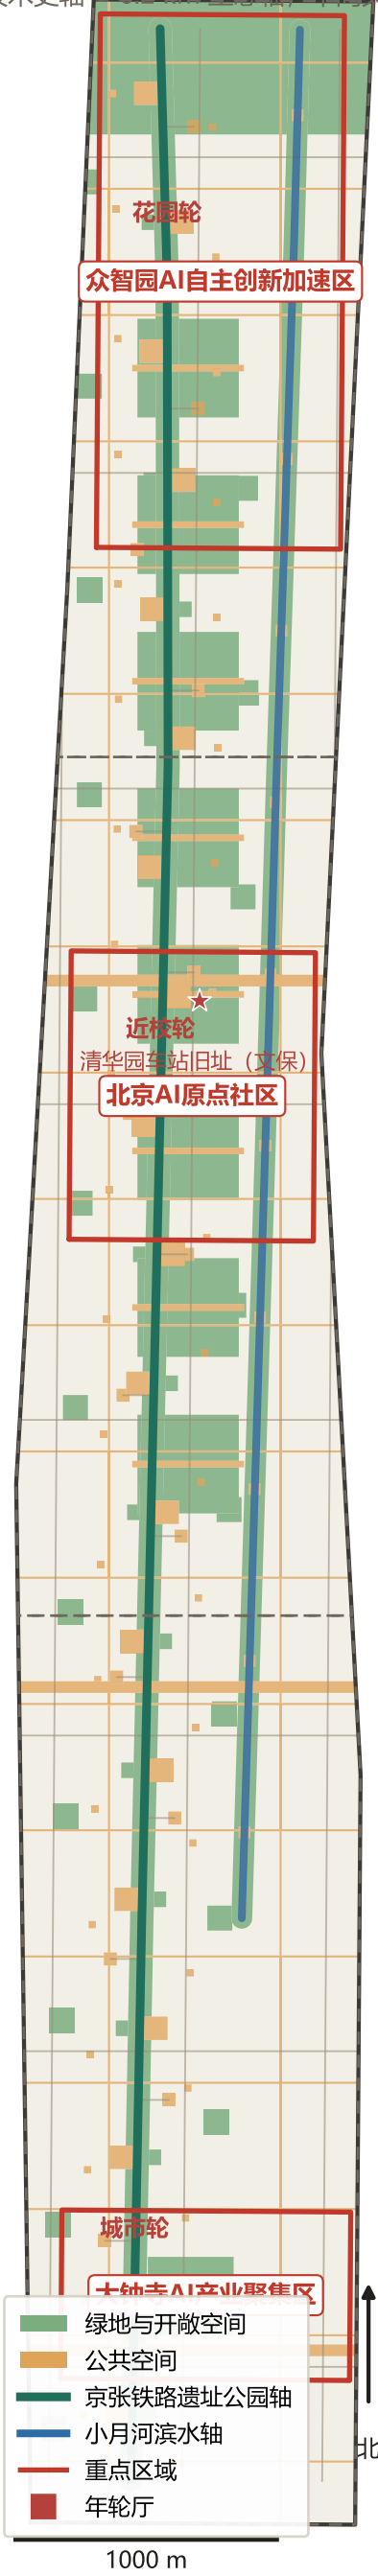

① 区位与三层范围

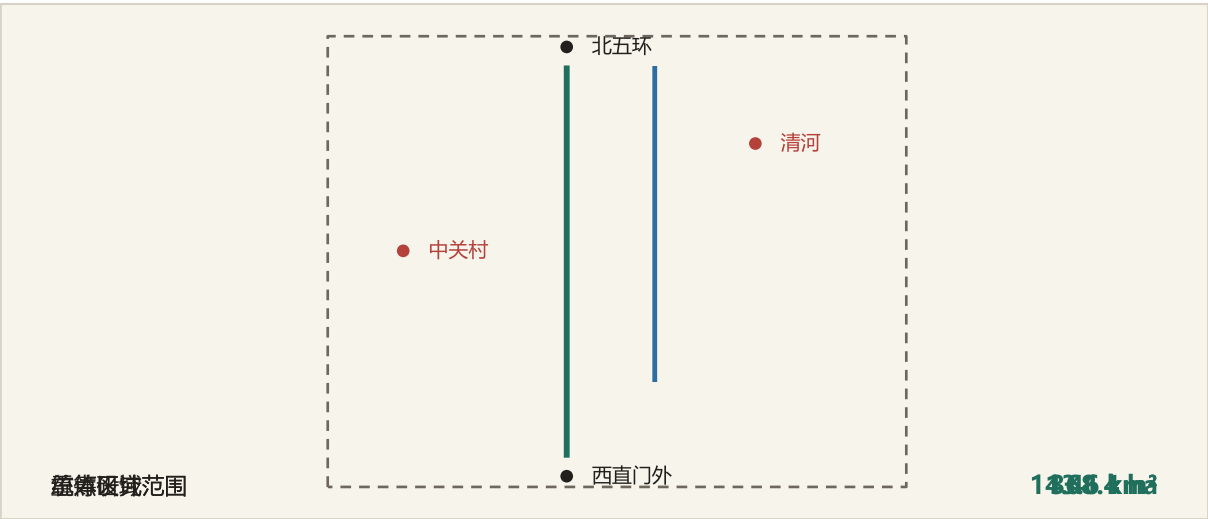

② 双轴

京张铁路遗址公园轴

9.7 km × 90 m

小月河滨水轴

6.2 km × 80 m

③ 六段分区

D1 清河·众智园段

D2 学院路北·八大学院段

D3 AI原点社区·五道口段

D4 中关村·知春路段

D5 大钟寺·北下关段

D6 西直门外·南端段

④ 关键数字

19

117

22

37

里 · 每里 496.8 m


1909—2025 年轮

条绿道

处新增概念体量

02 用地结构：三分与剖分

用地为对场地边界的严格剖分：无缝隙、无重叠、面积可复算

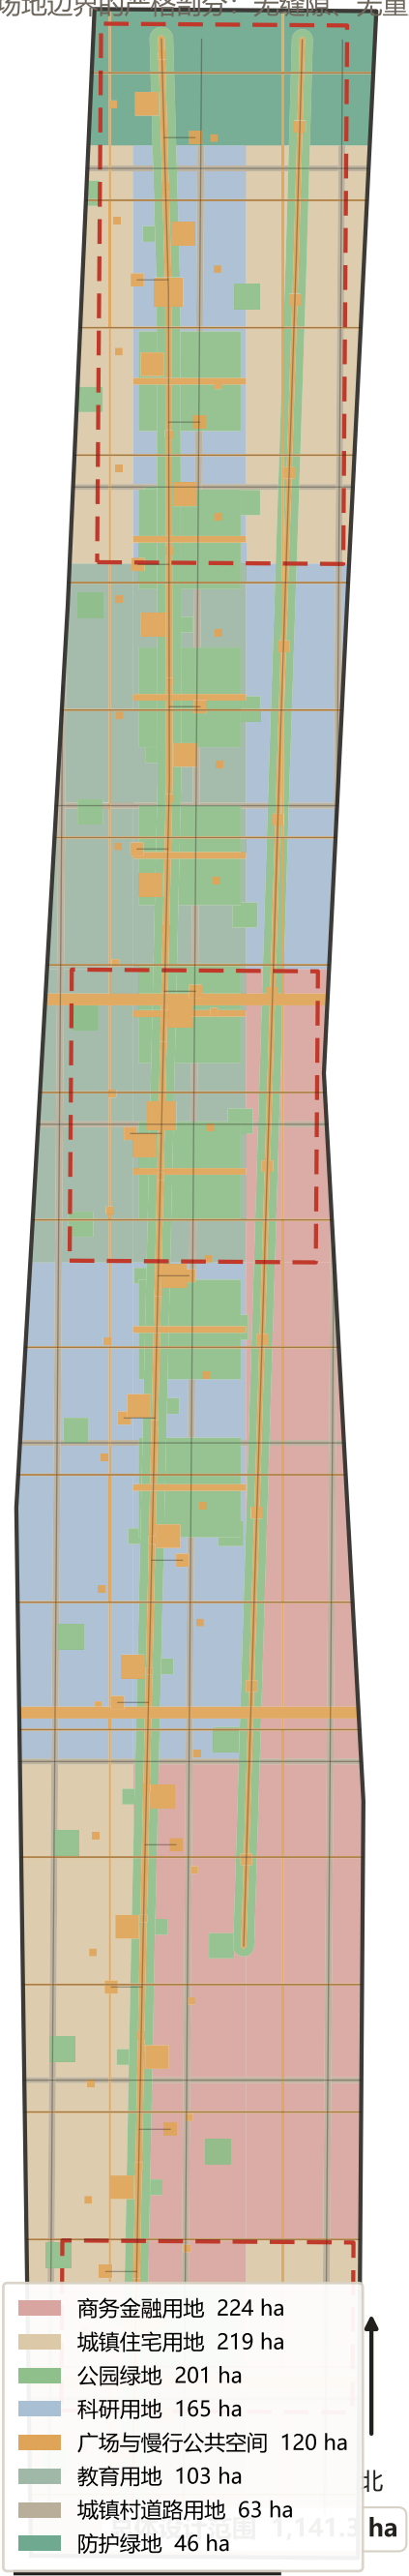

① 用地构成



国土空间用地分类（自然资发〔2023〕234号）场地子集


② 用地代码与面积

0902	商务金融用地	223.8 ha
0701	城镇住宅用地	219.4 ha
1401	公园绿地	200.8 ha
0802	科研用地	164.7 ha
1403	广场与慢行公共空间	120.3 ha
0804	教育用地	103.4 ha
1207	城镇村道路用地	63.4 ha
1402	防护绿地	45.5 ha

合计 = 场地面积 1,141.3 ha：用地为严格剖分，无缝隙、无重叠。

03 三处重点片区

三处片区各自对应一种年轮厅原型

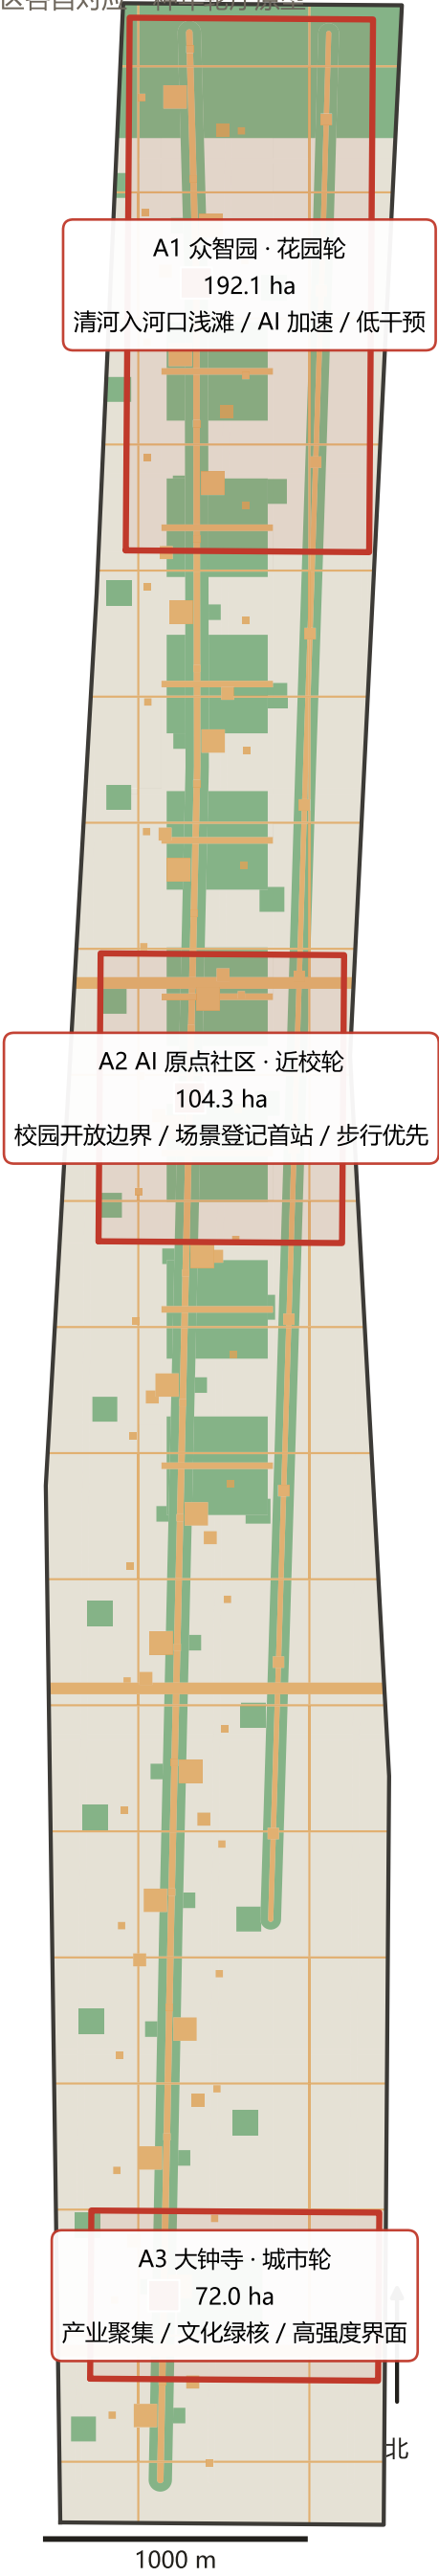

A1

众智园·花园轮

192.1 ha

- 清河入河口生态浅滩湿地
- 低干预：只做加法不做减法

A2

AI 原点社区·近校轮

104.3 ha

- 八大学院边界向城市打开 25 m
- 场景登记首站：先试、可退

A3

大钟寺·城市轮

72.0 ha


三处片区与三座年轮厅一一对应

- 产业聚集的高强度城市界面
- 大钟寺文化绿核

- 轨道接驳与公共空间复合

04 慢行与蓝绿系统

22 条绿道 + 双轴慢行主径，东西缝合被铁路与河道切断的街区

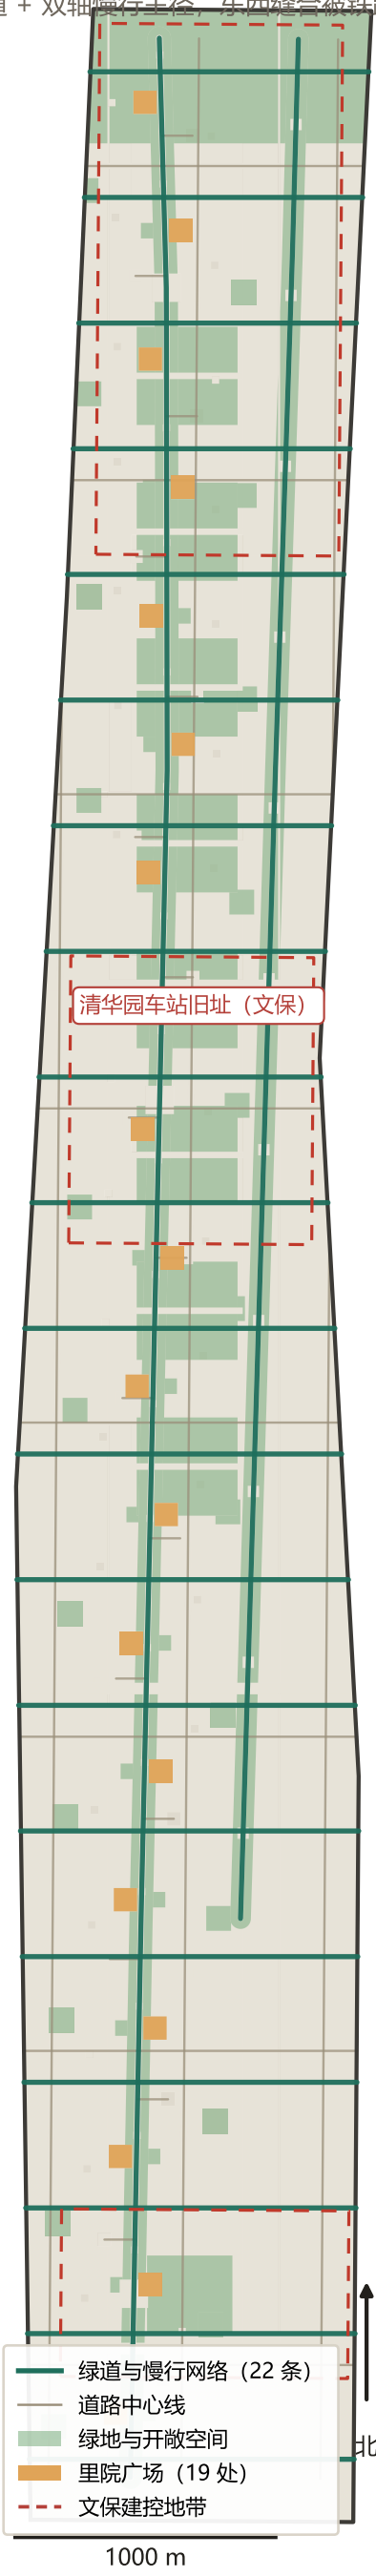

① 慢行网络

绿道总长	40.3 km
绿道条数	22
里院广场	19
接驳 / 滨水驿站	17 / 11
道路中心线	50

② 文保避让

★ 清华园车站旧址 (文保)

保护范围与Ⅰ类建控地带按保守外包表达；新增体量与建控地带的最小净距 12.2 m，控制地带内新建檐口限高 9 m。

③ 测试道路分级

开放	限制	禁入
允许低速配送与接驳测试	限时段、限速度、需人工复核	涉密院所、部队、校园红线内不测试


A • 提交几何复算值

A • 提交几何复算值

site_area_sqm	11,412,825.386	sqm	官方 provisional 边界 · EPSG:4548
green_space_area_sqm	2,463,013.830	sqm	green_space.geojson 并集
public_space_area_sqm	1,203,476.584	sqm	public_space.geojson 并集
building_footprint_area_sqm	15,855.006	sqm	37 处新增概念体量
green_ratio	0.2158	ratio	绿地/场地，非法定指标
public_space_ratio	0.1054	ratio	公共空间/场地

B • 证据链：每个数字都能追到文件

geometry/site_boundary.geojson	PROV-SITE-001	brief/site-package/geometry/provisional_boundaries.geojson
geometry/green_space.geojson	49 feats	EPSG:4548 U area
geometry/public_space.geojson	145 feats	EPSG:4548 U area

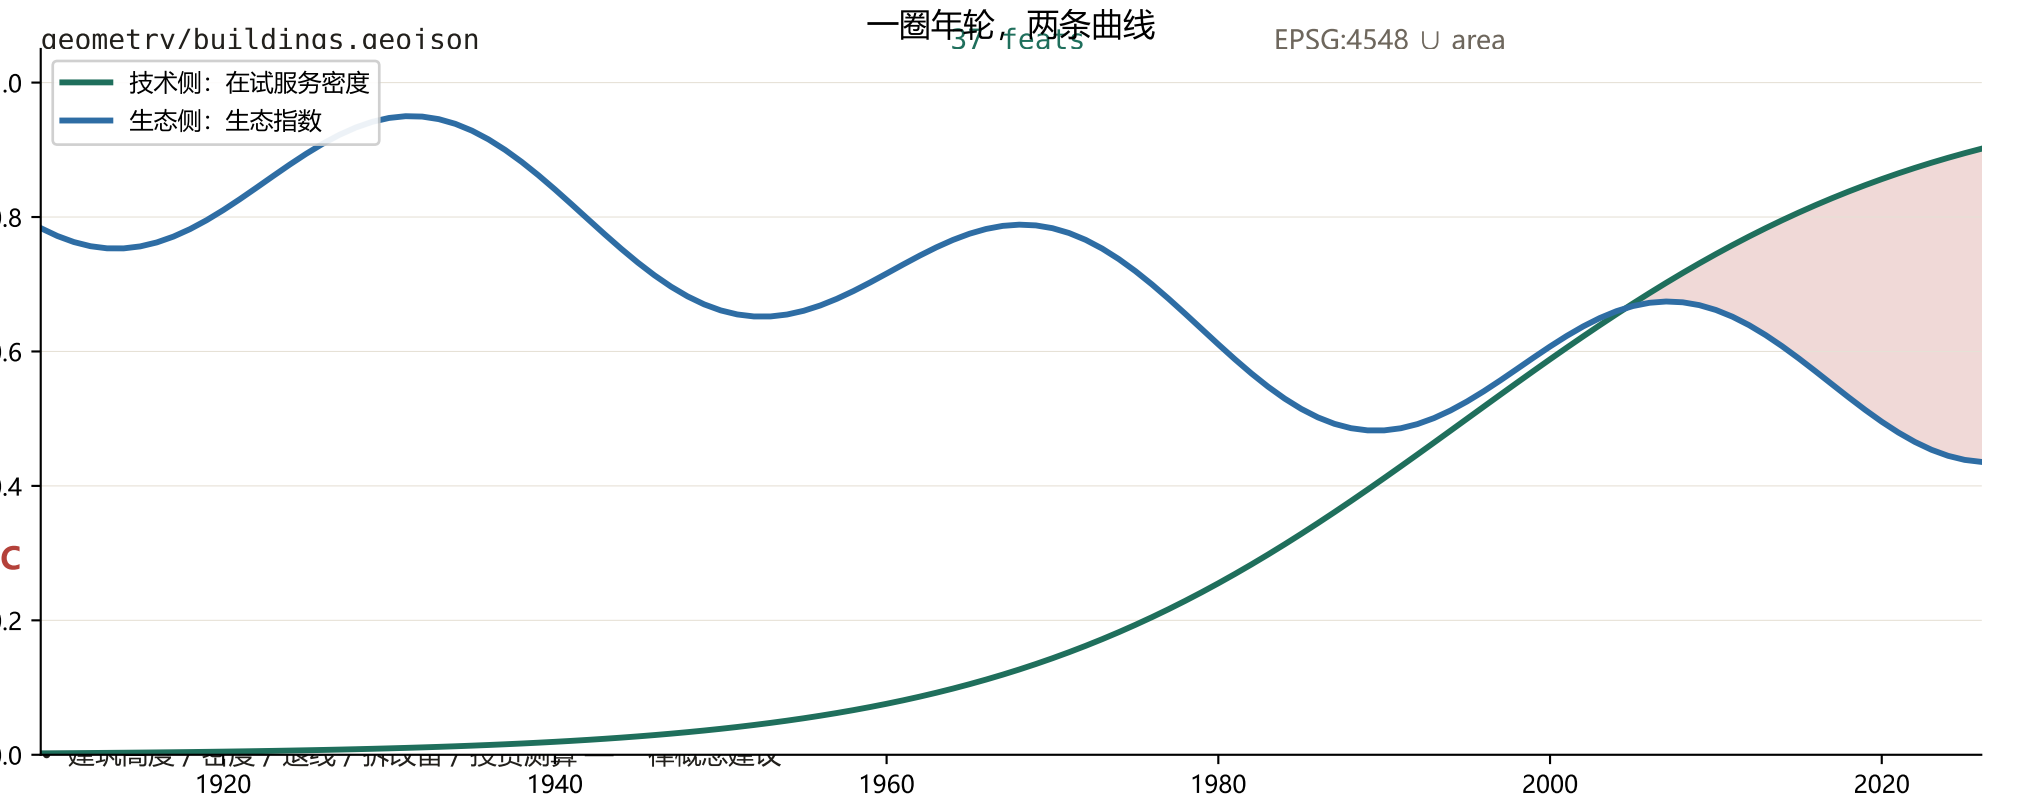

本方案放弃什么

01 放弃全线贯通

涉密院所、部队与部分高校红线内的段落不打通，承认断点，用借道绕行与界面化处理替代。

02 放弃无人化

保留早点摊主、修车师傅、门卫、保洁、驿站管理员，且不把他们的岗位计入效率优化目标。

03 放弃实时全域感知

只在非禁入区布设，数据不出院——院所与社区的数据留在本地服务器。

04 放弃控规类结论

容积率、高度、密度、绿地率、退线、拆改留、道路线位、投资测算一律只写概念建议。

05 放弃一次性建成

十年三期，前三年只做能做的；涉及权属突破的段落承认可能推不动。

06 放弃「优化市井」这个提法本身

改为先试、可退、居民说了算：有期限（12 个月）、可退出、有对照（A/B）、结果公开。