


Centennial Jing-Zhang AI Innovation Belt · concept proposal / reference scheme

THE NEAR SIDE • One-Page Overview

Criterion: any move claiming to bring AI into the city must first explain how it gets from the park edge to a door an ordinary person can reach. Three covenants: crossable - closable - countable

- The submitted area averages 1,188 m wide (594 m half-width); 99.98% lies within 650 m of the spine
- The near side (0-300 m) is 51.1% of the belt and its main working surface
- 33 near-side units, one per 300 m, each with a near-side room and a 2 4-hour passage

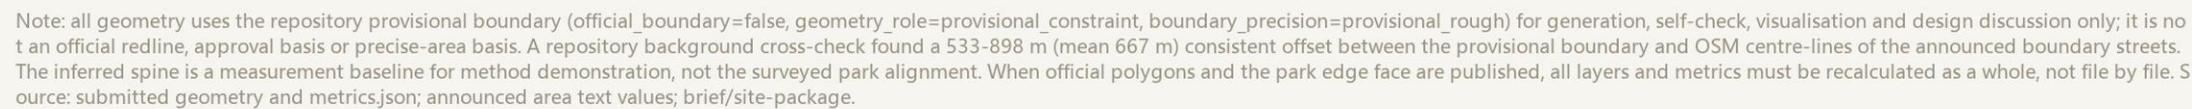

THE NEAR SIDE - The Last 300 Metres • A3 Booklet

Turn the last 300 metres outside the park edge into the belt's first asset. All content is a conceptual proposal and reference scheme, not statutory planning.

Centennial Jing-Zhang AI Innovation Belt · concept proposal / reference scheme

Land-Use Structure and the Three Rings

Land use is a complete partition of the submitted area (no gaps, no overlaps). The three rings are measured from the park edge face: near side 0-300 m, seepage ring 300-500 m, link ring beyond 500 m, each with its own renewal action and phasing.

Criterion: any move claiming to bring AI into the city must first explain how it gets from the park edge to a door an ordinary person can reach. Three covenants: crossable - closable - countable

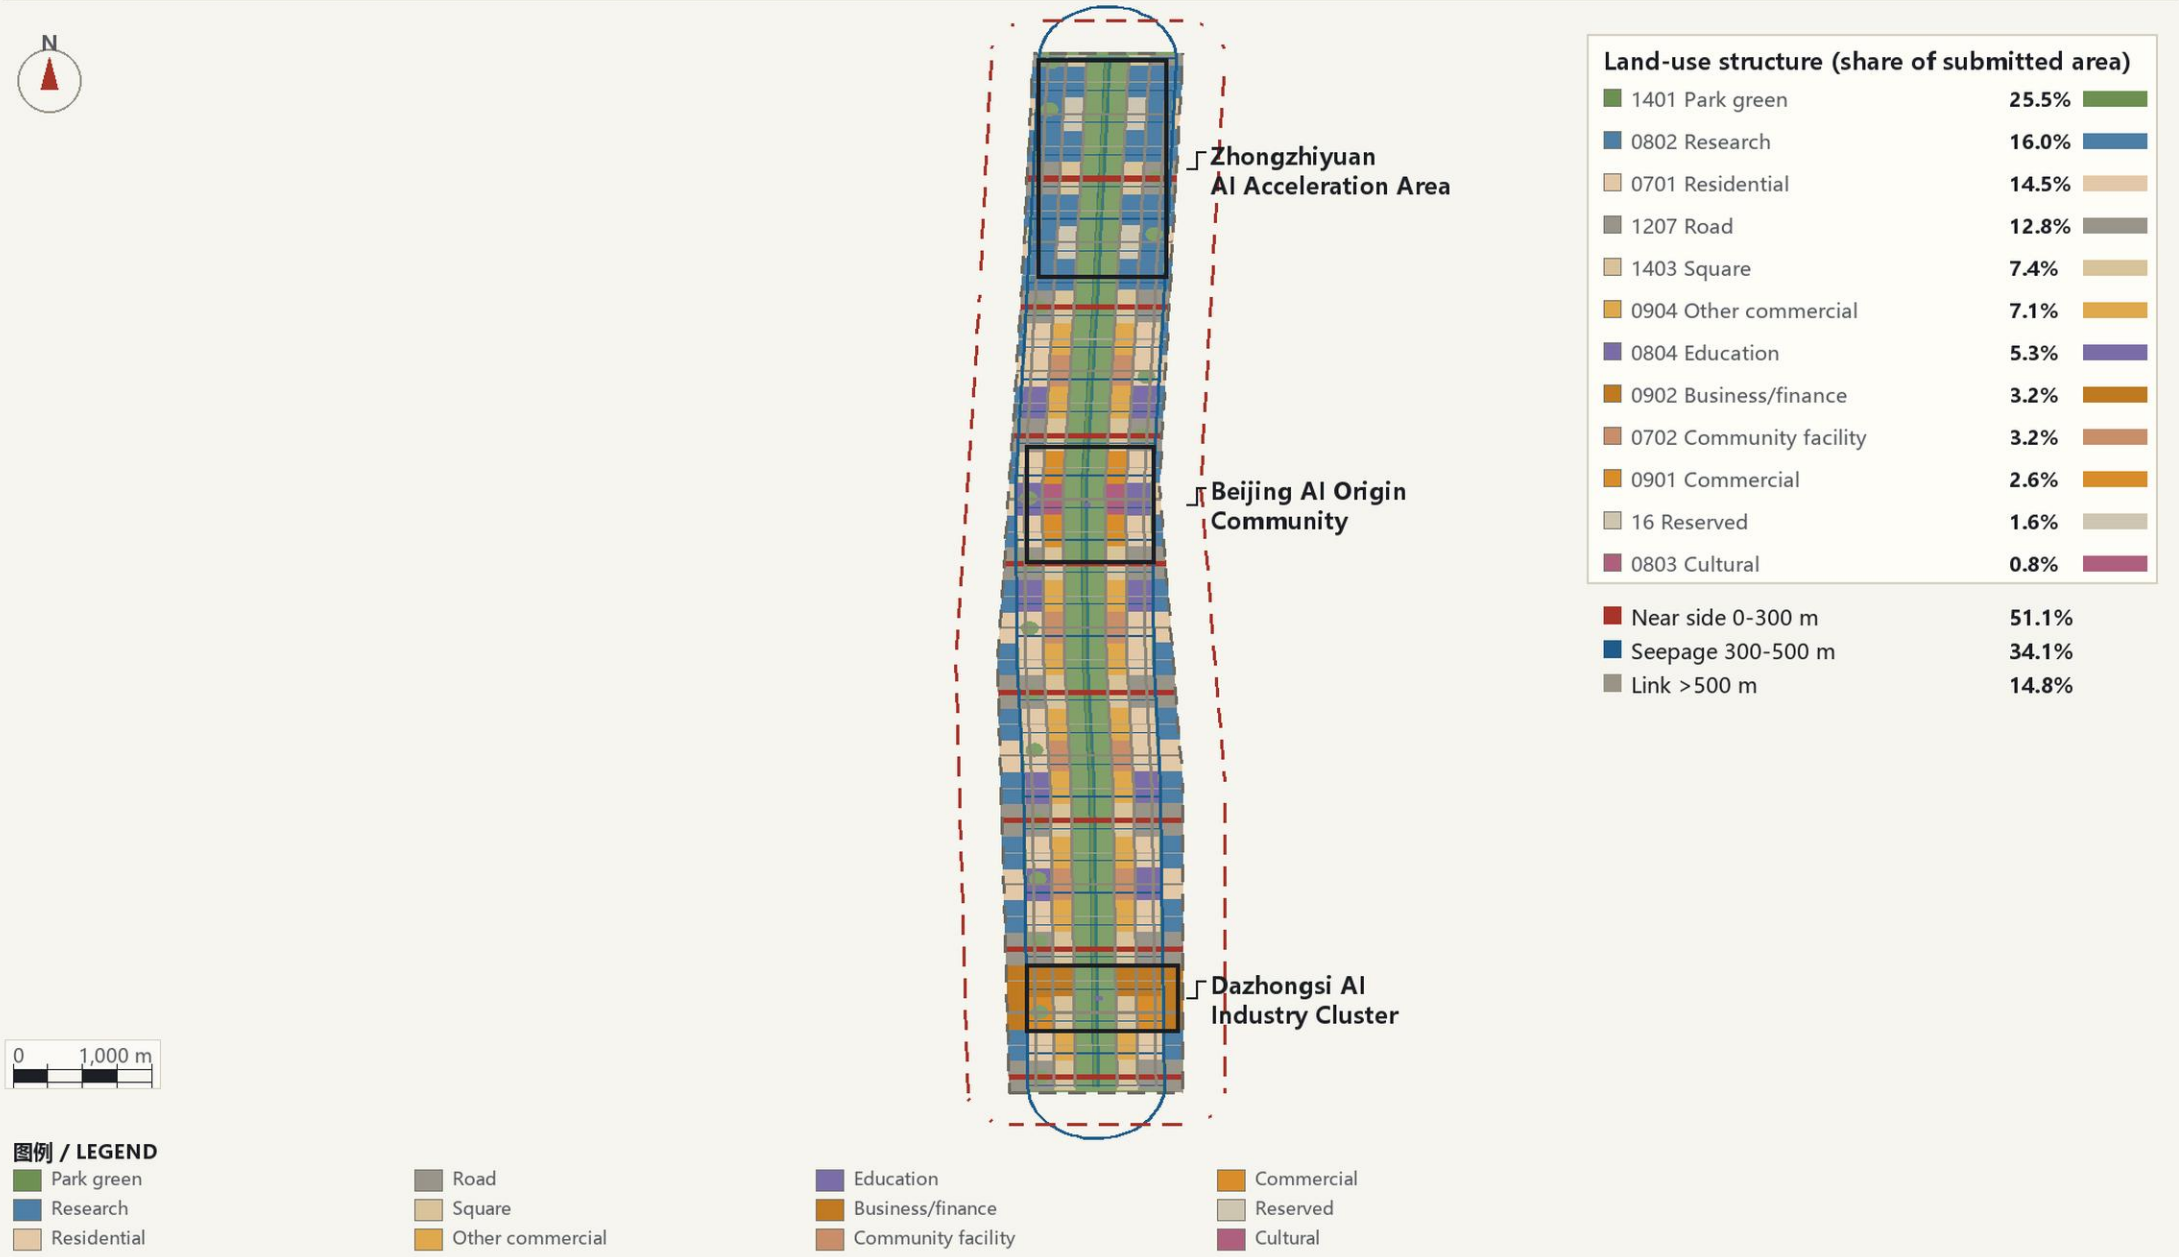


Fig. 2 Land use and three rings: a complete partition with no gaps and no overlaps

- The partition has no gaps and no overlaps: 139 parcels cover 100% of the submitted area
- Park green is the largest single use at 291.5 ha (25.5%); 18.0 ha of reserve land hosts controlled tests
- Three rings: near side 51.1%, seepage ring 34.1%, link ring 14.8%

THE NEAR SIDE - The Last 300 Metres • A3 Booklet

Turn the last 300 metres outside the park edge into the belt's first asset. All content is a conceptual proposal and reference scheme, not statutory planning.


Centennial Jing-Zhang AI Innovation Belt · concept proposal / reference scheme

Detailed Design for the Three Key Areas

Each key area solves one kind of 'last 300 metres': the north reserves interfaces in new development, the middle opens institute walls, the south completes the last stretch from the transit station to the destination.

Criterion: any move claiming to bring AI into the city must first explain how it gets from the park edge to a door an ordinary person can reach. Three covenants: crossable - closable - countable


Zhongzhiyuan AI Acceleration Area Announced ~192.1 ha

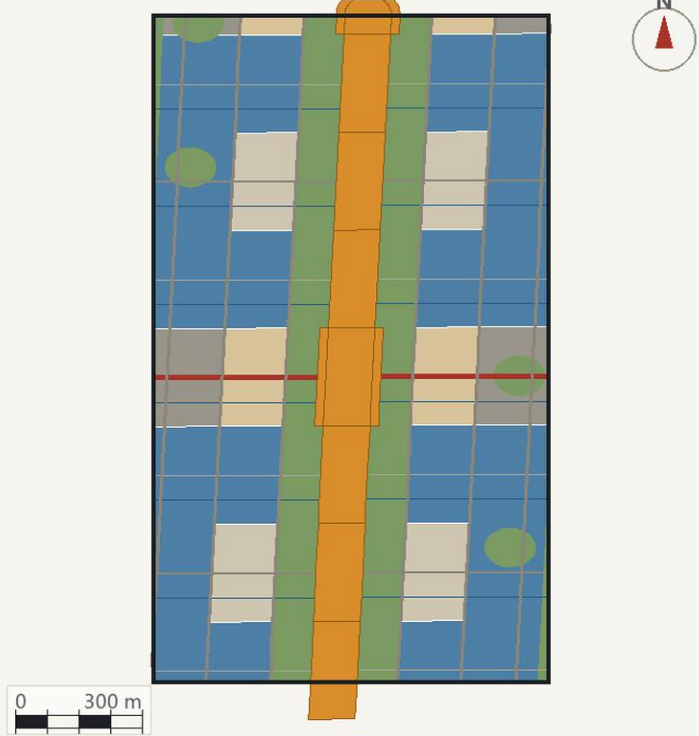

North • reserve the interfaces first

- A predominantly new-build key area. 18.0 ha of reserved land inside the 0-300 m near-side band hosts controlled validation of low-speed shuttles, delivery robots and smart fixtures.
- Near-side units NU-27 to NU-33: one near-side room and one 24-hour public passage each.
- Sequence: fix the park edge face, then the interface ledger, then the parcels. Never reversed.


Beijing AI Origin Community Announced ~104.3 ha

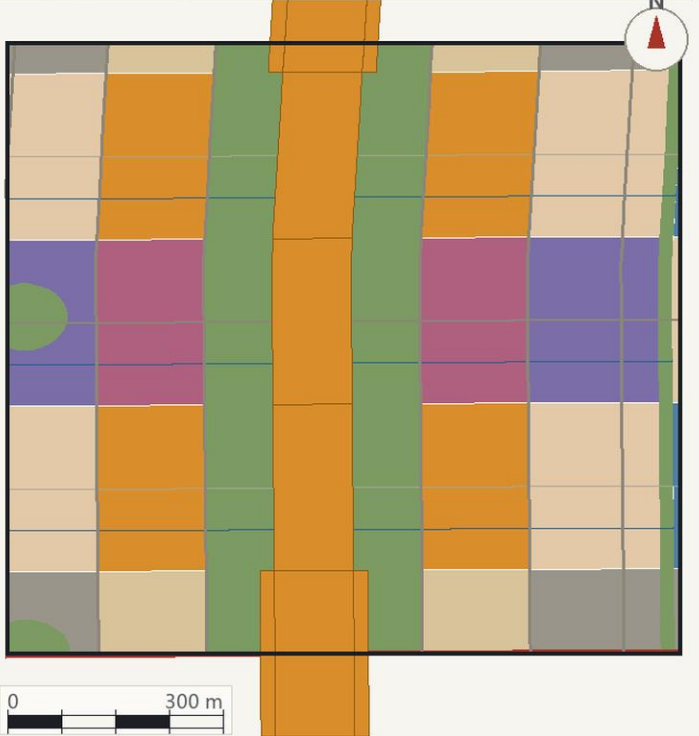

Middle • turn institute walls into countable doors

- A predominantly existing-fabric key area. The move is not new construction but adding crossable, closable and countable public interfaces onto existing walls and compound edges.
- Near-side units NU-13 to NU-20: ground-floor frontage targets and an obstacle list per unit.
- Deliverable: a 'last-300-metre obstacle ledger' itemising walls, gates, dead ends, kerbside parking and accessibility breaks.

Dazhongsi AI Industry Cluster Announced ~72.0 ha

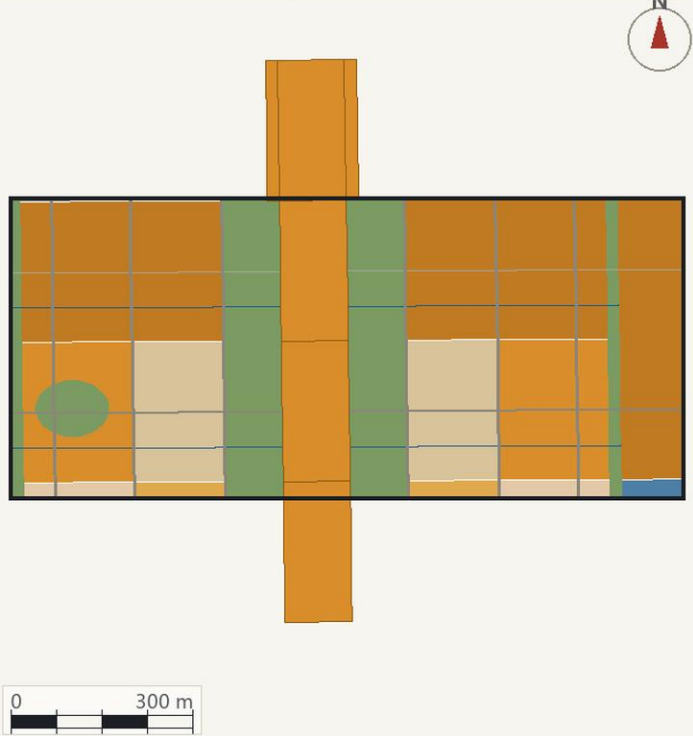

South • finish the last stretch from the station

- A transit-station and business cluster. Here the last 300 metres takes a concrete shape: exit the station, cross the street, enter the square, reach the ground floor.
- Near-side units NU-01 to NU-06: business and commercial near-side frontage with crossing squares.
- Move: no grand engineering - close the breaks in four path segments and name a responsible role for each.

图例 / LEGEND

Green	Research	Commercial/business	Reserved
Near-side room / crossing square	Residential	Education	Road

Fig. 3 Three key areas: reserve interfaces north, open gates mid, reach the ground floor south

- North, Zhongzhiyuan 192.9 ha: reserve interfaces - fix the park edge face, then the interface list, then parcels
- Middle, AI Origin Community 104.3 ha: add crossable, closable, countable doors onto existing walls
- South, Dazhongsi 72.0 ha: exit, cross, enter the square, reach the ground floor - close every break

THE NEAR SIDE - The Last 300 Metres • A3 Booklet

Turn the last 300 metres outside the park edge into the belt's first asset. All content is a conceptual proposal and reference scheme, not statutory planning.

Centennial Jing-Zhang AI Innovation Belt · concept proposal / reference scheme

Mobility, Blue-Green Network and the Near-Side Section

Design road-network density 9.80 km/km2, a 9,608 m continuous green spine, 42 public interface points and 33 near-side units. The section breaks the last 300 metres into five measurable bands.

Criterion: any move claiming to bring AI into the city must first explain how it gets from the park edge to a door an ordinary person can reach. Three covenants: crossable - closable - countable

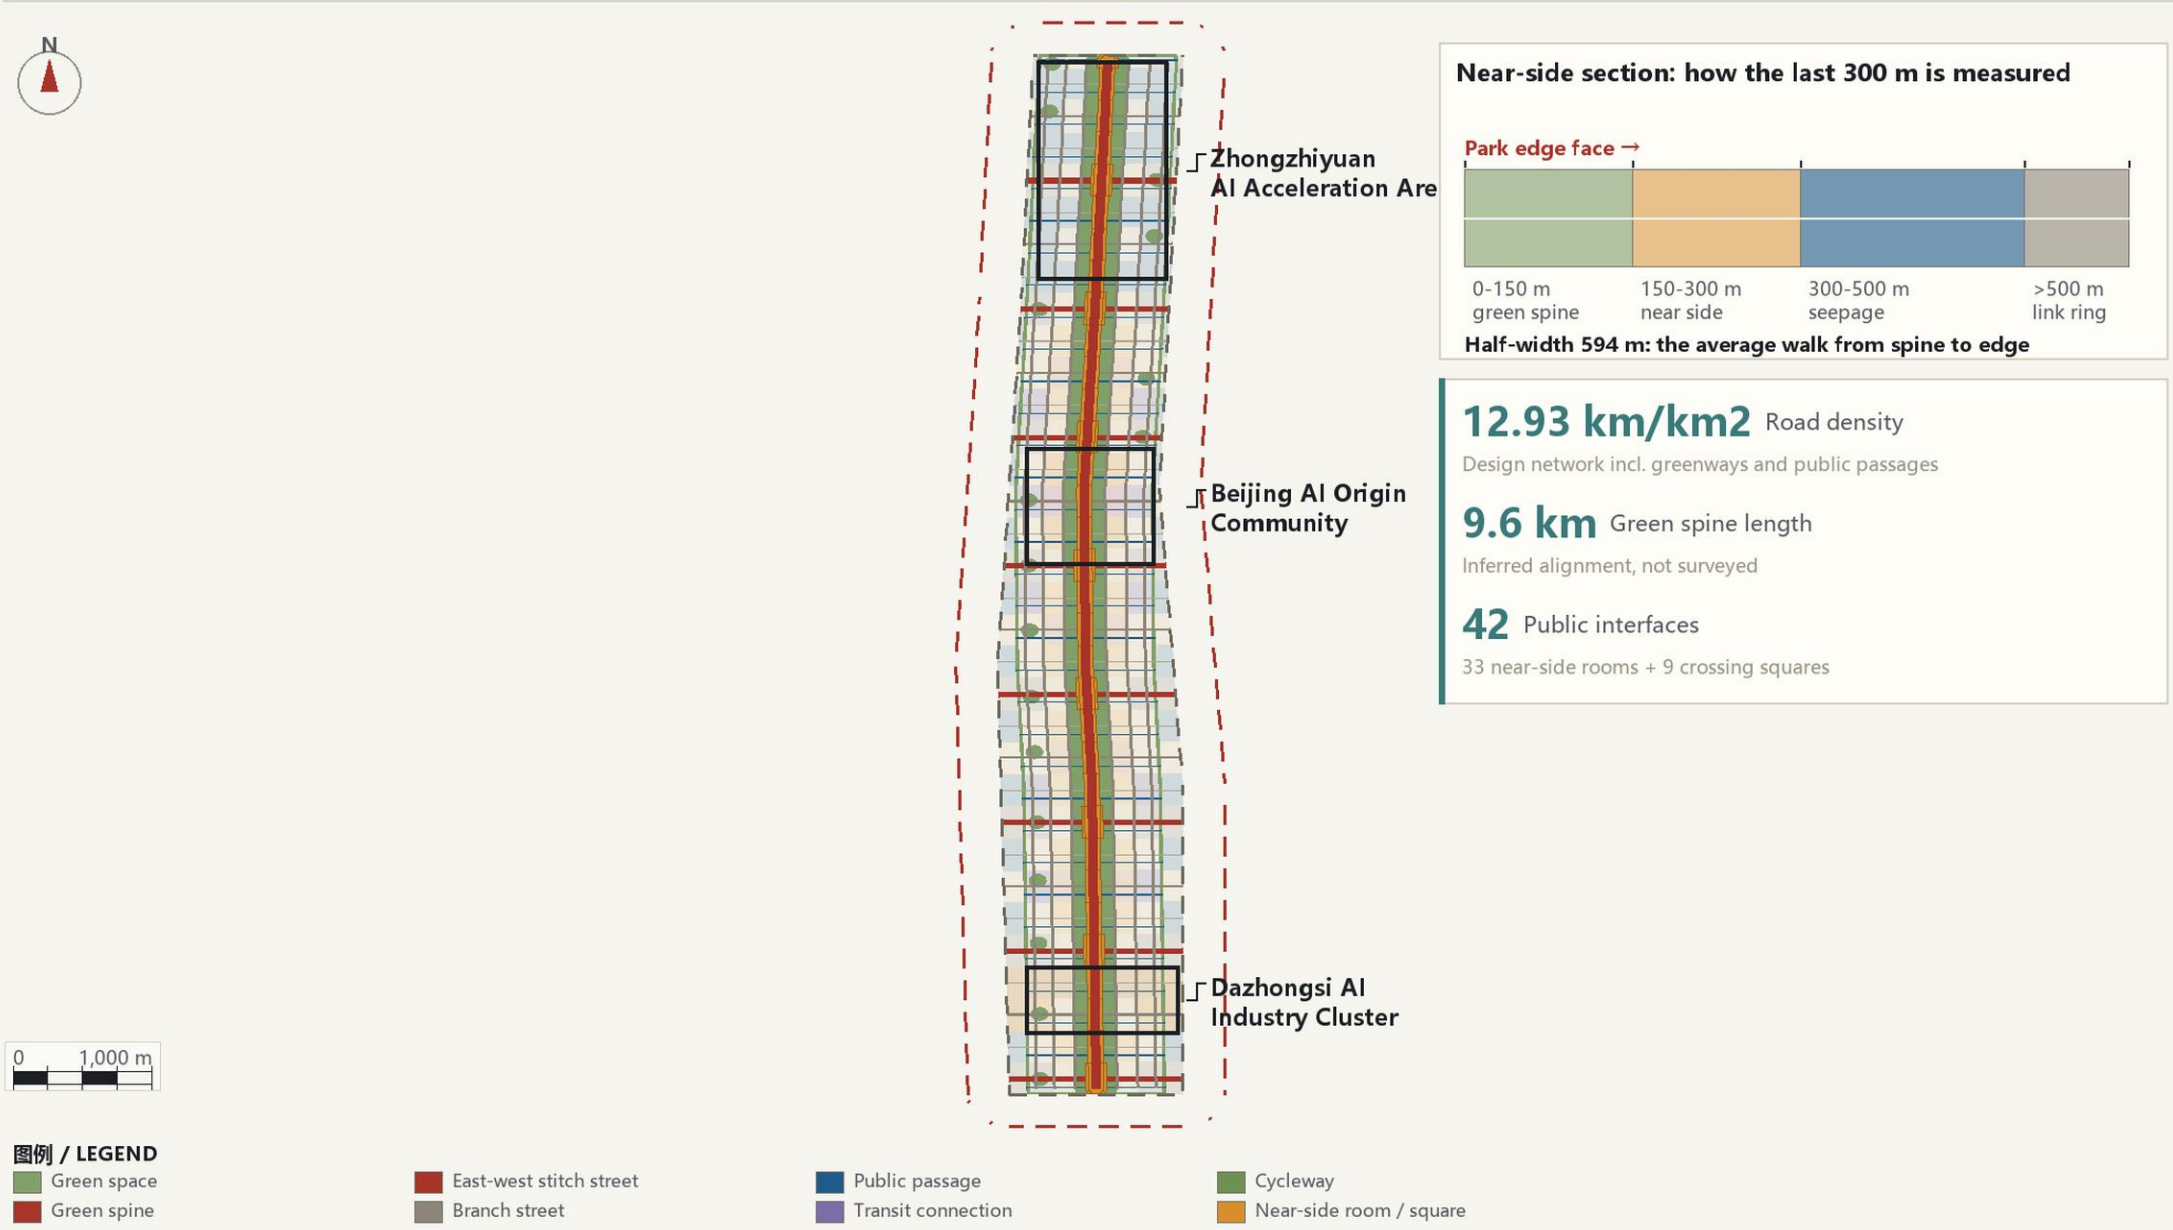


Fig. 4 Mobility, blue-green and near-side section: the last 300 m split into five measurable bands

- Design network density 12.9 km/km2, of which 8.4 km/km2 carries vehicles
- 9.6 km green spine, 42 public interfaces, 33 near-side units
- The last 300 m is split into five measurable bands; the belt's half-width is only 594 m

THE NEAR SIDE - The Last 300 Metres • A3 Booklet


Turn the last 300 metres outside the park edge into the belt's first asset. All content is a conceptual proposal and reference scheme, not statutory planning.

Centennial Jing-Zhang AI Innovation Belt · concept proposal / reference scheme

Core Metric Recalculation and Evidence Chain

The three formal core visual metrics are recomputed from the submitted site_boundary, green_space and public_space geometry and match the numeric values declared in visual/index.html; metrics that depend on unpublished controls are recorded as pending official data.

Criterion: any move claiming to bring AI into the city must first explain how it gets from the park edge to a door an ordinary person can reach. Three covenants: crossable - closable - countable

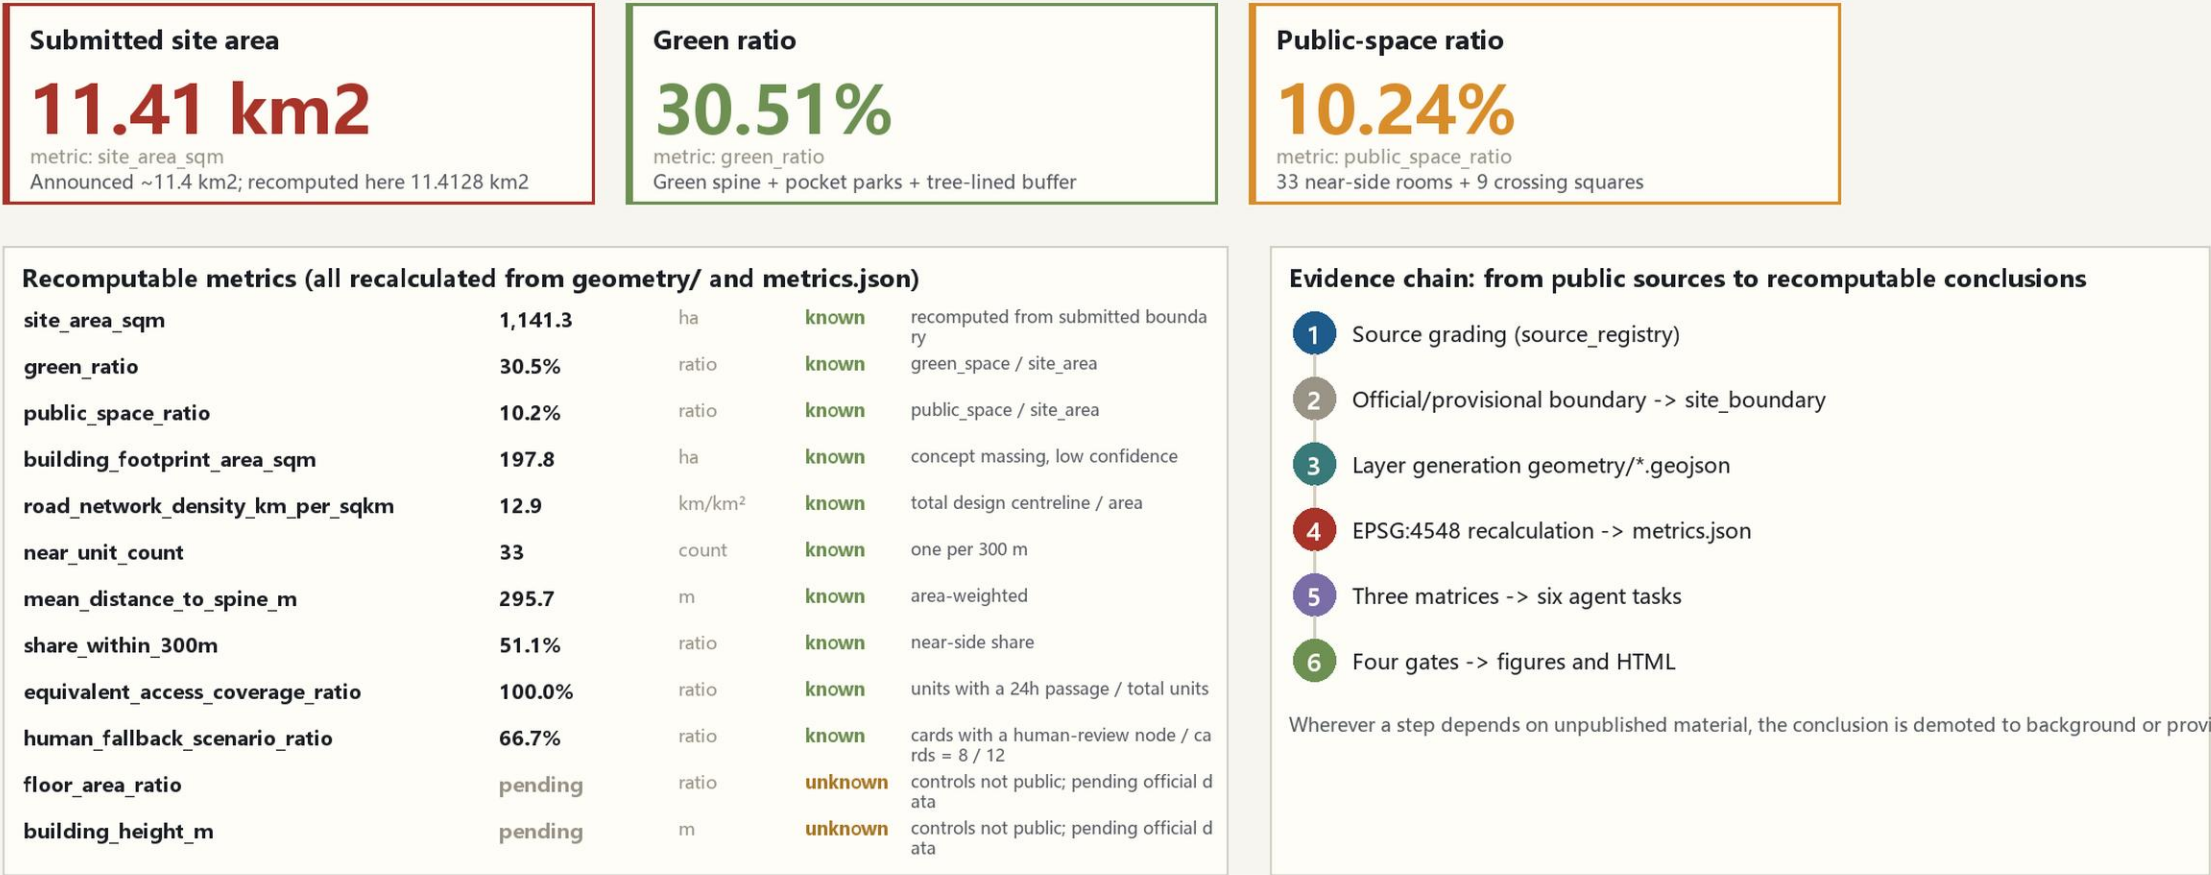

Precision warning: all geometry rests on the repository provisional boundary. Missing organiser polygons do not block content scoring, but this package does not claim its areas equal official precise areas. Everything is recalculated once official data is published.

Note: all geometry uses the repository provisional boundary (official_boundary=false, geometry_role=provisional_constraint, boundary_precision=provisional_rough) for generation, self-check, visualisation and design discussion only; it is not an official redline, approval basis or precise-area basis. A repository background cross-check found a 533-898 m (mean 667 m) consistent offset between the provisional boundary and OSM centre-lines of the announced boundary streets. The inferred spine is a measurement baseline for method demonstration, not the surveyed park alignment. When official polygons and the park edge face are published, all layers and metrics must be recalculated as a whole, not file by file. Source: submitted geometry and metrics.json; announced area text values; brief/site-package.

Fig. 5 Core metric recalculation and evidence chain

- The three formal core metrics are recomputed from the submitted geometry in EPSG:4548
- Every recomputable metric ships with a formula, source files and status
- Metrics depending on unpublished controls stay unknown rather than posing as known

Executive Summary / 一页摘要

Turn the last 300 metres outside the park edge into the belt's first asset. All content is a conceptual proposal and reference scheme, not statutory planning.

Executive Summary / 一页摘要

- Criterion: any move claiming to bring AI into the city must first explain how it gets from the park edge to a door an ordinary person can reach. Three covenants: crossable, closable, countable.
- The area-weighted mean distance to the spine is 295.7 m; near side (0-300 m) 51.1%, seepage ring (300-500 m) 34.1%, link ring (>500 m) 14.8%.
- The proposal therefore defines the last 300 metres not as a slogan but as a band recomputable from the submitted geometry, organising land use, streets, public space and phasing into three rings.
- Three formal core visual metrics: site area 11.41 km2; green ratio 33.6%; public-space ratio 10.2%.
- Metrics depending on unpublished controls (FAR, height, density, setback, ownership, station coordinates, heritage and blue lines) are recorded as pending official data.

Full narrative, all 54 metrics and the machine-readable ledger are in [report/proposal.html](#) and [visual/index.html](#); the 33-unit ledger is at [visual/assets/near_side_units.json](#).

Renewal Projects / 更新项目清单

Turn the last 300 metres outside the park edge into the belt's first asset. All content is a conceptual proposal and reference scheme, not statutory planning.

Renewal Projects / 更新项目清单

- R0 Park edge face survey - whole belt, 0-6 months; planning authority plus surveyor; dependency of all later projects.
- R1 Near-side unit ledger - 33 units, phase 1; streets, communities and AI assistant.
- R2 Accessibility-break repair - priority NU-13 to NU-20, phase 1; streets and owners.
- R3 Low-speed robot Test Street - Zhongzhiyuan, phase 1; management committee and firms; stops if two consecutive safety audits fail.
- R4 Institute public-interface retrofit - AI Origin Community, phase 2; skip unit if any owner objects.
- R5 Talent apartments and mixed blocks - seepage ring, phase 2; revert to retain if feasibility insufficient.
- R6 Dazhongsi station-front Arrival Hall - phase 2; transit operator and streets.
- R7 Regional synergy interfaces - key-area link rings, phase 3; maintain status quo if coordination fails.

Full narrative, all 54 metrics and the machine-readable ledger are in [report/proposal.html](#) and [visual/index.html](#); the 33-unit ledger is at [visual/assets/near_side_units.json](#).

Risk and Compliance / 风险与合规

Turn the last 300 metres outside the park edge into the belt's first asset. All content is a conceptual proposal and reference scheme, not statutory planning.

Risk and Compliance / 风险与合规

- Data boundary: all spatial data come from the repository provisional boundary or derivations on it; no non-public planning maps, non-official CAD/GIS or internal data.
- Copyright: all figures, logos and text are generated by this proposal's code or author; no unauthorised fonts, images, trademarks, portraits or enterprise identifiers.
- Privacy: AI scenarios collect no facial-recognition data, personal movement or sensitive health information; every AI service keeps a human or paper equivalent path.
- Official approval and implementation: all spatial proposals are conceptual proposals and reference schemes for professional teams to deepen; not statutory planning or government approval.
- Missing data: official boundary polygon, precise park edge face, regulatory controls, land ownership, heritage and blue lines, rail station/entrance coordinates.

Full narrative, all 54 metrics and the machine-readable ledger are in [report/proposal.html](#) and [visual/index.html](#); the 33-unit ledger is at [visual/assets/near_side_units.json](#).