

京张近端 / THE NEAR SIDE —— 最后三百米 • A3 文本


把公园边界外的最后 300 米，做成百年京张 AI 创新带的第一资产。全部内容为概念建议、参考方案，不替代法定规划。

百年京张AI创新带城市设计开源征集 · 概念建议 / 参考方案

京张近端 • 一页总览

这条带没有腹地：提交范围平均宽度仅 1,188 米，半宽 594 米，99.98% 的用地位于推定主脊 650 米以内。最后三百米不是这条带的一段——它就是这条带的全部。

判准：任何宣称「AI 进城」的空间动作，必须先说明它如何从公园边界面走到一个普通人能走到的门口。近端三约：可穿越 • 可关闭 • 可计数

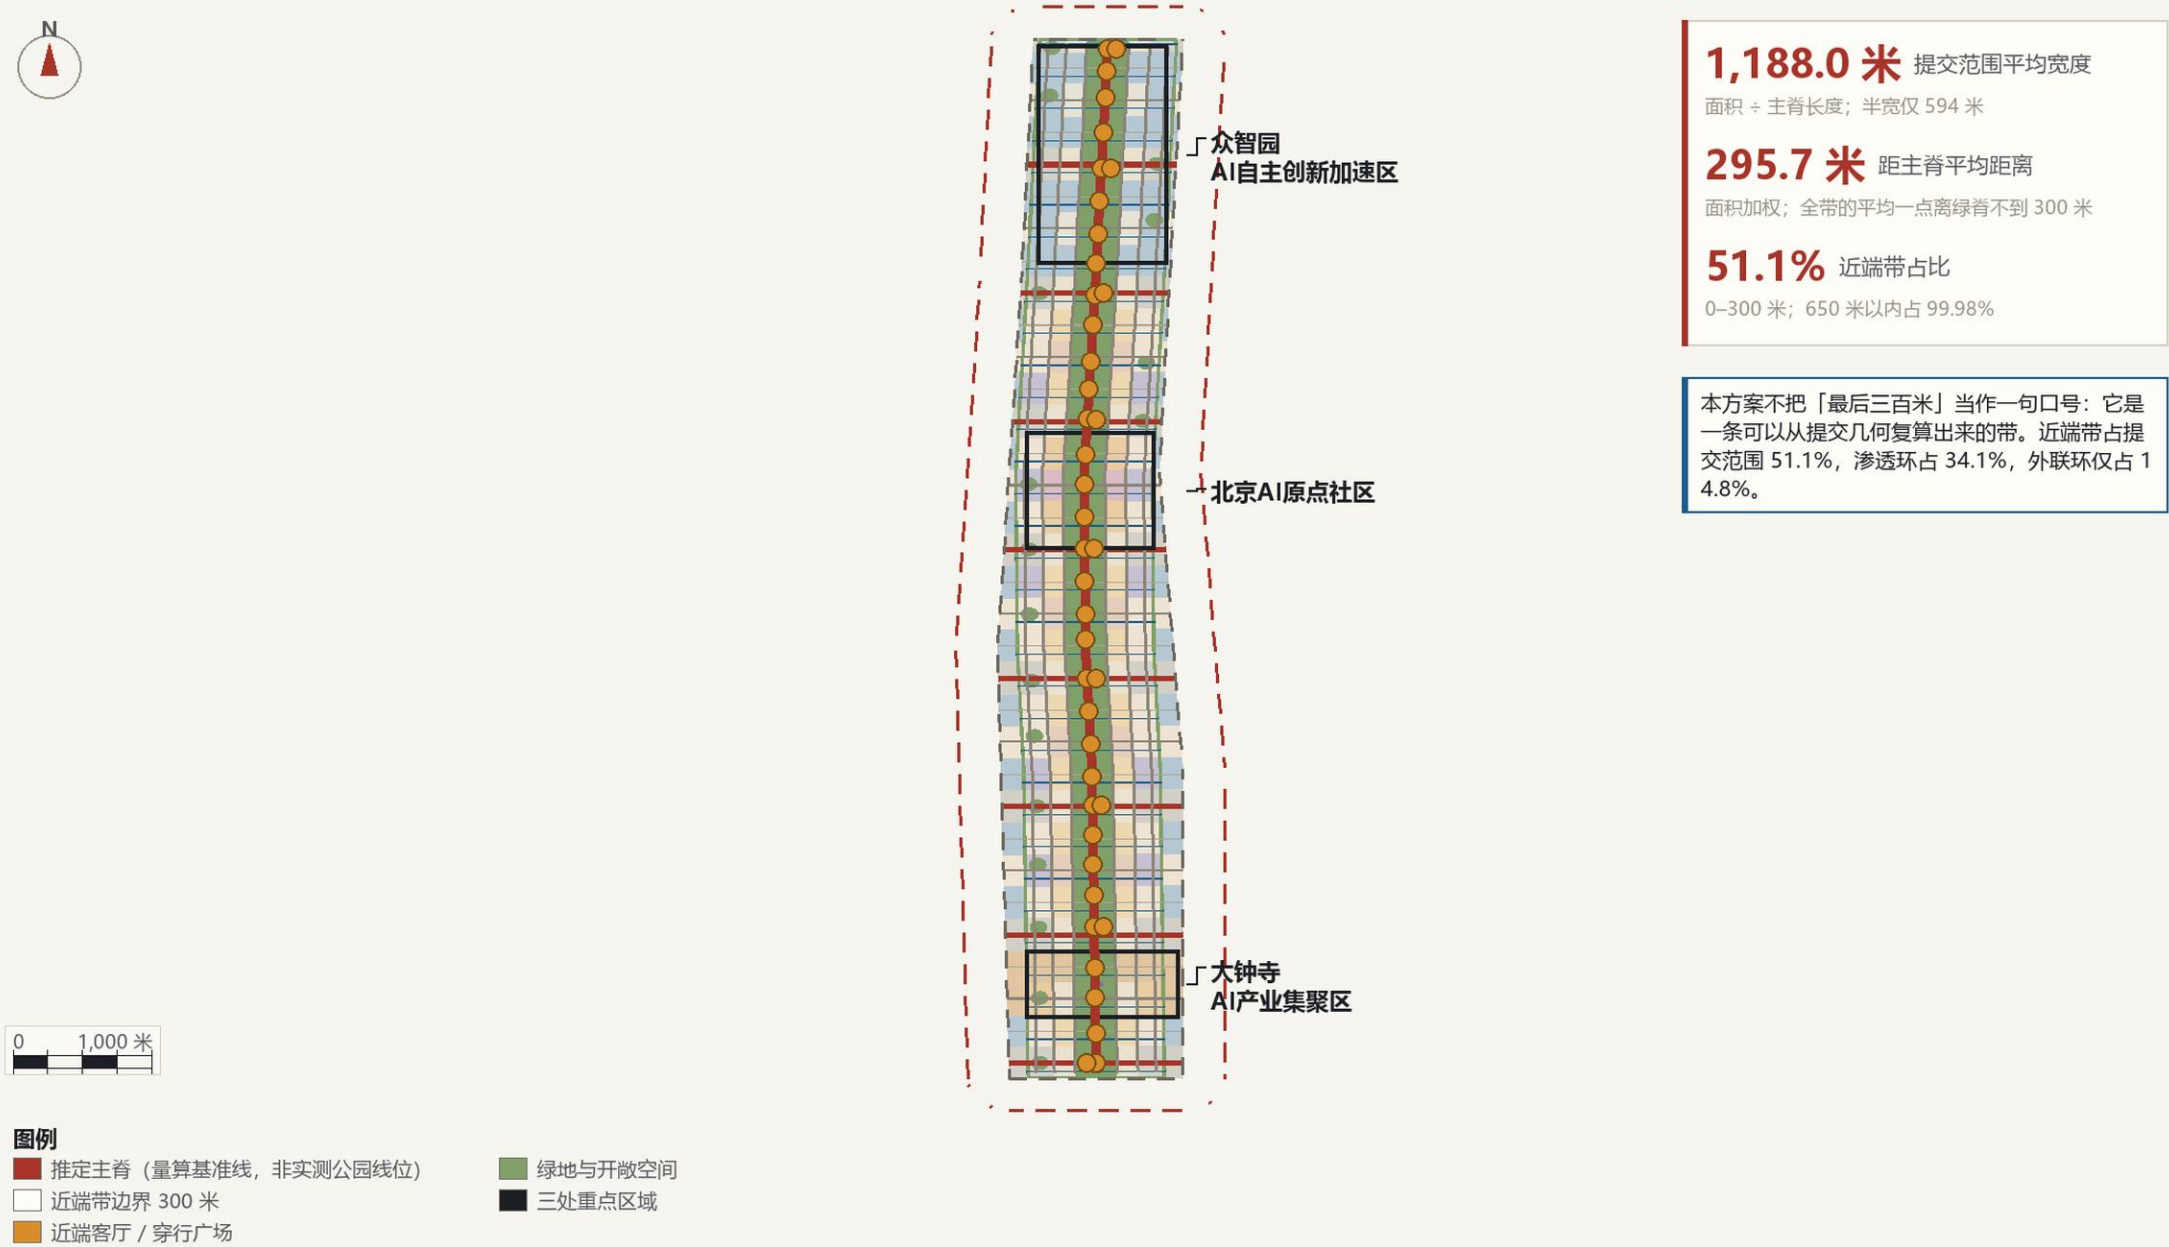

注：本包全部空间几何采用仓库临时粗略边界（official_boundary=false, geometry_role=provisional_constraint, boundary_precision=provisional_rough），仅用于生成、自检、可视化与设计讨论，不得作为官方红线、审批依据或精确面积依据。仓库背景核对显示：临时边界与公告命名街道的 OSM 实测中线存在 533–898 米（均值 667 米）同向偏移；图中推定主脊为方法演示用的量算基准线，不等于京张遗址公园实际线位。官方 polygon 与公园边界面发布后，全部图层与指标须整体重算，不得只替换单个文件。 来源：本方案提交几何与 metrics.json；公告面积文字值；仓库 brief/site-package。

图 1 一页总览：三环分带、推定主脊、33 个近端单元与三处重点区域

- 提交范围平均宽度 1,188 米（半宽 594 米），99.98% 位于推定主脊 650 米以内
- 近端带（0–300 米）占 51.1%，是全长最主要的工作面
- 33 个近端单元：每 300 米一个，各配一处近端客厅与一条 24 小时通道

京张近端 / THE NEAR SIDE —— 最后三百米 • A3 文本

把公园边界外的最后 300 米，做成百年京张 AI 创新带的第一资产。全部内容为概念建议、参考方案，不替代法定规划。

百年京张AI创新带城市设计开源征集 · 概念建议 / 参考方案


用地结构与三环分带

用地为提交范围的完整剖分（无缺口、无重叠）。三环按距公园边界面的距离划分：近端带 0–300 米、渗透环 300–500 米、外联环 500 米以外，并逐环对应不同的更新动作与分期。

判准：任何宣称「AI 进城」的空间动作，必须先说明它如何从公园边界面走到一个普通人能走到的门口。近端三约：可穿越 • 可关闭 • 可计数

图 2 用地结构与三环分带：提交范围的完整剖分，无缺口、无重叠

- 用地剖分无缺口、无重叠：139 个地块覆盖提交范围 100%
- 公园绿地 291.5 ha 为最大单一用地（25.5%）；留白用地 18.0 ha 用于受控测试
- 三环占比：近端带 51.1%、渗透环 34.1%、外联环 14.8%

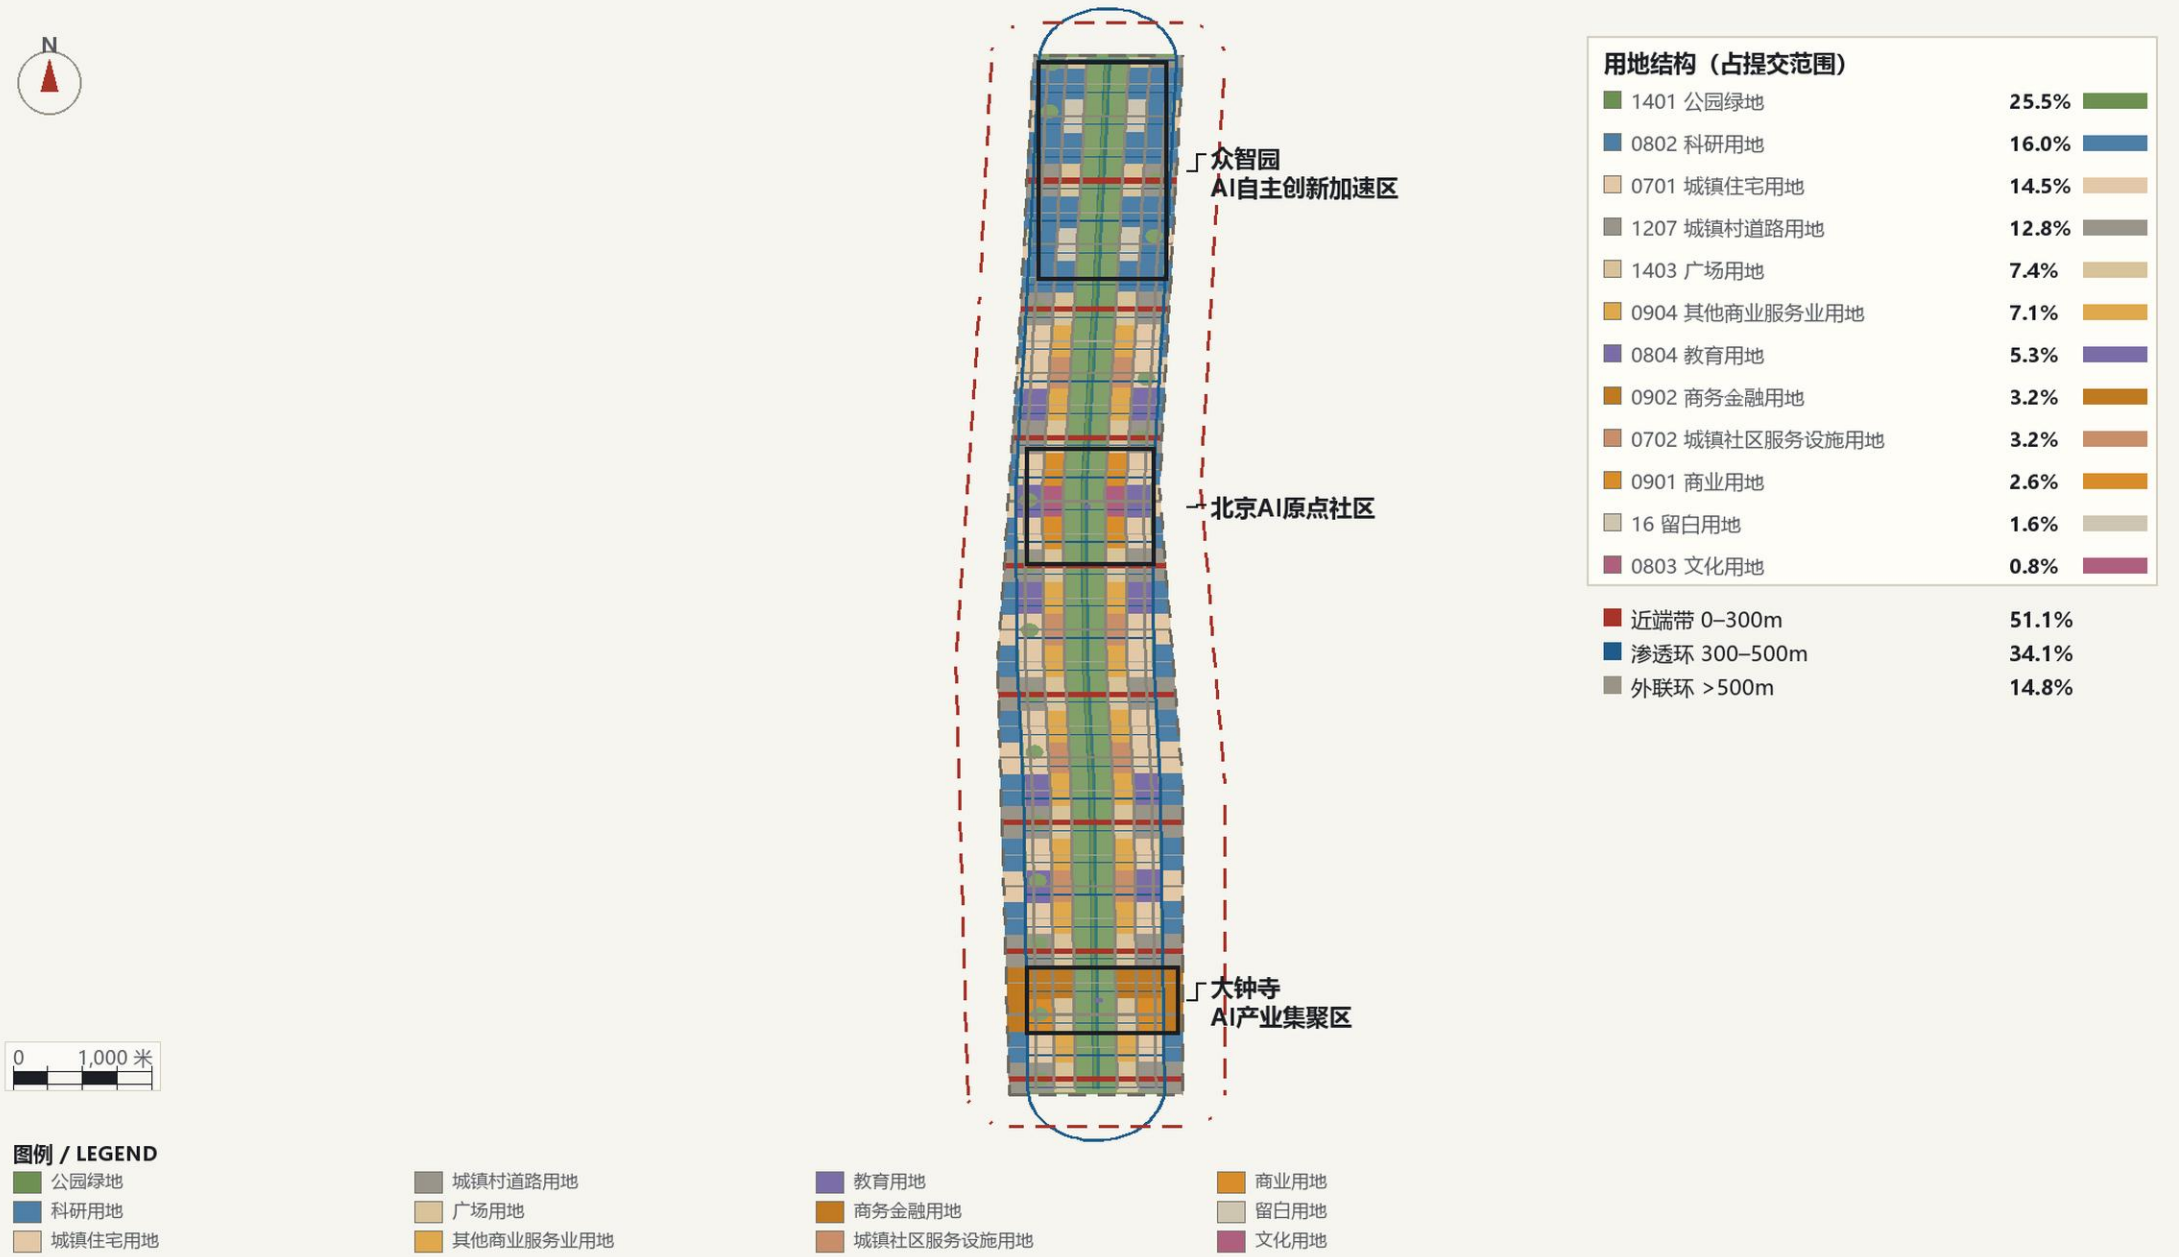

注：本包全部空间几何采用仓库临时粗略边界（official_boundary=false, geometry_role=provisional_constraint, boundary_precision=provisional_rough），仅用于生成、自检、可视化与设计讨论，不得作为官方红线、审批依据或精确面积依据。仓库背景核对显示：临时边界与公告命名街道的 OSM 实测中线存在 533–898 米（均值 667 米）同向偏移；图中推定主脊为方法演示用的量算基准线，不等于京张遗址公园实际线位。官方 polygon 与公园边界面发布后，全部图层与指标须整体重算，不得只替换单个文件。来源：本方案提交几何与 metrics.json；公告面积文字值；仓库 brief/site-package。

京张近端 / THE NEAR SIDE —— 最后三百米 • A3 文本



把公园边界外的最后 300 米，做成百年京张 AI 创新带的第一资产。全部内容为概念建议、参考方案，不替代法定规划。

百年京张AI创新带城市设计开源征集 · 概念建议 / 参考方案

三处重点区域详细设计

三处重点区各自解决一种「最后三百米」：北端是新建区的接口预留，中段是院所围墙的开门，南端是轨道站与商圈的到站最后一段。

判准：任何宣称「AI 进城」的空间动作，必须先说明它如何从公园边界面走到一个普通人能走到的门口。近端三约：可穿越 • 可关闭 • 可计数

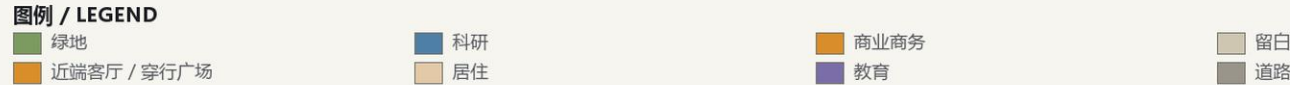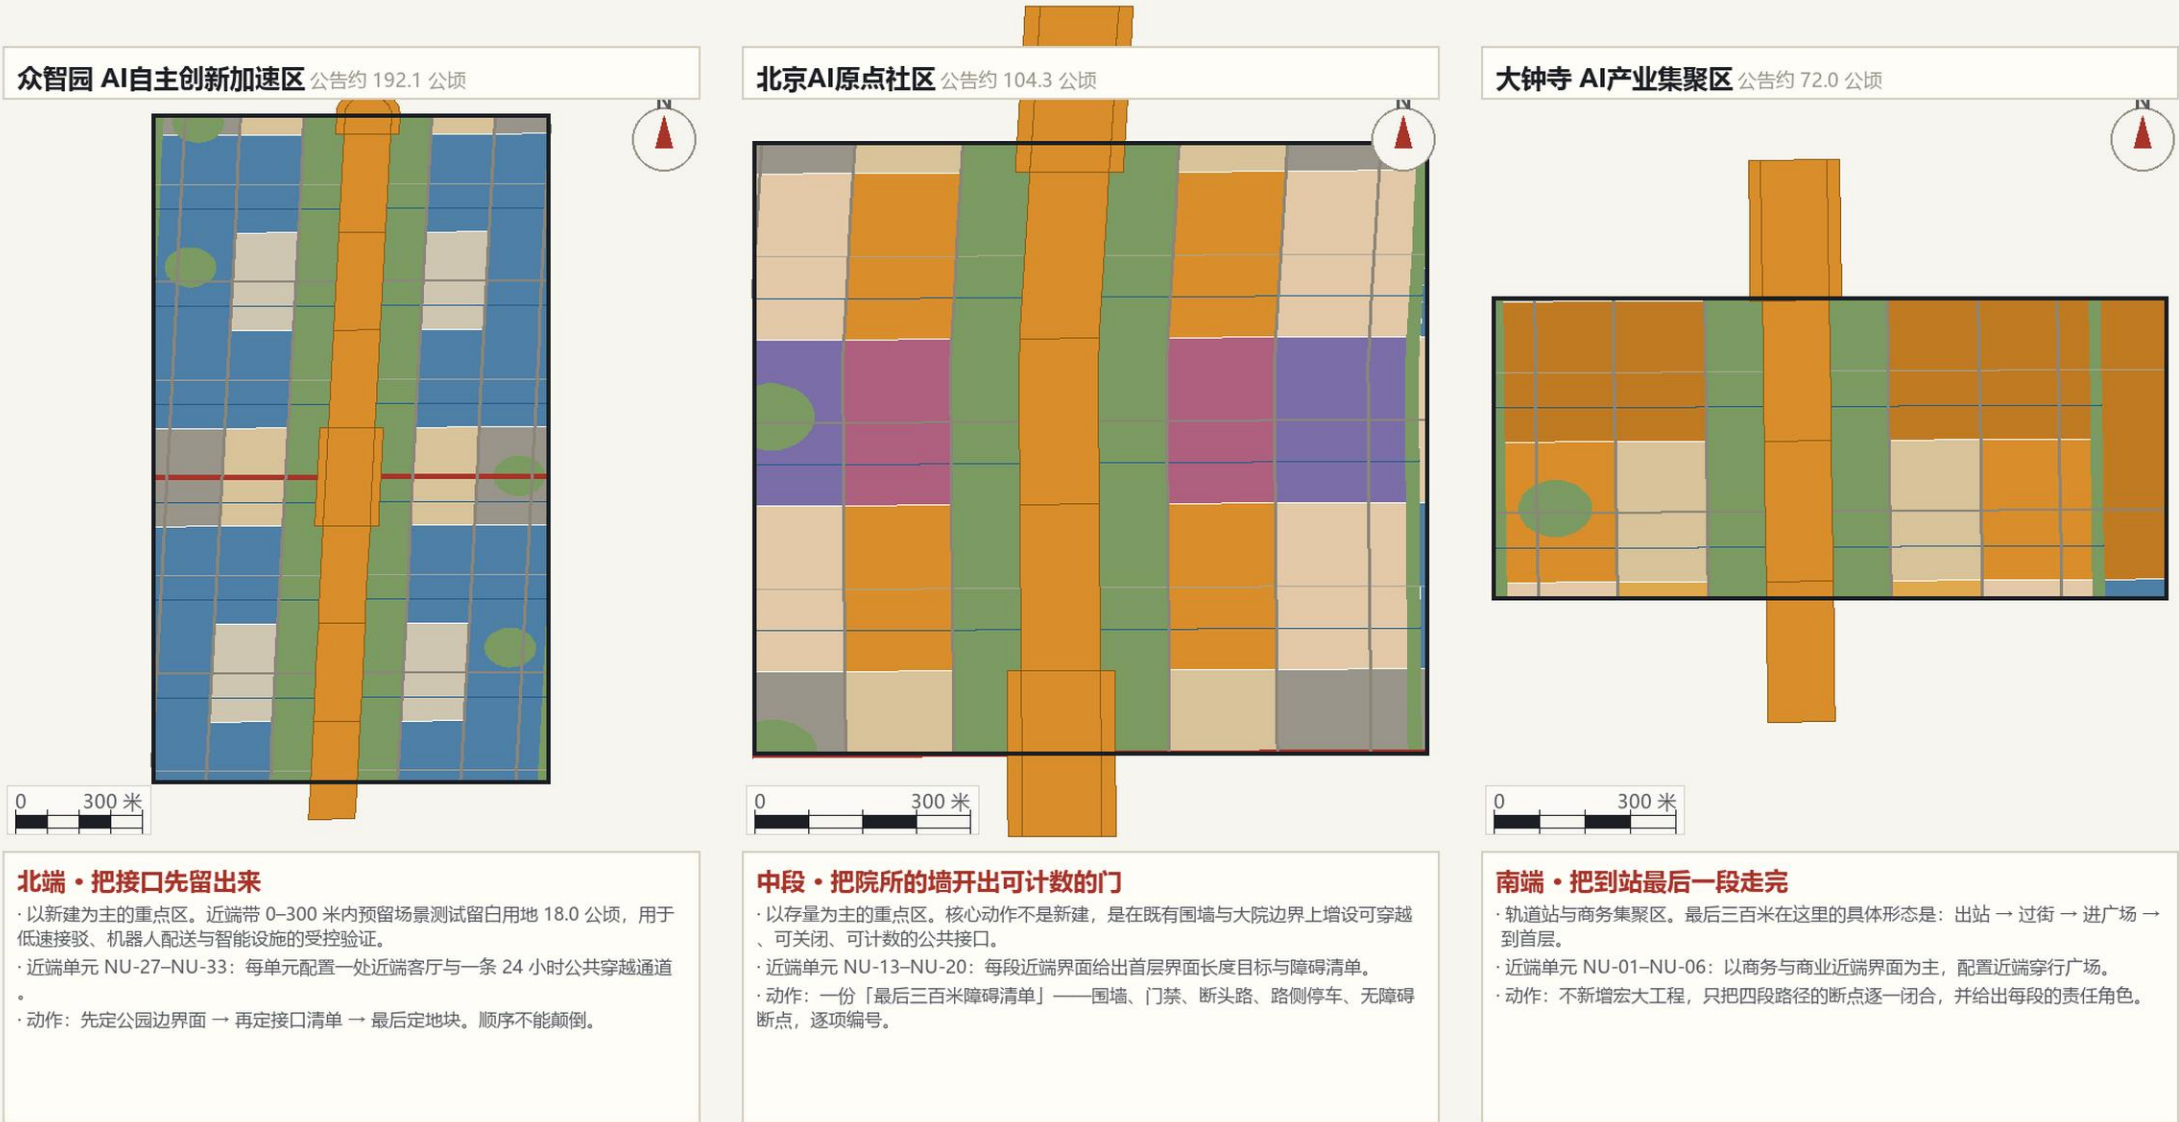

注：本包全部空间几何采用仓库临时粗略边界（official_boundary=false, geometry_role=provisional_constraint, boundary_precision=provisional_rough），仅用于生成、自检、可视化与设计讨论，不得作为官方红线、审批依据或精确面积依据。仓库背景核对显示：临时边界与公告命名街道的 OSM 实测中线存在 533–898 米（均值 667 米）同向偏移；图中推定主脊为方法演示用的量算基准线，不等于京张遗址公园实际线位。官方 polygon 与公园边界面发布后，全部图层与指标须整体重算，不得只替换单个文件。来源：本方案提交几何与 metrics.json；公告面积文字值；仓库 brief/site-package。

图 3 三处重点区域详细设计：北端留出接口、中段开出院门、南端走到首层

- 北端众智园 192.9 ha：预留接口，先定公园边界面、再定接口清单、最后定地块
- 中段 AI 原点社区 104.3 ha：在既有围墙上增设可穿越、可关闭、可计数的门
- 南端大钟寺 72.0 ha：出站 → 过街 → 进广场 → 到首层，四段路径逐一闭合

京张近端 / THE NEAR SIDE —— 最后三百米 • A3 文本

把公园边界外的最后 300 米，做成百年京张 AI 创新带的第一资产。全部内容为概念建议、参考方案，不替代法定规划。

百年京张AI创新带城市设计开源征集 · 概念建议 / 参考方案


慢行、蓝绿与近端断面

设计路网密度 9.80 km/km²，绿脊连续慢行主脉 9,608 米，42 处公共接口，33 个近端单元。断面图把「最后三百米」拆成五段可量测的带。

判准：任何宣称「AI 进城」的空间动作，必须先说明它如何从公园边界面走到一个普通人能走到的门口。近端三约：可穿越 • 可关闭 • 可计数

图 4 慢行、蓝绿与近端断面：最后 300 米被拆成五段可量测的带

- 设计路网密度 12.9 km/km²，其中机动车通行道路 8.4 km/km²
- 绿脊慢行主脉 9.6 km、42 处公共接口、33 个近端单元
- 最后 300 米被拆成五段可量测的带，全带半宽仅 594 米

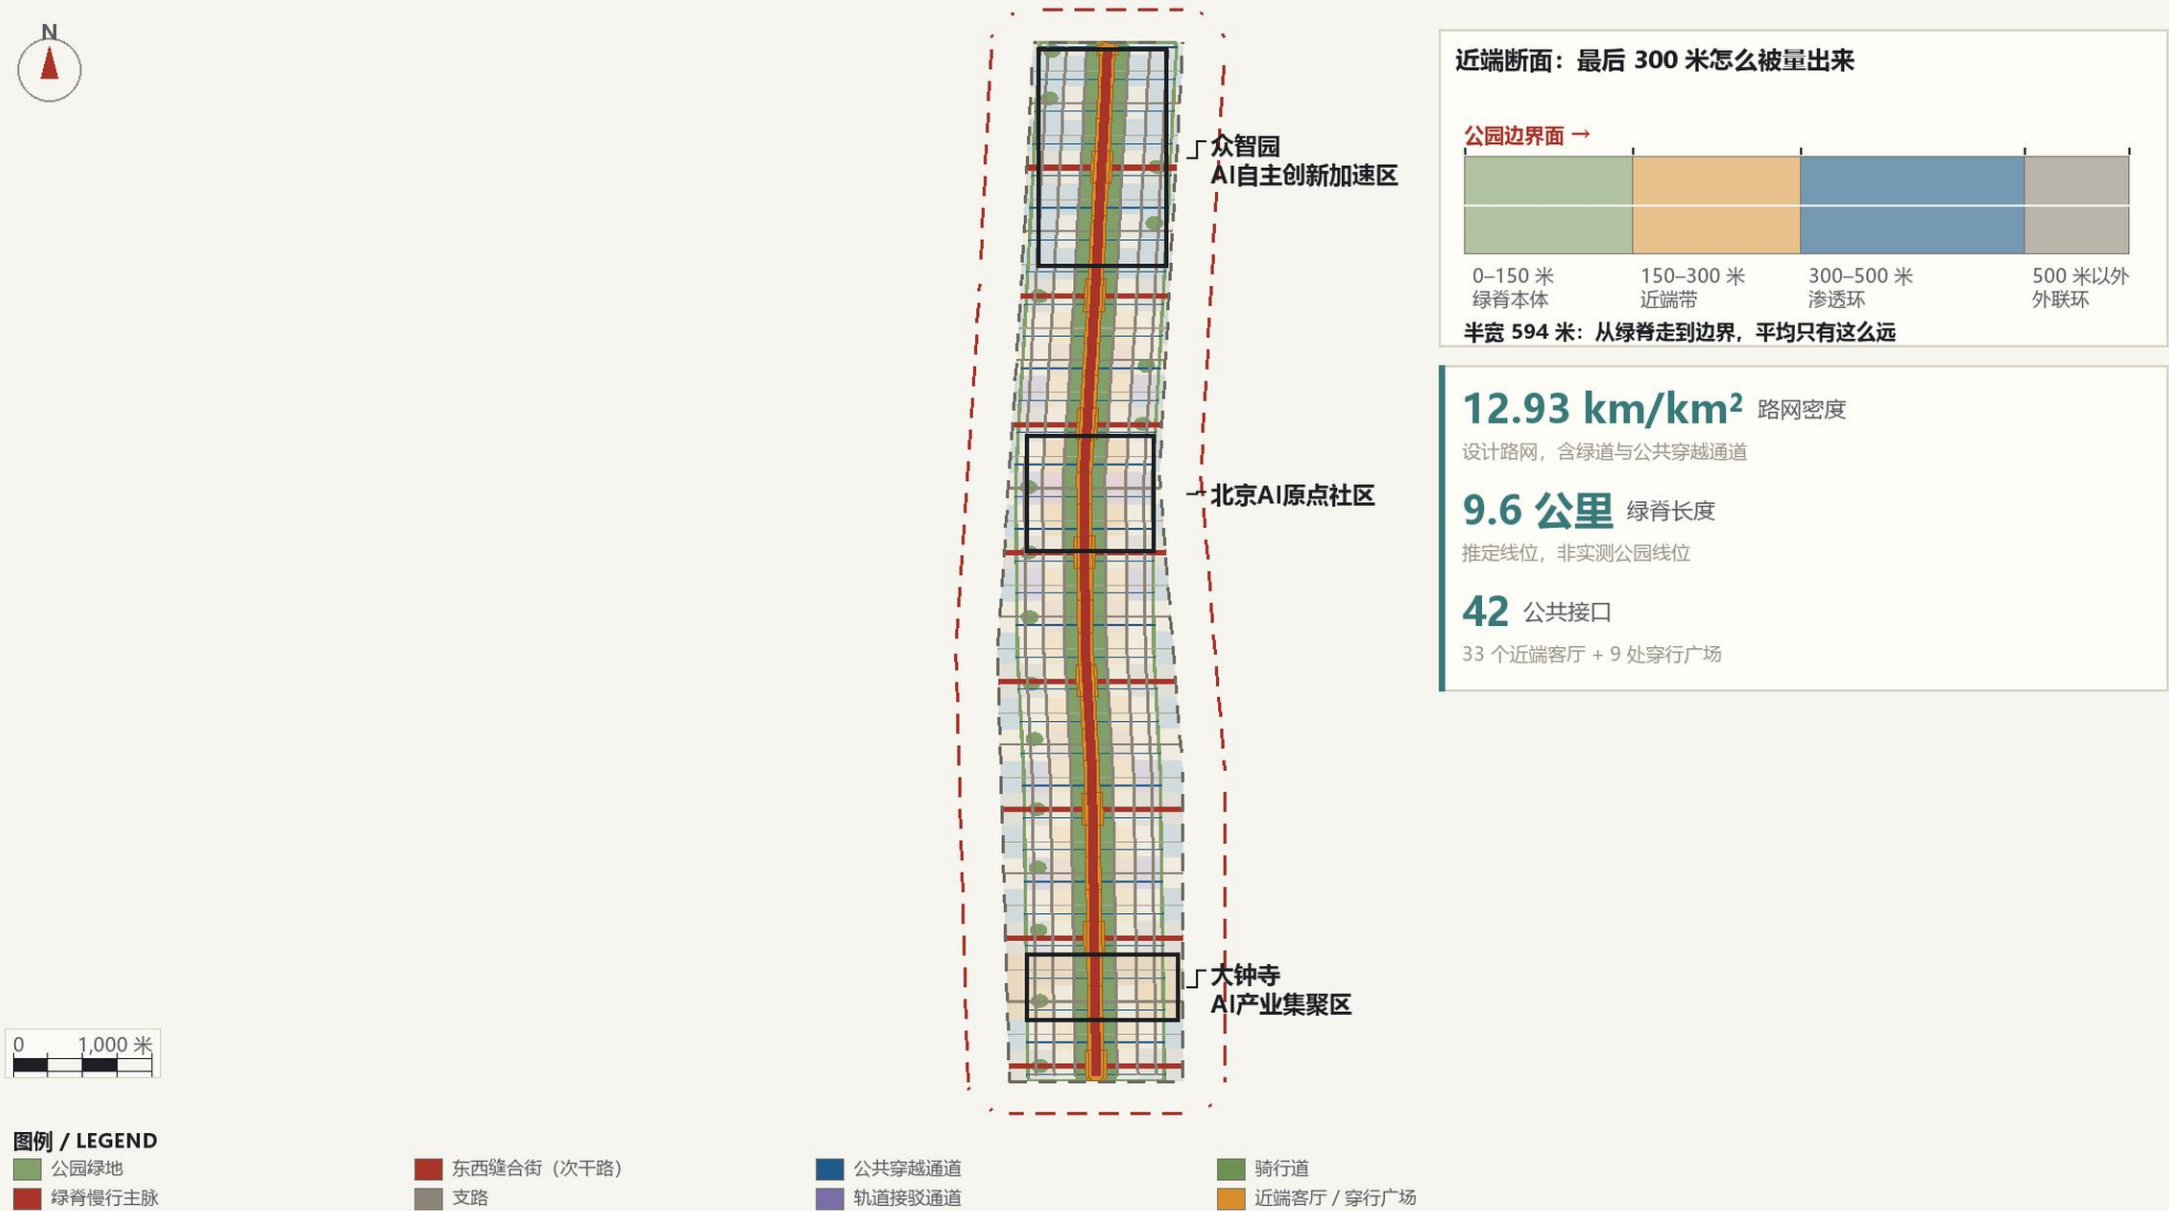

注：本包全部空间几何采用仓库临时粗略边界（official_boundary=false, geometry_role=provisional_constraint, boundary_precision=provisional_rough），仅用于生成、自检、可视化与设计讨论，不得作为官方红线、审批依据或精确面积依据。仓库背景核对显示：临时边界与公告命名街道的 OSM 实测中线存在 533-898 米（均值 667 米）同向偏移；图中推定主脊为方法演示用的量算基准线，不等于京张遗址公园实际线位。官方 polygon 与公园边界面发布后，全部图层与指标须整体重算，不得只替换单个文件。来源：本方案提交几何与 metrics.json；公告面积文字值；仓库 brief/site-package。

京张近端 / THE NEAR SIDE —— 最后三百米 • A3 文本

把公园边界外的最后 300 米，做成百年京张 AI 创新带的第一资产。全部内容为概念建议、参考方案，不替代法定规划。

百年京张AI创新带城市设计开源征集 · 概念建议 / 参考方案

核心指标复算与证据链

三项 formal 核心视觉指标均由本包提交的 site_boundary、green_space 与 public_space 几何复算得出，并与 visual/index.html 的数值一致；依赖未公开管控条件的指标一律记为待正式数据补齐。

判准：任何宣称「AI 进城」的空间动作，必须先说明它如何从公园边界面走到一个普通人能走到的门口。近端三约：可穿越 • 可关闭 • 可计数

提交范围面积

11.41 km²

metric: site_area_sqm
公告约 11.4 km²；本包复算 11.41 km²

绿地率

30.51%

metric: green_ratio
绿脊 + 口袋公园 + 林荫防护带

公共空间比例

10.24%

metric: public_space_ratio
33 个近端客厅 + 9 处穿行广场

可复算指标（全部由本包 geometry/ 与 metrics.json 复算）				
site_area_sqm	1,141.3	ha	known	提交边界复算
green_ratio	30.5%	ratio	known	green_space / site_area
public_space_ratio	10.2%	ratio	known	public_space / site_area
building_footprint_area_sqm	197.8	ha	known	概念体量，低置信度
road_network_density_km_per_sqkm	12.9	km/km ²	known	设计中心线总长 / 面积
near_unit_count	33	个	known	每 300 米一个
mean_distance_to_spine_m	295.7	m	known	面积加权
share_within_300m	51.1%	ratio	known	近端带占比
equivalent_access_coverage_ratio	100.0%	ratio	known	24 小时通道覆盖的近端单元 / 近端单元总数
human_fallback_scenario_ratio	66.7%	ratio	known	含人工复核节点的场景卡 / 场景卡总数 = 8 / 12
floor_area_ratio	待正式数据补齐	ratio	unknown	官方控规未公开，待正式数据补齐
building_height_m	待正式数据补齐	m	unknown	官方控规未公开，待正式数据补齐

证据链：从公开资料到可复算结论

1

公开资料分级 source_registry

2

官方/临时边界 → site_boundary

3

分层生成 geometry/*.geojson

4

EPSG:4548 面积复算 → metrics.json

5

三矩阵覆盖 → 六项智能体任务

6

四门自检 → 可读图件与网页

任一环节依赖未公开资料时，结论降为背景或临时，不升级为正式结论。

精度警示：本包全部空间几何基于仓库临时粗略边界；组织方缺少官方 polygon 不阻断内容评分，但本包不主张其面积等于官方精确面积。官方数据发布后整体重算。

注：本包全部空间几何采用仓库临时粗略边界（official_boundary=false, geometry_role=provisional_constraint, boundary_precision=provisional_rough），仅用于生成、自检、可视化与设计讨论，不得作为官方红线、审批依据或精确面积依据。仓库背景核对显示：临时边界与公告命名街道的 OSM 实测中线存在 533–898 米（均值 667 米）同向偏移；图中推定主脊为方法演示用的量算基准线，不等于京张遗址公园实际线位。官方 polygon 与公园边界面发布后，全部图层与指标须整体重算，不得只替换单个文件。来源：本方案提交几何与 metrics.json；公告面积文字值；仓库 brief/site-package。

图 5 核心指标复算与证据链：从公开资料到可复算结论

- 三项 formal 核心指标由提交几何在 EPSG:4548 下复算得出
- 可复算指标逐项给出公式、来源文件与状态，未知项写明待补资料
- 依赖未公开管控条件的指标一律记为 unknown，不冒充已知

一页摘要 / Executive Summary

把公园边界外的最后 300 米，做成百年京张 AI 创新带的第一资产。全部内容为概念建议、参考方案，不替代法定规划。

一页摘要 / Executive Summary

- 判准：任何宣称「AI 进城」的空间动作，必须先说明它如何从公园边界面走到一个普通人能走到的门口。近端三约：可穿越 · 可关闭 · 可计数。
- 面积加权平均到主脊距离 295.7 米；近端带（0–300 米）占 51.1%，渗透环（300–500 米）占 34.1%，外联环（>500 米）占 14.8%。
- 因此，本方案不把「最后三百米」当作一句口号，而把它定义为一条可以从提交几何复算出来的带，并以三环组织用地、路网、公共空间与分期。
- 三项 formal 核心视觉指标：提交范围面积 11.41 km²；绿地率 33.6%；公共空间比例 10.2%。
- 依赖未公开管控条件的指标（容积率、建筑高度、建筑密度、退线、权属、轨道站点坐标、文保与蓝线）一律记为待正式数据补齐。

完整叙述、全部 54 项指标与可复算台账见 report/proposal.html 与 visual/index.html；33 个单元的机器可读台账见 visual/assets/near_side_units.json。

更新项目清单 / Renewal Projects

把公园边界外的最后 300 米，做成百年京张 AI 创新带的第一资产。全部内容为概念建议、参考方案，不替代法定规划。

更新项目清单 / Renewal Projects

- R0 公园边界面调查 —— 全带，0–6 个月，规划主管部门 + 测绘单位；所有后续项目的依赖。
- R1 近端单元台账 —— 33 个 NU，一期，街道 + 社区 + AI 助手。
- R2 无障碍断点修复 —— 优先 NU-13–NU-20，一期，街道 + 权属主体。
- R3 低速机器人测试街 —— 众智园测试街，一期，管委会 + 企业；连续两期未通过安全测试即停止。
- R4 院所公共接口改造 —— AI 原点社区，二期，高校/院所 + 街道；任一主体反对则跳过该单元。
- R5 人才公寓与混合街区 —— 渗透环，二期，投资/运营主体。
- R6 大钟寺站前到站厅 —— 大钟寺，二期，轨道运营方 + 街道。
- R7 区域协同接口 —— 三处重点区外联环，三期，区政府 + 区域平台。

完整叙述、全部 54 项指标与可复算台账见 report/proposal.html 与 visual/index.html；33 个单元的机器可读台账见 visual/assets/near_side_units.json。

风险与合规 / Risk and Compliance

把公园边界外的最后 300 米，做成百年京张 AI 创新带的第一资产。全部内容为概念建议、参考方案，不替代法定规划。

风险与合规 / Risk and Compliance

- 数据边界：全部空间数据来自仓库临时边界或本方案在其上的推导；未使用非公开规划图件、非官方 CAD/GIS 或内部数据。
- 版权：图件、Logo 与文案均由本方案代码或作者生成；未使用未经授权的字体、图片、商标、人物肖像或企业标识。
- 隐私：AI 场景不采集人脸识别数据、个人行踪或健康敏感信息；每个 AI 服务保留人工或纸质等价路径。
- 官方批准与实施承诺：所有空间落地建议均为概念建议、参考方案或可供专业团队深化研究，不替代正式规划，不构成政府审定结论。
- 待补资料：官方边界 polygon、公园边界面精确线位、官方控规条件、土地权属、文保与蓝线、轨道站点与出入口坐标。

完整叙述、全部 54 项指标与可复算台账见 report/proposal.html 与 visual/index.html；33 个单元的机器可读台账见 visual/assets/near_side_units.json。