

复线 DOUBLE TRACK


每一条自动化旁边都有一条人工线 · 百年京张AI创新带城市设计 · 展板 1 / 2

复线 · 京张智能体协同带总体概念

DOUBLE TRACK

海淀 · 京张铁路遗址公园沿线 | 设计范围 11.4 km² · 统筹研究范围 43.6 km² | 概念建议方案，非官方审定结论

FIG 01 / 05 site-overview

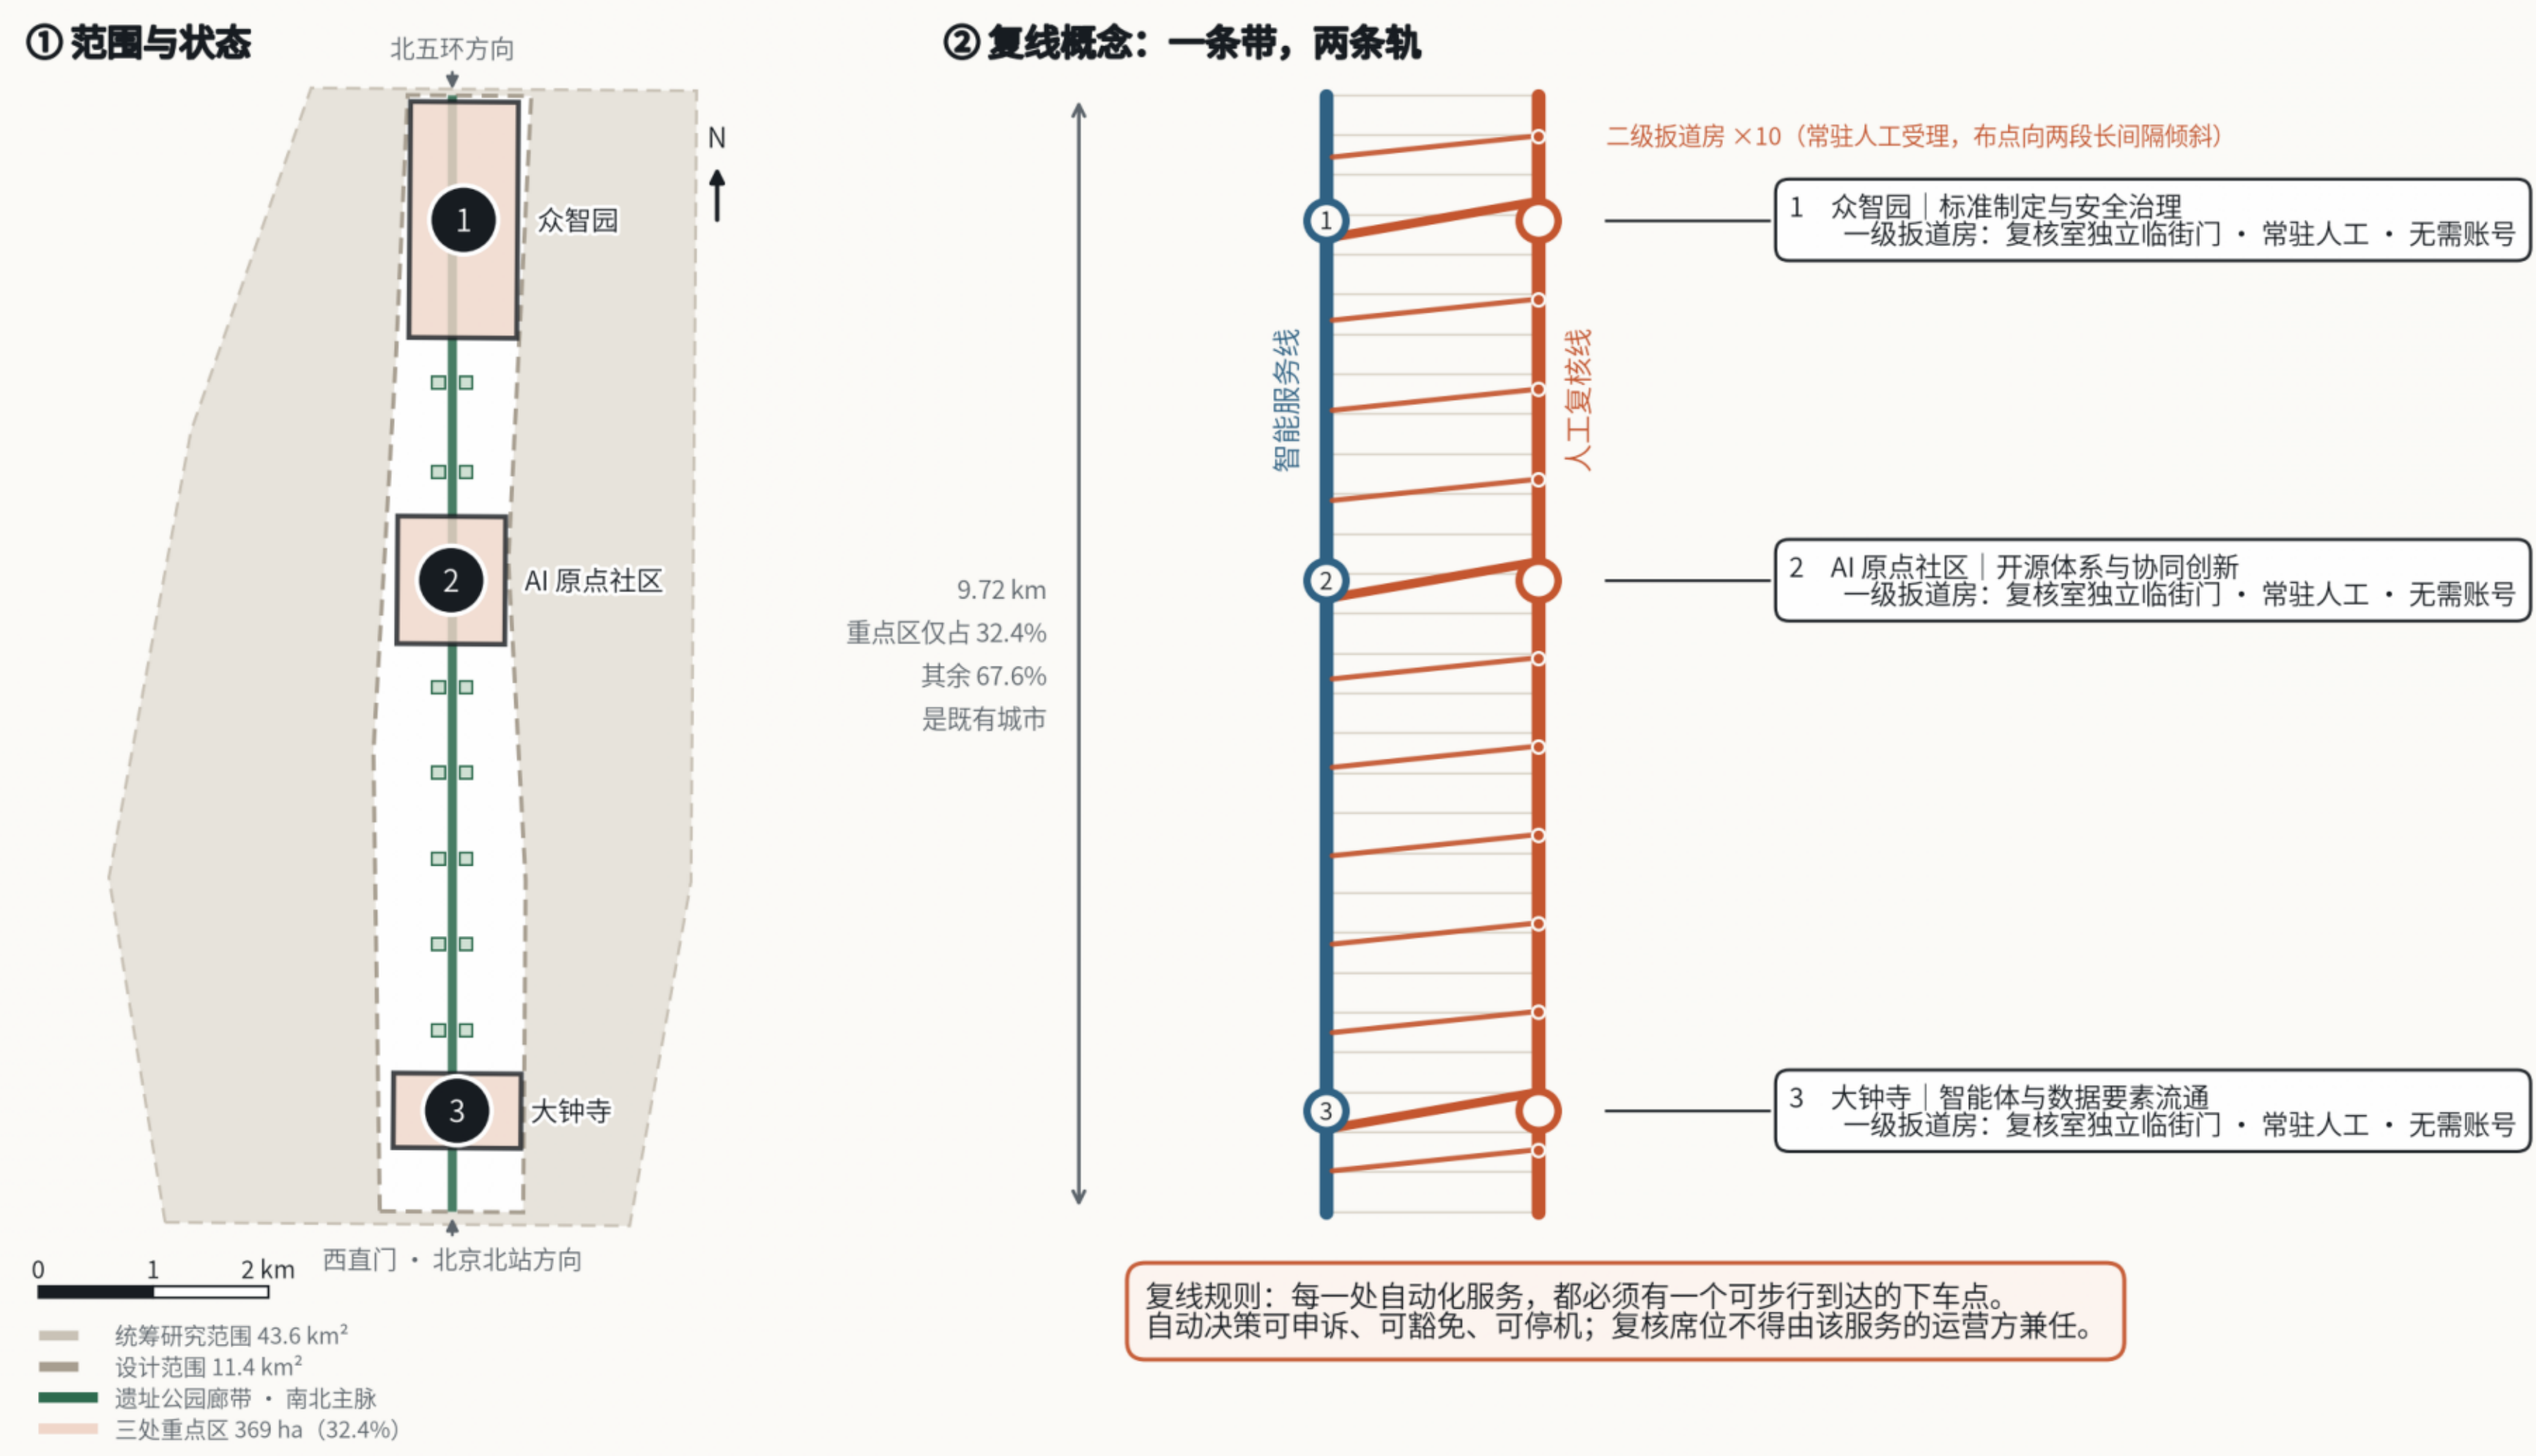

临时边界说明：三层范围与三处重点区均为组织方提供的 provisional 替代边界（虚线表达），非官方红线；取得正式图纸后需重算全部图层与指标。

复线 DOUBLE TRACK · rein-karthar


来源：DATA-SRC-PROVISIONAL-BOUNDARIES-20260605 (组织方临时替代边界) · DATA-SRC-OFFICIAL-ANNOUNCEMENT-20260605 (官方公告 1.3 / 1.4 / 1.5) | 本图由本方案 geometry/.geojson 与 metrics.json 衍生并投影至 EPSG:4548；权威数据以 GeoJSON / JSON 为准，图面为解释层。

复线 · 空间结构与用地传导

SPATIAL STRUCTURE

五带断面贯通 9.72 km | 重点区与段间地带共用同一结构、装载不同内容 | 概念建议方案

FIG 02 / 05 land-use-structure

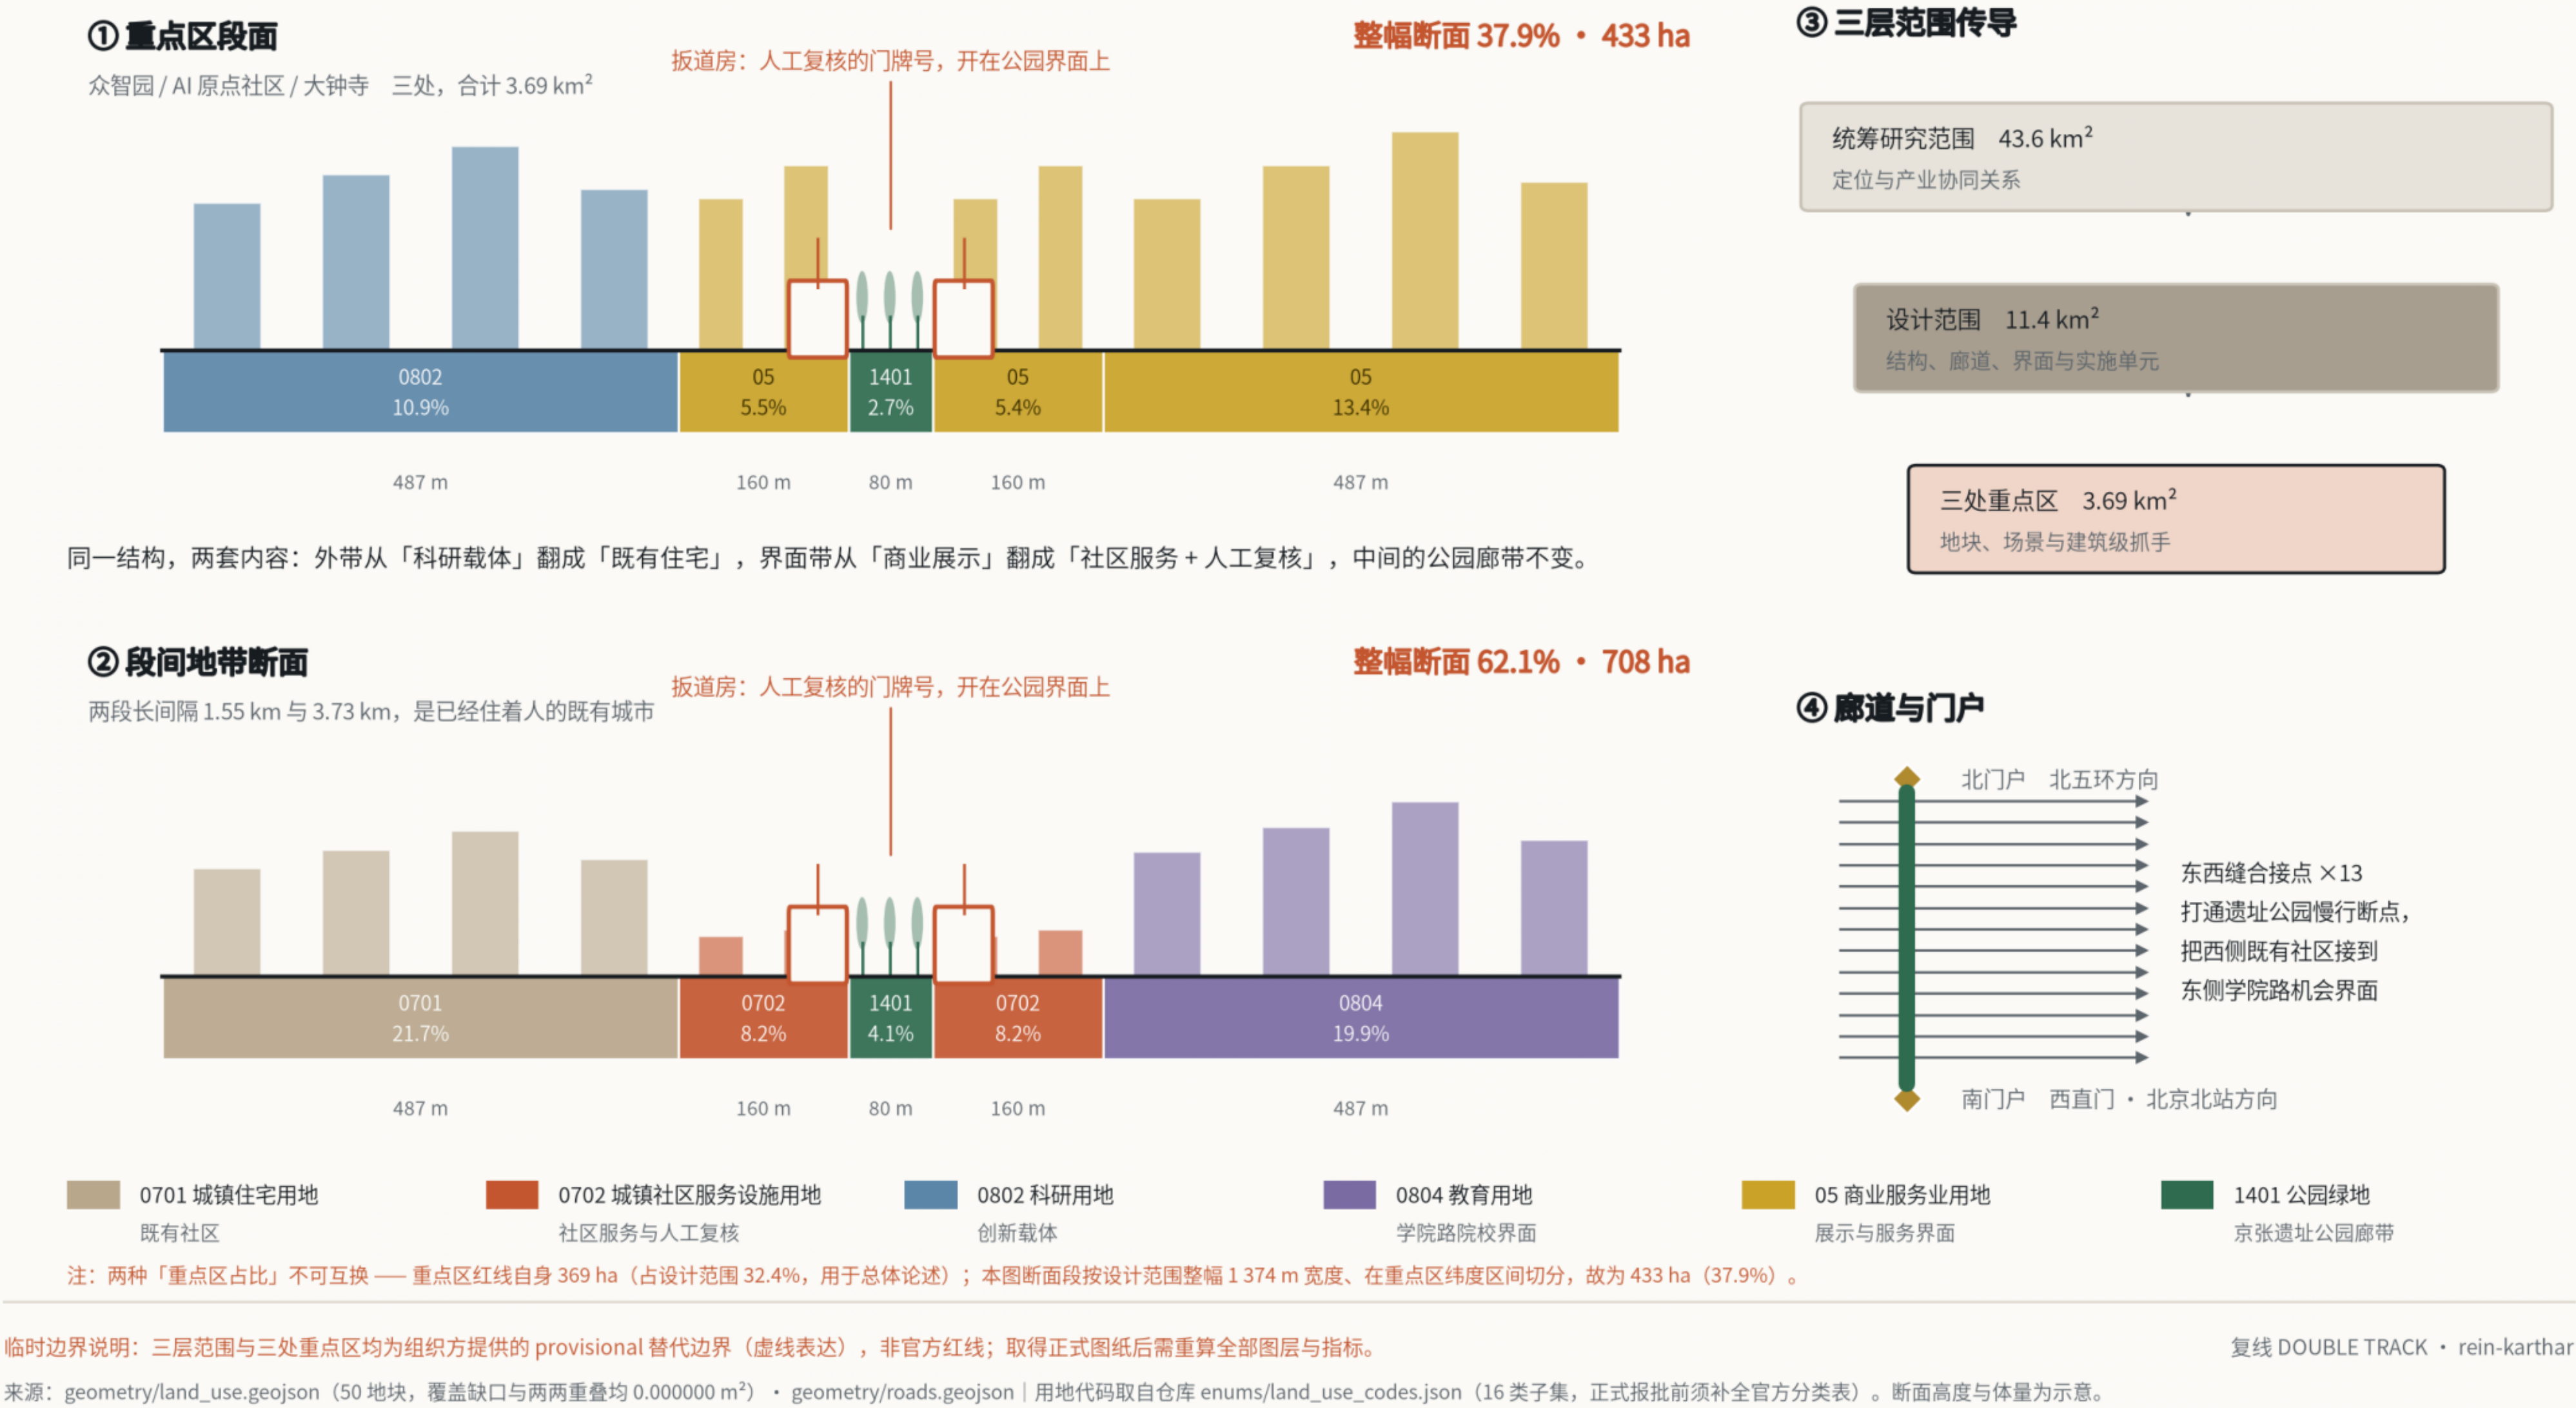


复线 DOUBLE TRACK · rein-karthar

复线 · 三处重点区：一条链，不是三个园区

THREE KEY AREAS

北端定标准 → 中段做开源 → 南端接市场 | 三区合计 369 ha | 项目抓手与风险条件逐区列出 | 概念建议方案

FIG 03 / 05 key-areas

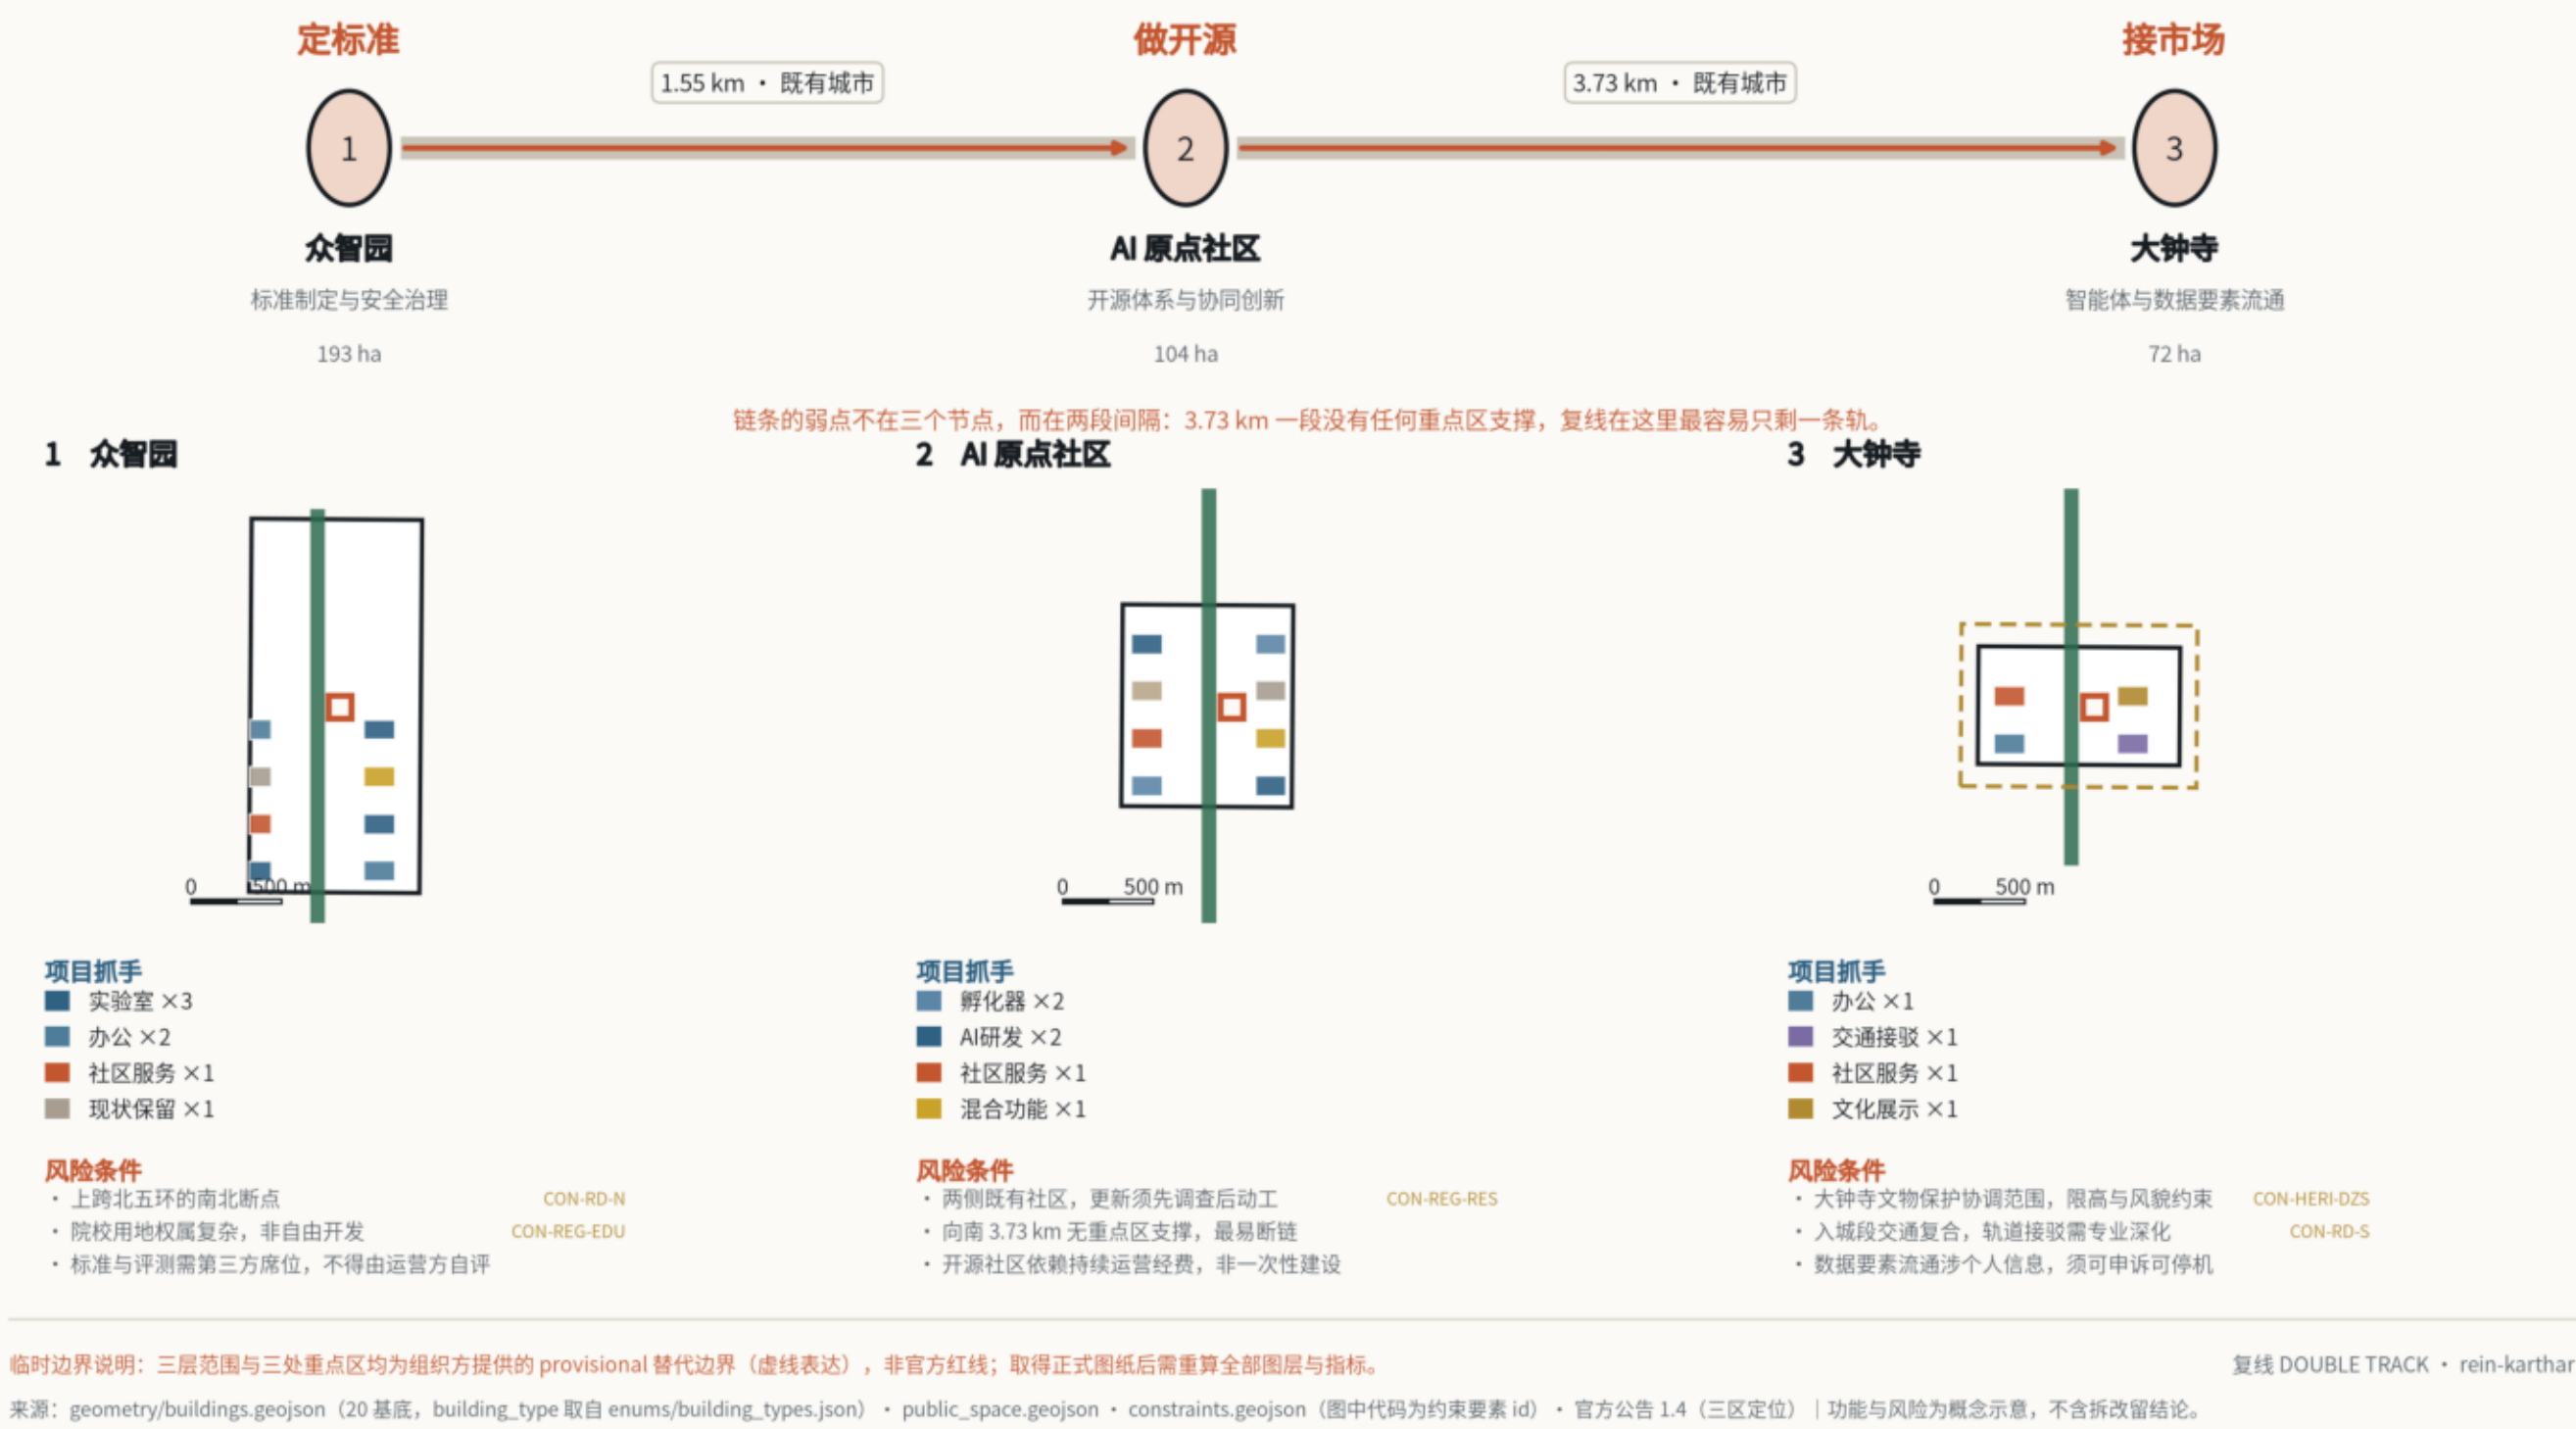

核心判断

· 场地是一条 9.72 公里的线，不是三个园区。

· 三处重点区占 32.36%，区间段 67.64%——设计重点在区间。

· 一条断面、两种载荷：重点区承载科研展示，区间段承载社区服务与人工复核。

· 一个系统不能充当自身失效的探测器：复核能力必须在构造上独立。

· 复核室另设独立临街门——投诉者不必穿过被投诉的系统才能开口。

证据链与实施


交通慢行 · 蓝绿系统 · 指标复算 · 分期 · 展板 2 / 2

复线 · 蓝绿网络与南北贯通

FIG 04 / 05 mobility-bluegreen

Blue-Green Network and North-South Continuity

复线 / DOUBLE TRACK BELT — 东西缝合节点与人工受理点沿遗址公园主脉布设；慢行断点按公告存在、位置未公布，表达为待实测区段。

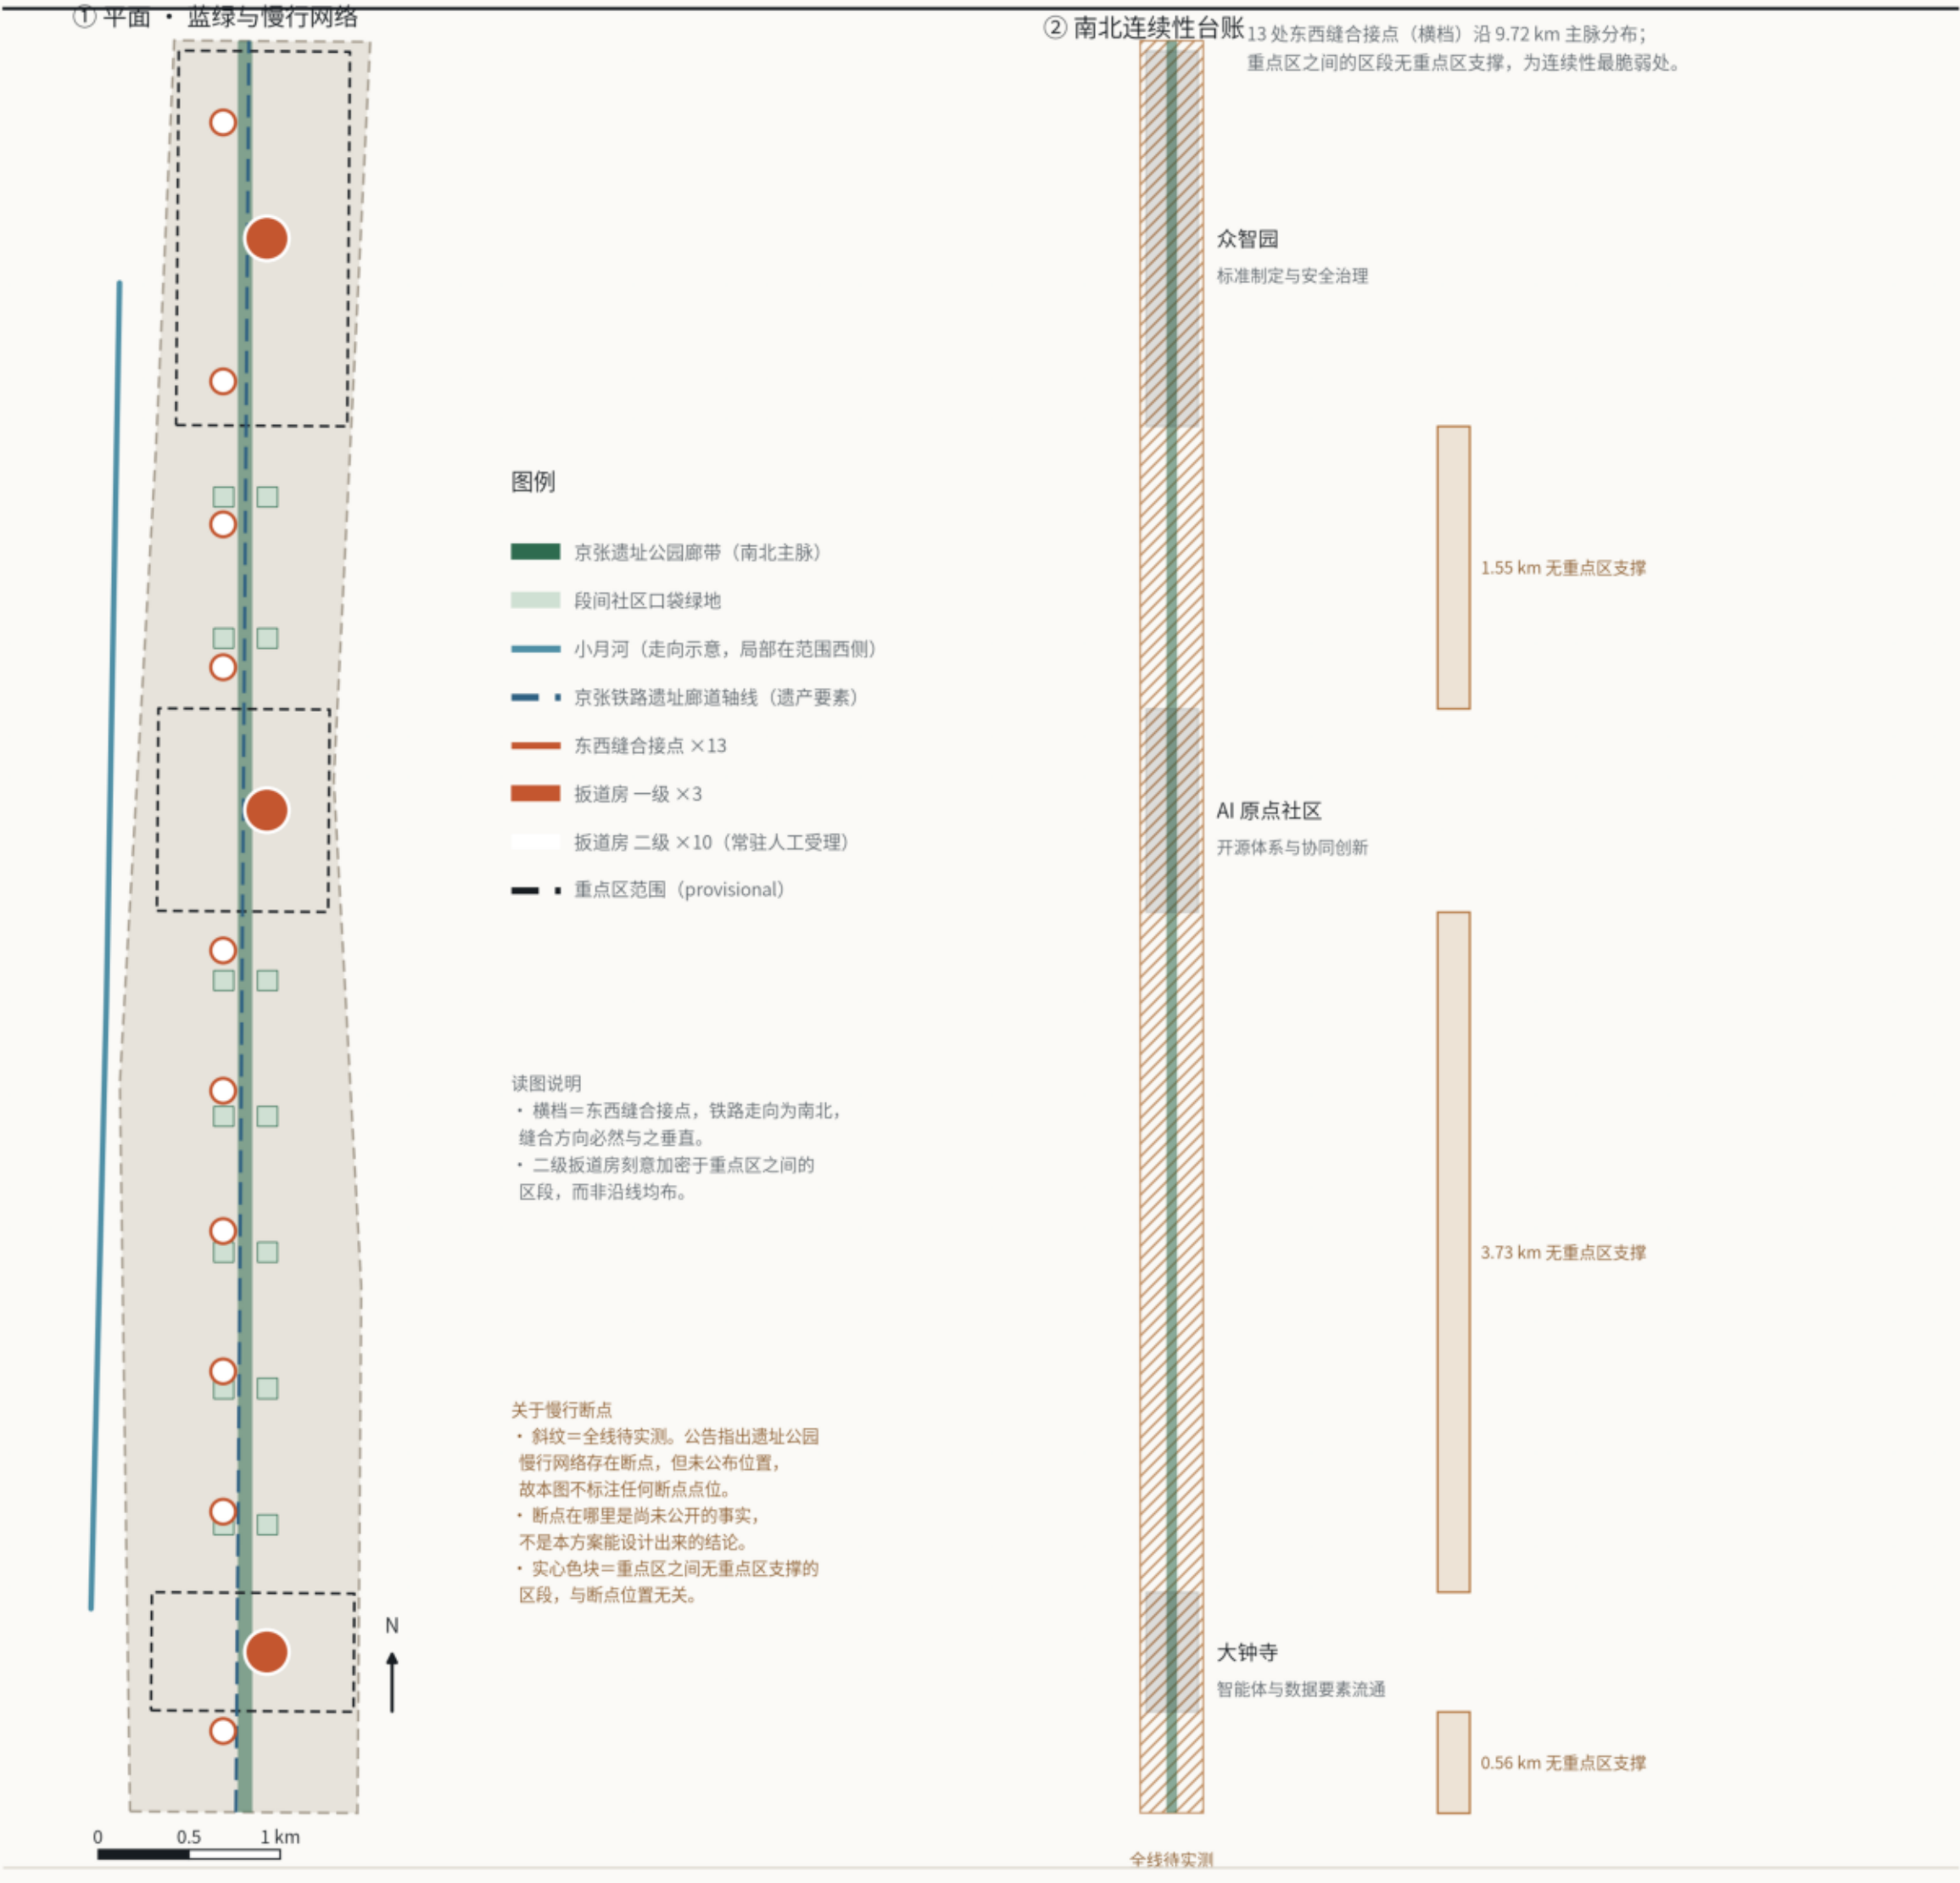

慢行贯通与东西缝合

- 南北贯通：9.72 公里慢行主线。公告指出遗址公园慢行网络存在断点，

但未公布位置——本方案将全线登记为「待实测」，不虚构断点坐标。

- 东西缝合：13 处渡线横跨走廊，按区间长度加密，而非均匀分布。

- 10 处二级板道房刻意布置在两段长区间内（1.55 km 与 3.73 km），

而不是集中在三处重点区——区间才是复核线最稀薄的地方。

- 蓝绿：公园带 80 米，两侧各 160 米绿带；

全部公共空间点位不需账号、不需扫码即可使用。

复线 · 指标来源与复算关系

FIG 05 / 05 metrics-evidence

METRICS · SOURCE, RECOMPUTATION, PENDING CONTROLS, SELF-CHECK

全部面积在 EPSG:4548 下由 GeoJSON 派生；每项指标附 formula 与 source_files。左列为证据层，中列为复算层，右列为两项独立校核、组织方待确认控规条件与自检登记。

证据层 GeoJSON	复算层 METRICS	校核 · 待确认 · 自检
9 个图层 · 权威数据	17 项 · 每项附 formula	独立复算与资料缺口
项目范围线 SITE_BOUNDARY 重点区域 KEY_AREA 用地分类 LAND_USE 建筑基底 BUILDING_FOOTPRINT 道路用地面 ROAD_AREA 绿地开敞空间 GREEN_SPACE 公共空间 PUBLIC_SPACE 分期范围 PHASE 约束要素 多类 合计 133 个要素 · 全部通过枚举与拓扑校验	范围 总体设计范围面积 11,412,825 m² 重点区数量 3 重点区面积合计 3,692,893 m² 重点区占比 0.3236 用地 分代码用地面积 11,412,826 m² 用地覆盖率 1.0000 强度 建筑基底面积 351,909 m² 建筑密度 0.0308 总建筑面积 2,490,577 m² 容积率(样本) 0.2182 绿地与公共空间 绿地面积 946,690 m² 绿地率 0.0829 公共空间面积 337,800 m² 公共空间占比 0.0296 道路 道路面积 539,609 m² 道路面积率 0.0473 实施 分期范围合计 11,357,123 m²	复算关系 · 与公告口径独立校核 总体设计范围 本方案复算 11,412,825 m² 公告 11,400,000 m² 偏差 0.11% 重点区域合计 本方案复算 3,692,893 m² 公告 3,684,000 m² 偏差 0.24% 校核对象为公告公布面积，非本方案自设目标值；临时边界口径下用于结构判断，不作为面积结论。 待确认控规指标 · 组织方资料缺口 容积率 missing · 最终成果必需 建筑高度 missing · 最终成果必需 建筑密度 missing · 最终成果必需 绿地率 missing · 最终成果必需 建筑退线 missing · 最终成果必需 自检登记 self_check.json BOUNDARY_TRUST pass KEY_AREAS_TRUST pass LAND_USE_TOPOLOGY pass VISUAL_STATIC pass PROFESSIONAL_EVIDENCE pass
指标为概念建议阶段的复算值；官方红线与法定控规条件下发后须整体复算。		复线 DOUBLE TRACK · rein-karthar
来源：[source:SITE-PACKAGE] 枚举与范围登记 · [source:OFFICIAL-ANNOUNCEMENT] 公布面积 · 本方案 geometry/"-geojson 与 metrics.json (EPSG:4548 复算)		

分期原则：先建区间，后建节点

- 一期：三处一级板道房与所在重点区界面。

- 二期：打通区间段二级驻点与 13 处跨线缝合点。

- 三期：两端地标节点与全线风貌整备。

- 常规做法先做三处重点区，会让区间段全程处于「有自动化、无复核线」的状态。

六项智能体任务回应

agent.1 命名与视觉：复线／板道房／渡线／换线日；蓝线自动、橙线人工，永不合并为一色。

agent.2 生态：六例全球片区只取机制、不取数字；三区成链——定标准 → 做开源 → 接市场。

agent.3 场景：12 张场景卡强制四列（可步行地址／失效承担者／成熟度／裁决方）+8 组画像，5 组为非人才。

agent.4 公共空间：全部点位不需账号扫码；三处朝圣地标；贡献墙记录含未入选方案且可增补。

agent.5 文化：人字形展线在青龙桥、距场地 60 公里以上，不挪用为场地母题。

agent.6 运营：年度「换线日」公开评测，月度「复议日」当面复核，另设投诉→修订的反向路径。